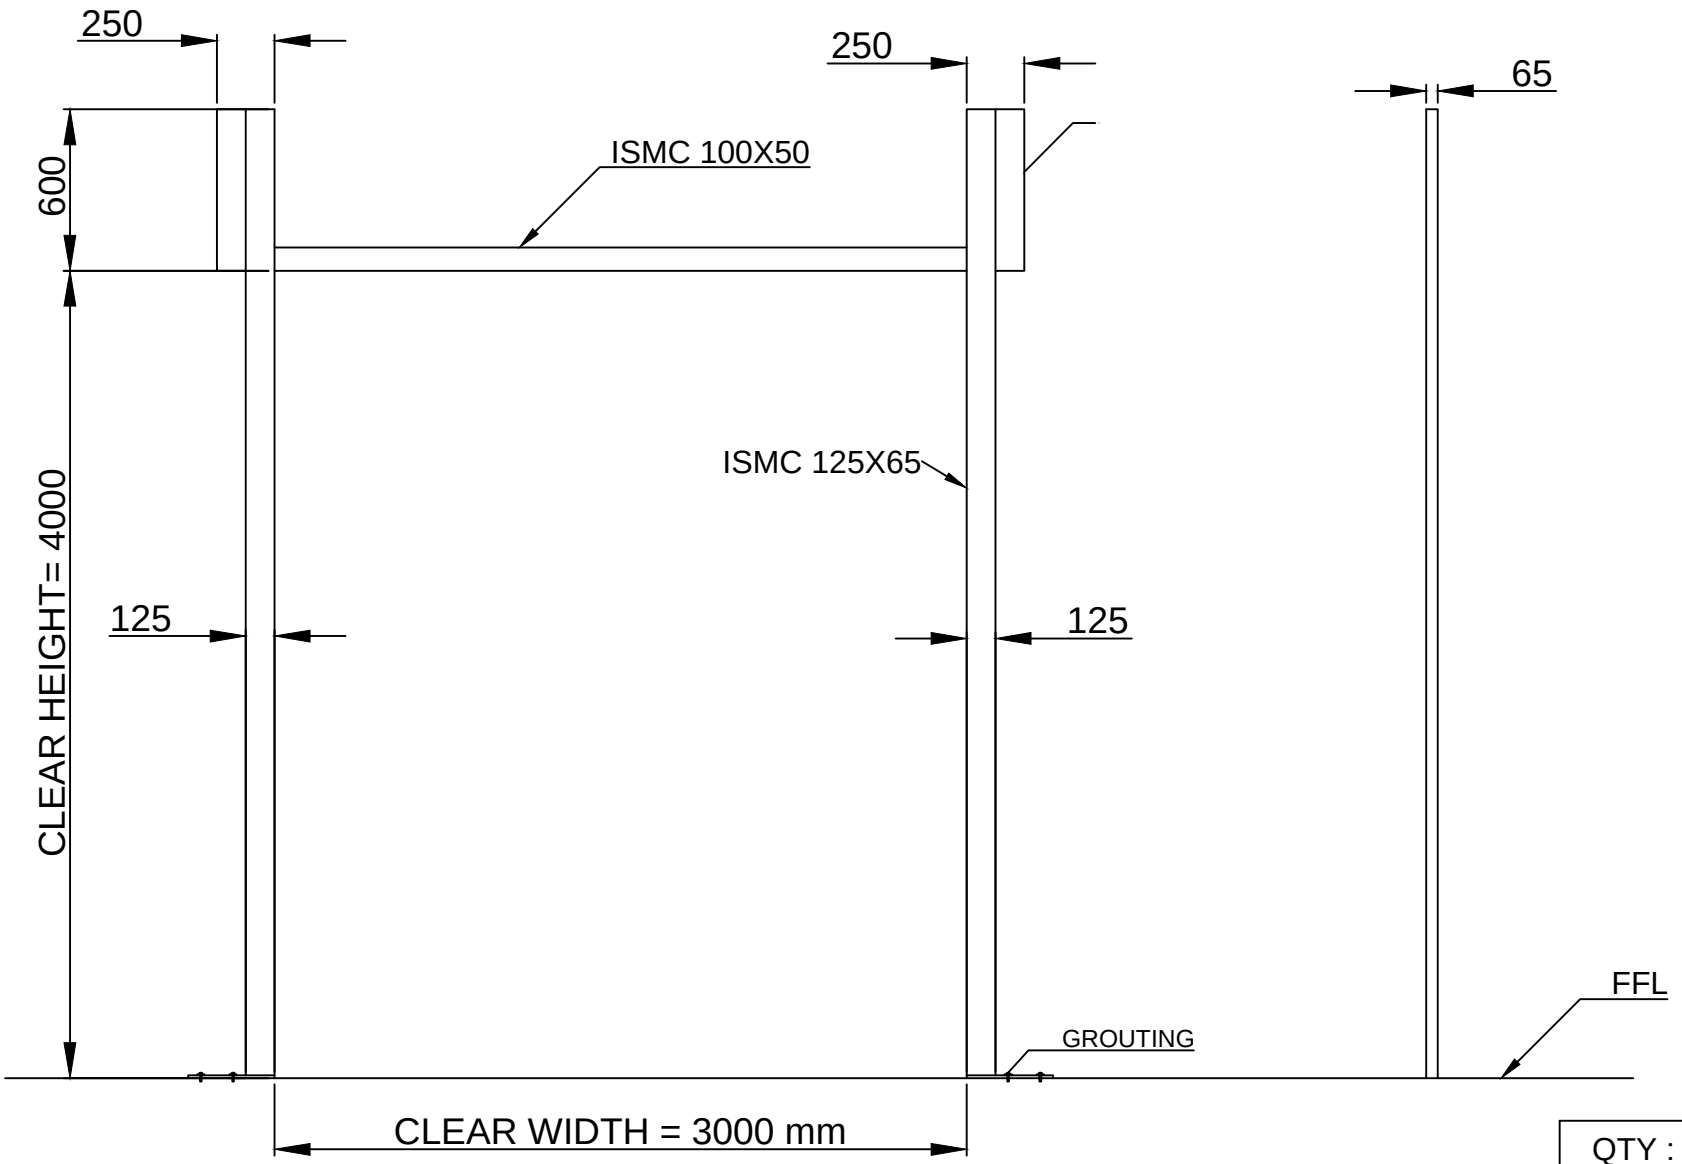

QTY : 1 NO

This drawing & design is the property of NIHVA TECHNOLOGIES. Not to be sold or copied to any other concern.

TITLE	ALUMINUM HIGH SPEED DOOR STRUCTURE DWG			NIHVA TECHNOLOGIES PVT. LTD.
	NAME	SIGN	DATE	
DRAWN	S.M.S.		07.10.2020	CLIENT - AMULYA TRADERS
CHECK	P.V.A.		07.10.2020	PROJECT - JOHN DEERE
APPRD.				SITE LOCATION - PUNE
If any queries contact : projectsupport@nihva.com				DWG. NO. : NIHVA/20-21/0060 / REV- 0
ALL DIMENSION ARE IN mm				SCALE: NTS / WT: / SHEET: 01 OF 01

NIHVA TECHNOLOGIES PVT. LTD. PUNE
Tel : 020 66304033
Email:- info@nihva.com
Website:- www.nihva.com

NOTE -
(1) ALL REQUIRED TECHNICAL MS STRUCTURE & FITTING IN CLIENT SCOPE .
(2) ALL CIVIL WORK IN CLIENT SCOPE .