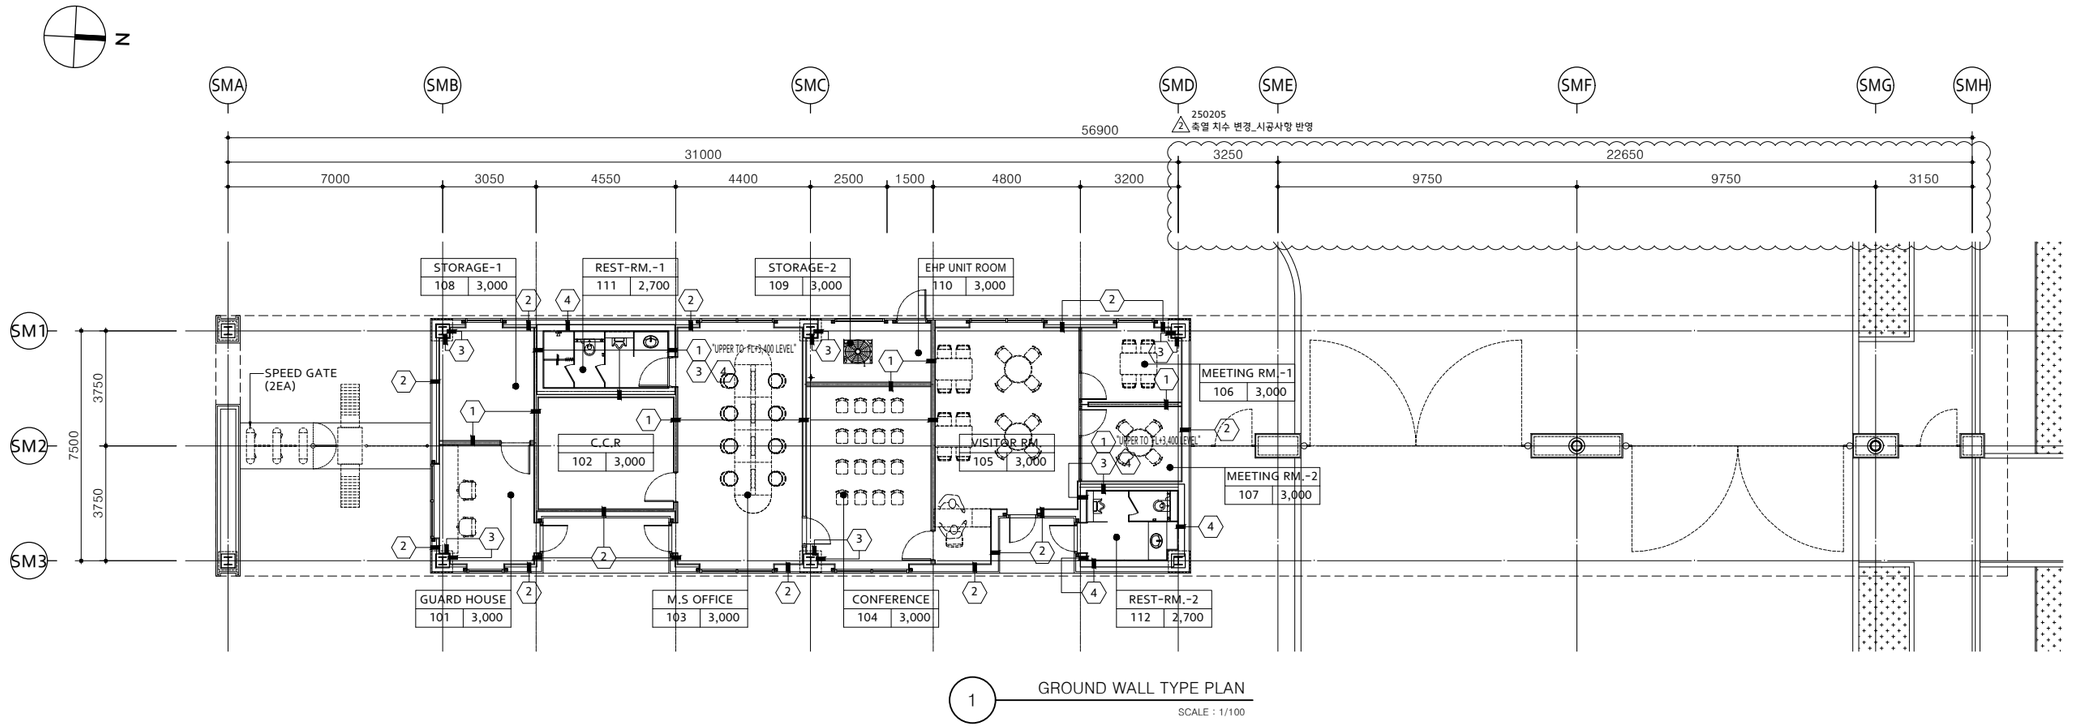


1 GROUND WALL TYPE PLAN

SCALE : 1/100

KEY PLAN


NOTE

WALL TYPE SCHEDULE


WALL NO.	TYPE	STUD SPEC. SHAPE	STUD SPEC. SIZE	STUD SPEC. L	RUNNER	GYP. BD TYPE	HEIGHT (MAX.)	WALL THICKNESS (T)	INSULATION	REMARK
1	GA	C	100*45*0.8	300	102*40*0.8	G	5.60	150		GYP. BD. TYPE -G: GENERAL GYP. BD THK. 12.5 2PLY
2	GB	C	100*45*0.8	300	102*40*0.8	G	5.60	125		
3	GB	C	50*45*0.8	300	52*40*0.8	G	3.63	75		
4	BB	-	-	-	-	-	-	220		

WALL TYPE DETAIL


TYPE-GA

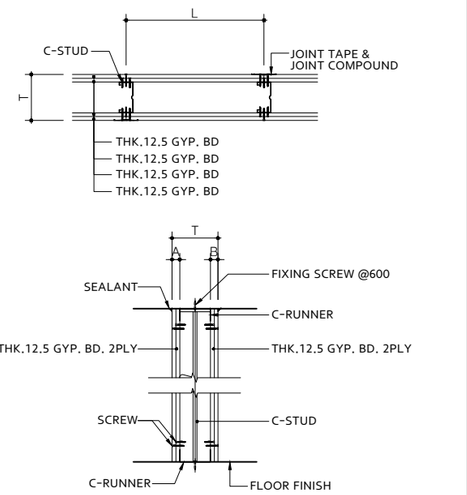


TYPE-GB

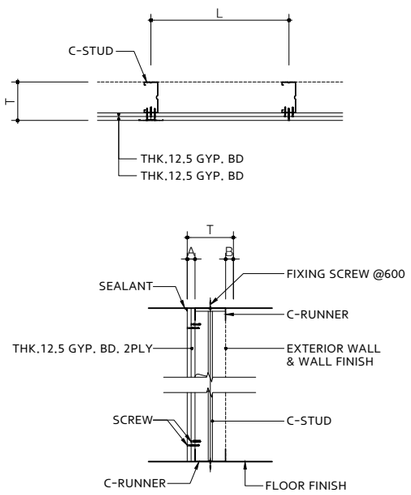

TYPE-BA

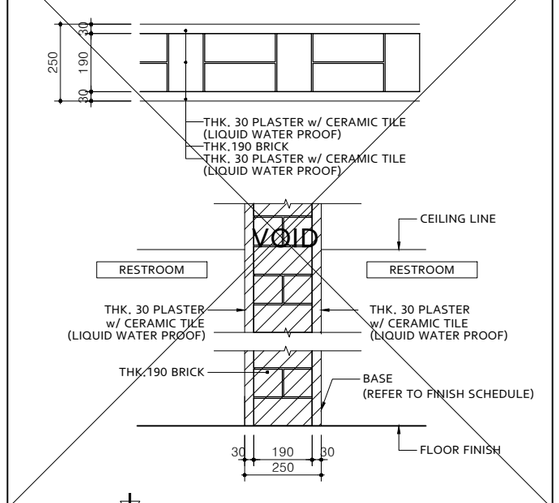

TYPE-BB

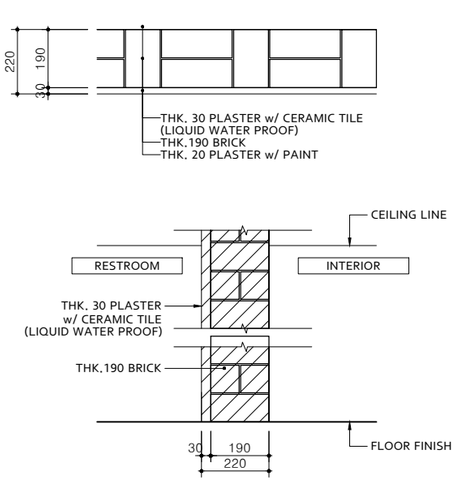

REV.	DESCRIPTION	DRAWN	DATE
2	CD Rev.2	OH.J.S	2025.02.14
1	CD Rev.1	OH.J.S	2024.10.18
0	CONSTRUCTION DRAWING	OH.J.S	2024.07.30
A	DESIGN DEVELOPMENT	OH.J.S	2024.06.28

CLIENT: HYUNDAI

ARCHITECTS & ENGINEERS: JUNGLIM ARCHITECTURE

PROJECT TITLE: PUNE HMI PROJECT

DRAWING TITLE: [MAIN SECURITY OFFICE] WALL TYPE PLAN & DETAIL

SCALE	DRAWN	CHECKED	REVIEWED	APPROVED	APPROVED
A1:1/100 A3:1/200	OH.J.S	HONG.G.D	LEE.S.L	HEC INDIA	PARK.T.S
DATE: 14 FEB.2025					

MAIN CONTRACTOR: HEC INDIA LLP

DRAWING NO.: WA-IPB-645-A-5401

REV.: 2

A1 SIZE (841mm x 594mm)