



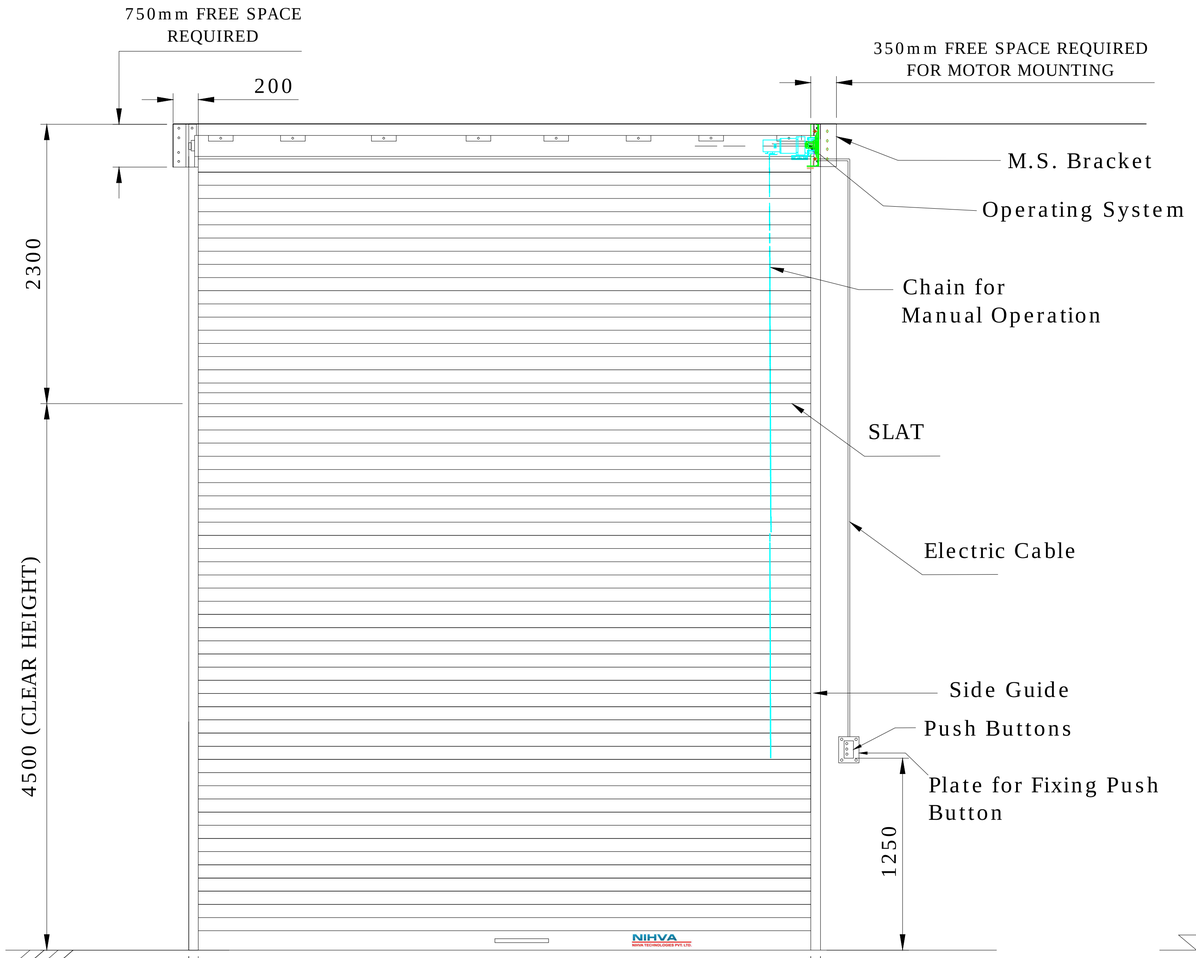


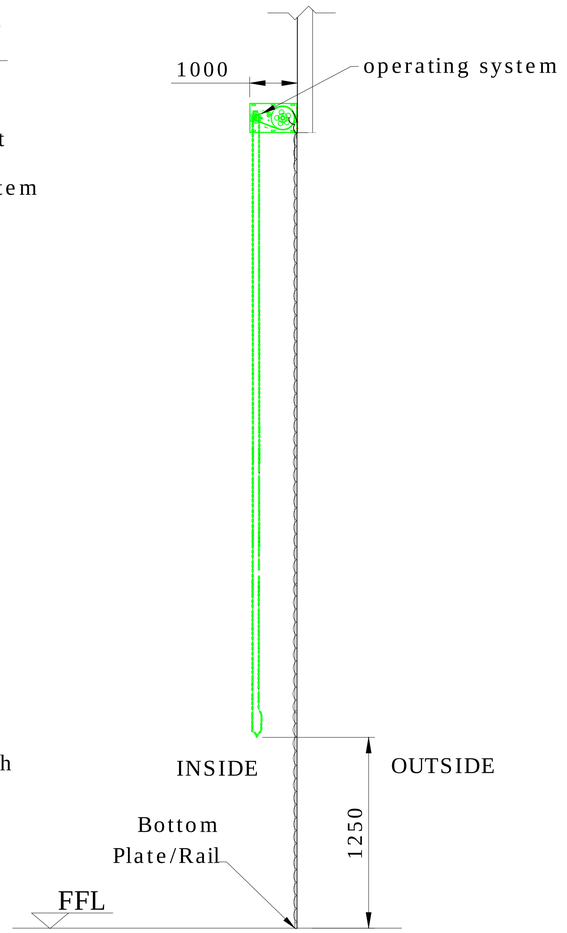

Section A-A

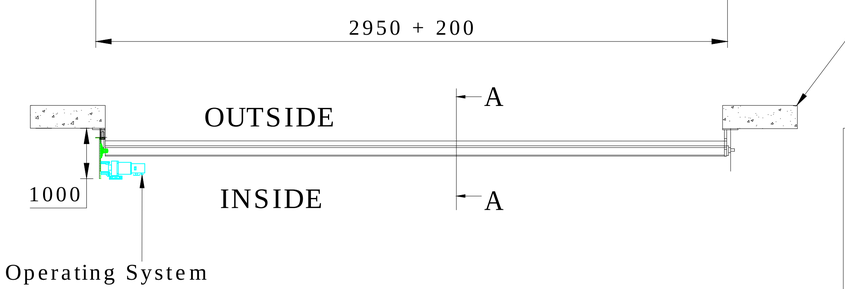

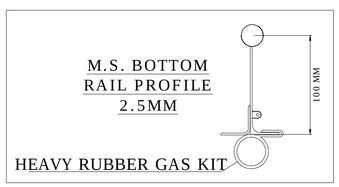

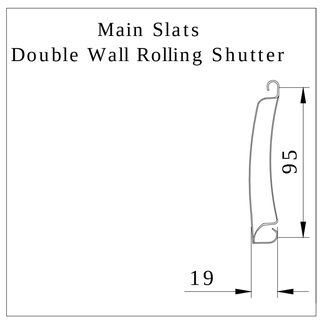

NOTE: COLOUR OF THE SHUTTER WILL BE OFF WHITE
REVISION 1- SHUTTER WILL BE INSTALLED FROM INSIDE
REVISION 2- SHUTTER AND STRUCHURE CHANGES IN HEIGHT AND WIDTH

CLEAR WIDTH(CW)	CLEAR HEIGHT(CH)	QUANTITY	LOCATION
2950mm	4500mm	1 NOS	START FROM NORTH SIDE ROLLING SHUTTER 01

DIMENSION :

CLEAR WIDTH	CLEAR HEIGHT	QUANTITY
2950mm	4500mm	1 NOS

MATERIAL :

THICKNESS :

NOTE-
01.REQUIERD STRUCTURE FOR ROLLING SHUTTER WILL BE IN CLIENT'S SCOPE.
02.NEED STRUCTURAL/RCC SUPPORT BRACKET AND GUIDE MOUNTING.
03.SINGLE PHASE SUPPLY IS REQUIRED.
04.NEED TO CONSTRUCT 70mm WALL IN NORTH SIDE.
05.LHS MOTOR

NIHVA TECHNOLOGIES PVT. LTD.
NIHVA TECHNOLOGIES PVT. LTD. PUNE
Email:- info@nihva.com
Website:- www.nihva.com

TITLE:

DOUBLE WALL ROLLING SHUTTER

CLIENT'S APPROVAL :

CLIENT - LUPIN

PROJECT - LUPIN

SITE LOCATION -NAGPUR.

DWG. NO. : NIHVA/17-18/0030/R02

SCALE: NTS	WT:	SHEET:1 OF 1

DRAWN BY: SURAJ	DATE: 27-05-2017
CHECK BY: SAGAR	DATE: 27-05-2017
APPROVED BY : S.S	DATE: 27-05-2017

If any queries contact : projects@nihva.com

NOTE: ALL DIMENSIONS ARE IN mm

THIS DRAWING & DESIGNING IS THE PROPERTY OF NIHVA TECHNOLOGIES. NOT TO BE SOLD OR COPIED TO ANY OTHER CONCERN.