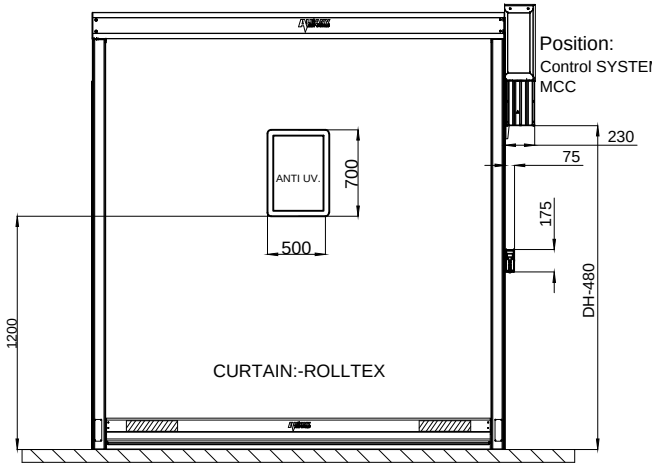
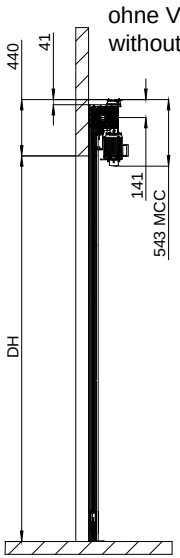
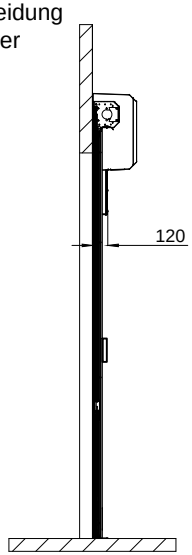
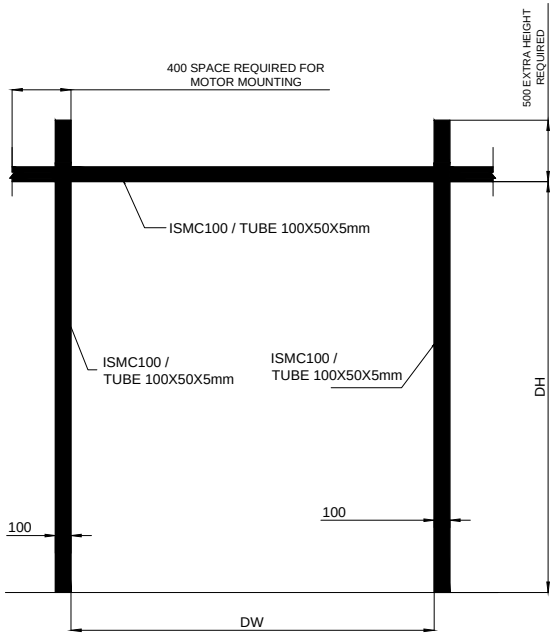
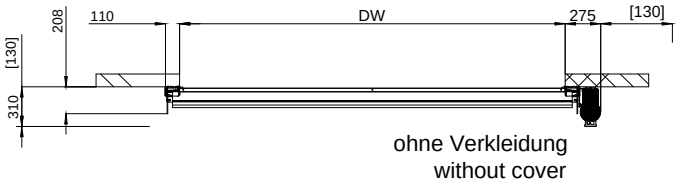
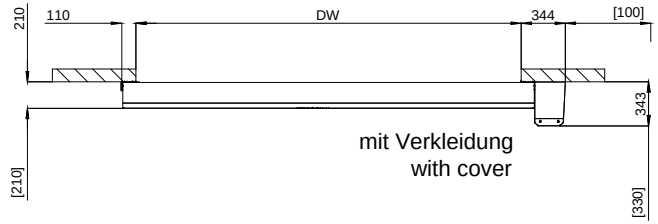



NOTE : ALL CIVIL & STRUCTURAL WORK WILL BE IN CLIENT SCOPE.

RAL : 5002 BLUE

| CLEAR WIDTH(DW) | CLEAR HEIGHT(DH) | QTY |
|---|---|---|
| 2000mm | 2500mm | 02 NOS |
| 4000mm | 2500mm | 03 NOS |

Tolerance ±3 mm (for all dimensions)

Dimensions in [ ] ==> clearance for installation

This drawing & design is the property of NIHVA TECHNOLOGIES. Not to be sold or copied to any other concern.

TITLE: HIGH SPEED DOOR RP300 & STRUCTURE

| | NAME | SIGN | DATE |
|---|---|---|---|
| DRAWN | P.V.A | | 04.07.19 |
| CHECK | V.M.T | | 04.07.19 |
| APPV'ED | | | |

If any queries contact : design@nihva.com

ALL DIMENSION ARE IN mm

NIHVA TECHNOLOGIES PVT. LTD.
NIHVA TECHNOLOGIES PVT. LTD. PUNE
Tel : 020 66304033
Email:- info@nihva.com
Website:- www.nihva.com

CLIENT :- ABB ROBOTICS

PROJECT :-

LOCATION :- BANGALORE.

DWG. NO. :- NIHVA/19-20/0046 REV.:-00

SCALE: NTS WT: SHEET: 01 OF 01