




SIDE VIEW

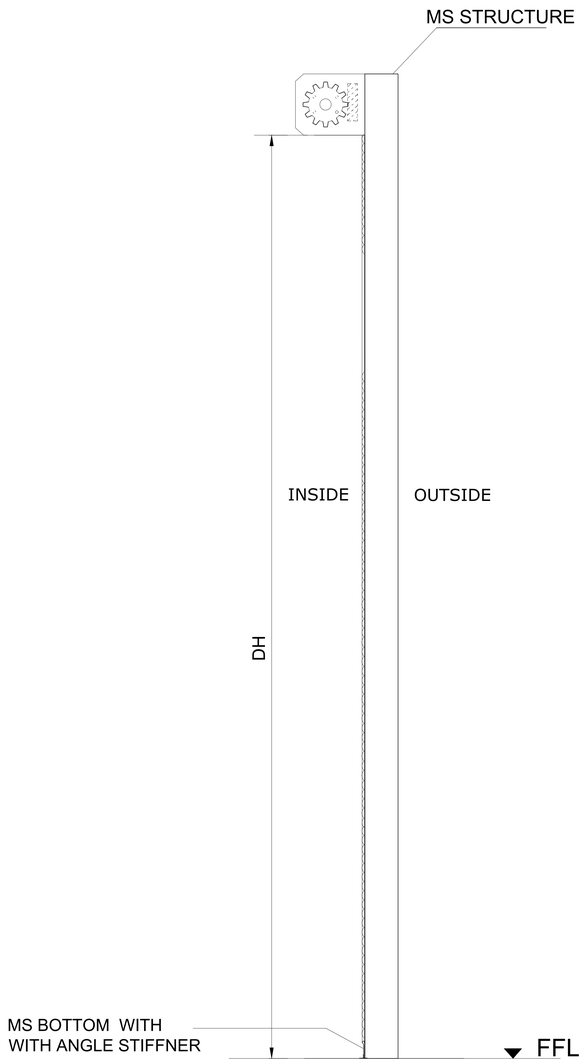

OUTSIDE ELEVATION

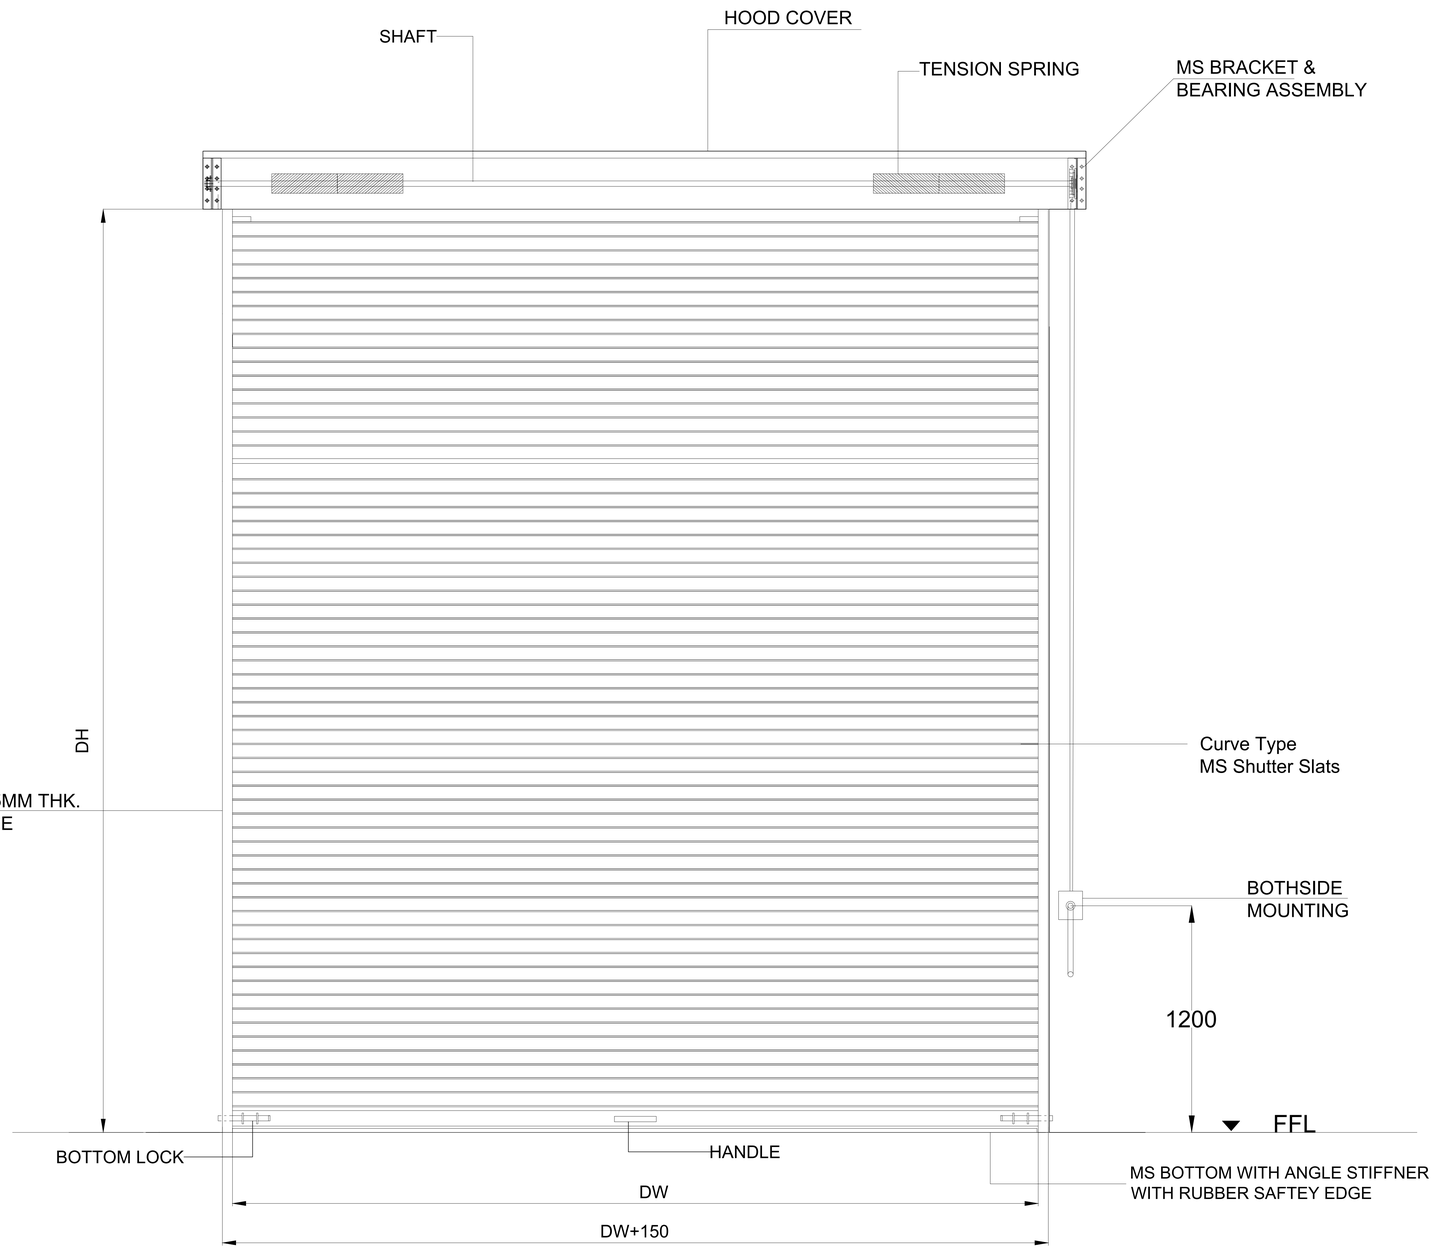

PLAN

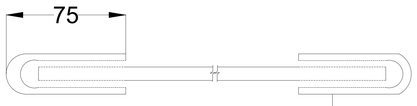

NOTE:-

1. ALL DIMENSION ARE IN MM
2. ALL CIVIL WORK WILL BE IN S.P.F.S SCOPE.
3. MOUNTING: MS STRUCTURE MOUNTING WILL BE IN S.P.F.S SCOPE
4. SURFACE FINISH: POWDER COATING OF APPROVED RAL CODE -RAL 9001
5. SLATS QTY FOR SINGLE SHUTTER WILL BE 65NOS
6. SLAT GALVANIZATION SHALL BE MIN.230g/sqm
7. ROLLING SHUTTER SHALL BE WITHSTAND A BASIC WIND SPEED OF 50M/S

REV.NO	REVISION	DATE	REVISED BY

CLEAR WIDTH (DW)	CLEAR HEIGHT (DH)	QTY
4000	5500	1nos

This drawing & designing is the property of NIHVA TECHNOLOGIES. Not to be sold or copied to any other concern.

TITLE :-
GEAR OPERATED ROLLING SHUTTER

NIHVA TECHNOLOGIES PVT. LTD. PUNE
Tel : 020 66304033
Email:- info@nihva.com
Website:- www.nihva.com

	NAME	DATE
DRAWN	SUMIT.J	07/11/2023
CHECK		
APPROVAL		

CLIENT - SHREE PER FAB STEELS PVT LTD
PROJECT -ROLLING SHUTTER
FORMAT NO - NIHVA - DD -F-03
PROJ. NO. : NIHVA/NTPL/191 REV-01
If any queries contact : design@nihva.com
SCALE: NTS WT: SHEET: 01 OF 01
ALL DIMENSION ARE IN mm