

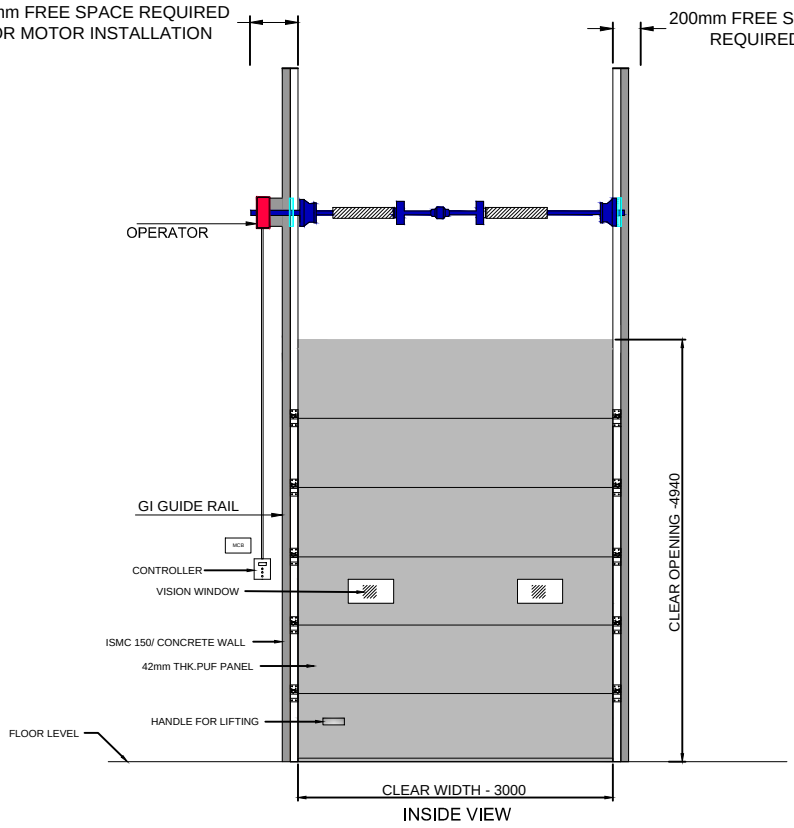


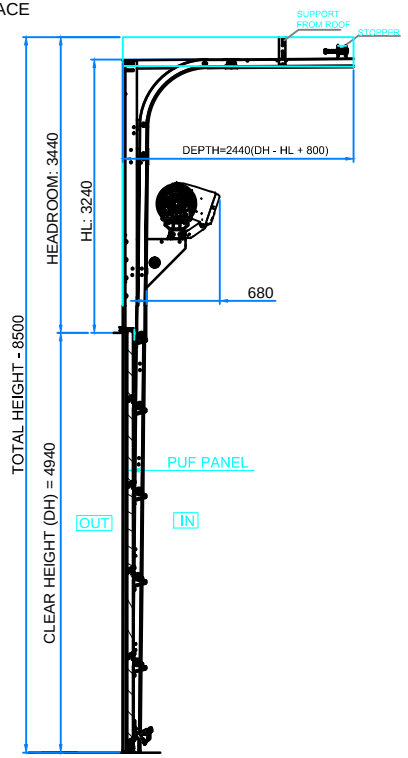

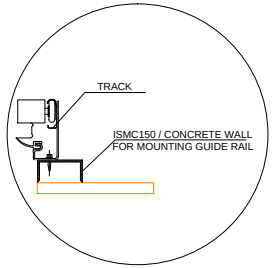

GUIDE DETAIL

SR NO	CLEAR WIDTH	CLEAR HEIGHT	QTY	TH
01	3000mm	4940mm	1	8500

TOLERANCE: ±10mm

This drawing & design is the property of NIHVA TECHNOLOGIES. Not to be sold or copied to any other concern.

TITLE				
SECTIONAL DOOR (HL)				NIHVA TECHNOLOGIES PVT. LTD. PUNE
				Tel : 020 66304033
	NAME	SIGN	DATE	Website:- www.nihva.com Email:- info@nihva.com
DRAWN	P.V.A		16.08.19	CLIENT - RELIABLE CONSTROTECH
CHECK	V.C.J		16.08.19	PROJECT - TATA CUMMINS
APPROVAL				SITE LOCATION- PHALTAN
If any queries contact : design@nihva.com				DWG. NO. : NIHVA/19-20/0078 REV: 00
ALL DIMENSION ARE IN mm				SCALE: NTS WT: SHEET: 01 OF 01