




SIDE VIEW

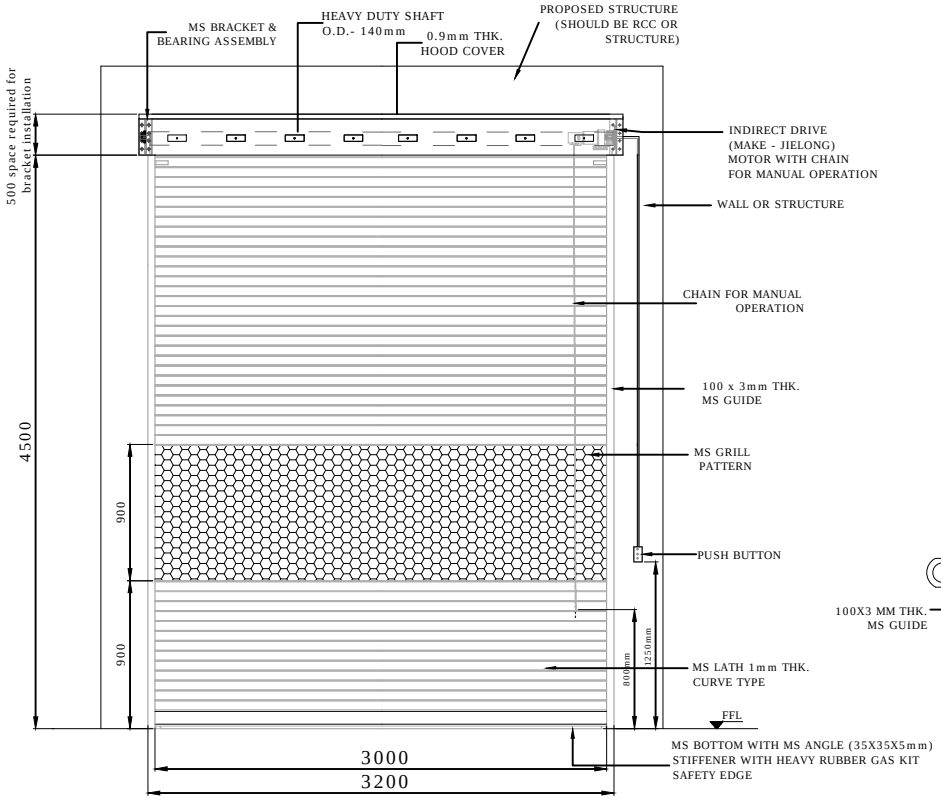


ELEVATION

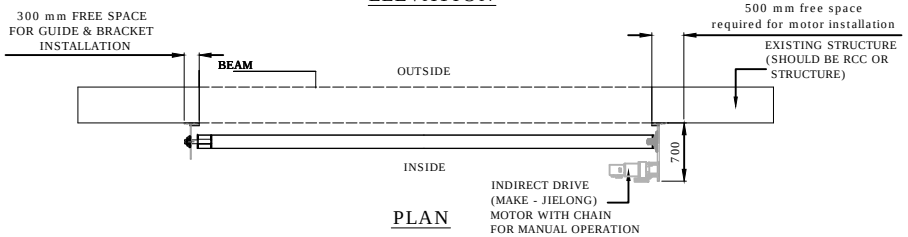


PLAN

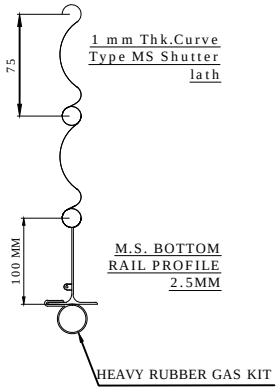

M.S. BOTTOM RAIL PROFILE 2.5MM

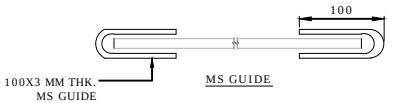

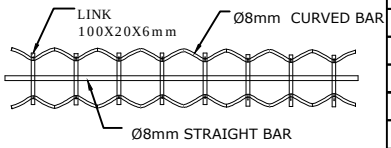

M.S. GRILL PATTERN

R02 - ADD DETAILS IN DRAWING.
R01 - GRILL SIZE CHANGED.

SHUTTER TYPE	CLEAR WIDTH (CW)	CLEAR HEIGHT (CH)	GUIDE SIZE	BRACKET SIZE	SHAFT SIZE (O.D)	QUANTITY	LOCATION
RS2	3000	4500	100X3mm	450X450X5mm	140mm	2	G.F. UTILITY BUILDINGS

SHUTTER SPEED- APPROX. 0.05m/s

DIMENSION :

CLEAR WIDTH	CLEAR HEIGHT	QUANTITY
3000	4500	02 NOS

MATERIAL:

THICKNESS :

NOTE:
1.REQUIRED STRUCTURE FOR ROLLING SHUTTER WILL BE CLIENT'S SCOPE.
2.SINGLE PHASE. 3 CORE 1.5 SQ. CABLE REQUIRE AT SITE(CLIENT'S SCOPE)
3. SHUTTER WILL BE POWDER COATED CLIENT SHOULD CONFIRM RAL COLOR SHADE.
4.POWER SUPPLY LOCATION WILL BE ACTUAL SITE CONDITION.

REV NO	DATE	DESCRIPTION
REV 0	21-11-17	INITIAL DRAWING
REV 1	29-11-17	MORE DETAILS ADDED TO THE DRAWING.
REV 2	13-12-17	MORE DETAILS ADDED TO THE DRAWING.

NIHVA TECHNOLOGIES PVT. LTD.
NIHVA TECHNOLOGIES
PVT. LTD. PUNE
Email:- info@nihva.com
Website:- www.nihva.com

TITLE:

MOTORIZED ROLLING SHUTTER 3X4.5m

CLIENT'S APPROVAL :

CLIENT - SCON PROJECTS

PROJECT -ENZENE BIOSCIENCES LTD.

SITE LOCATION - CHAKAN.

DWG. NO. : NIHVA/17-18/0284 REV.:-02

SCALE: NTS WT: SHEET:1 OF 1

		DATE	SIGN.
DRAWN	SURAJ	13-12-2017	
CHECK	OMKAR	13-12-2017	
APPRD	SHEKHAR	13-12-2017	

If any queries contact : design@nihva.com

NOTE: ALL DIMENSIONS ARE IN mm

THIS DRAWING & DESIGN IS THE PROPERTY OF NIHVA TECHNOLOGIES. NOT TO BE SOLD OR COPIED TO ANY OTHER CONCERN.