

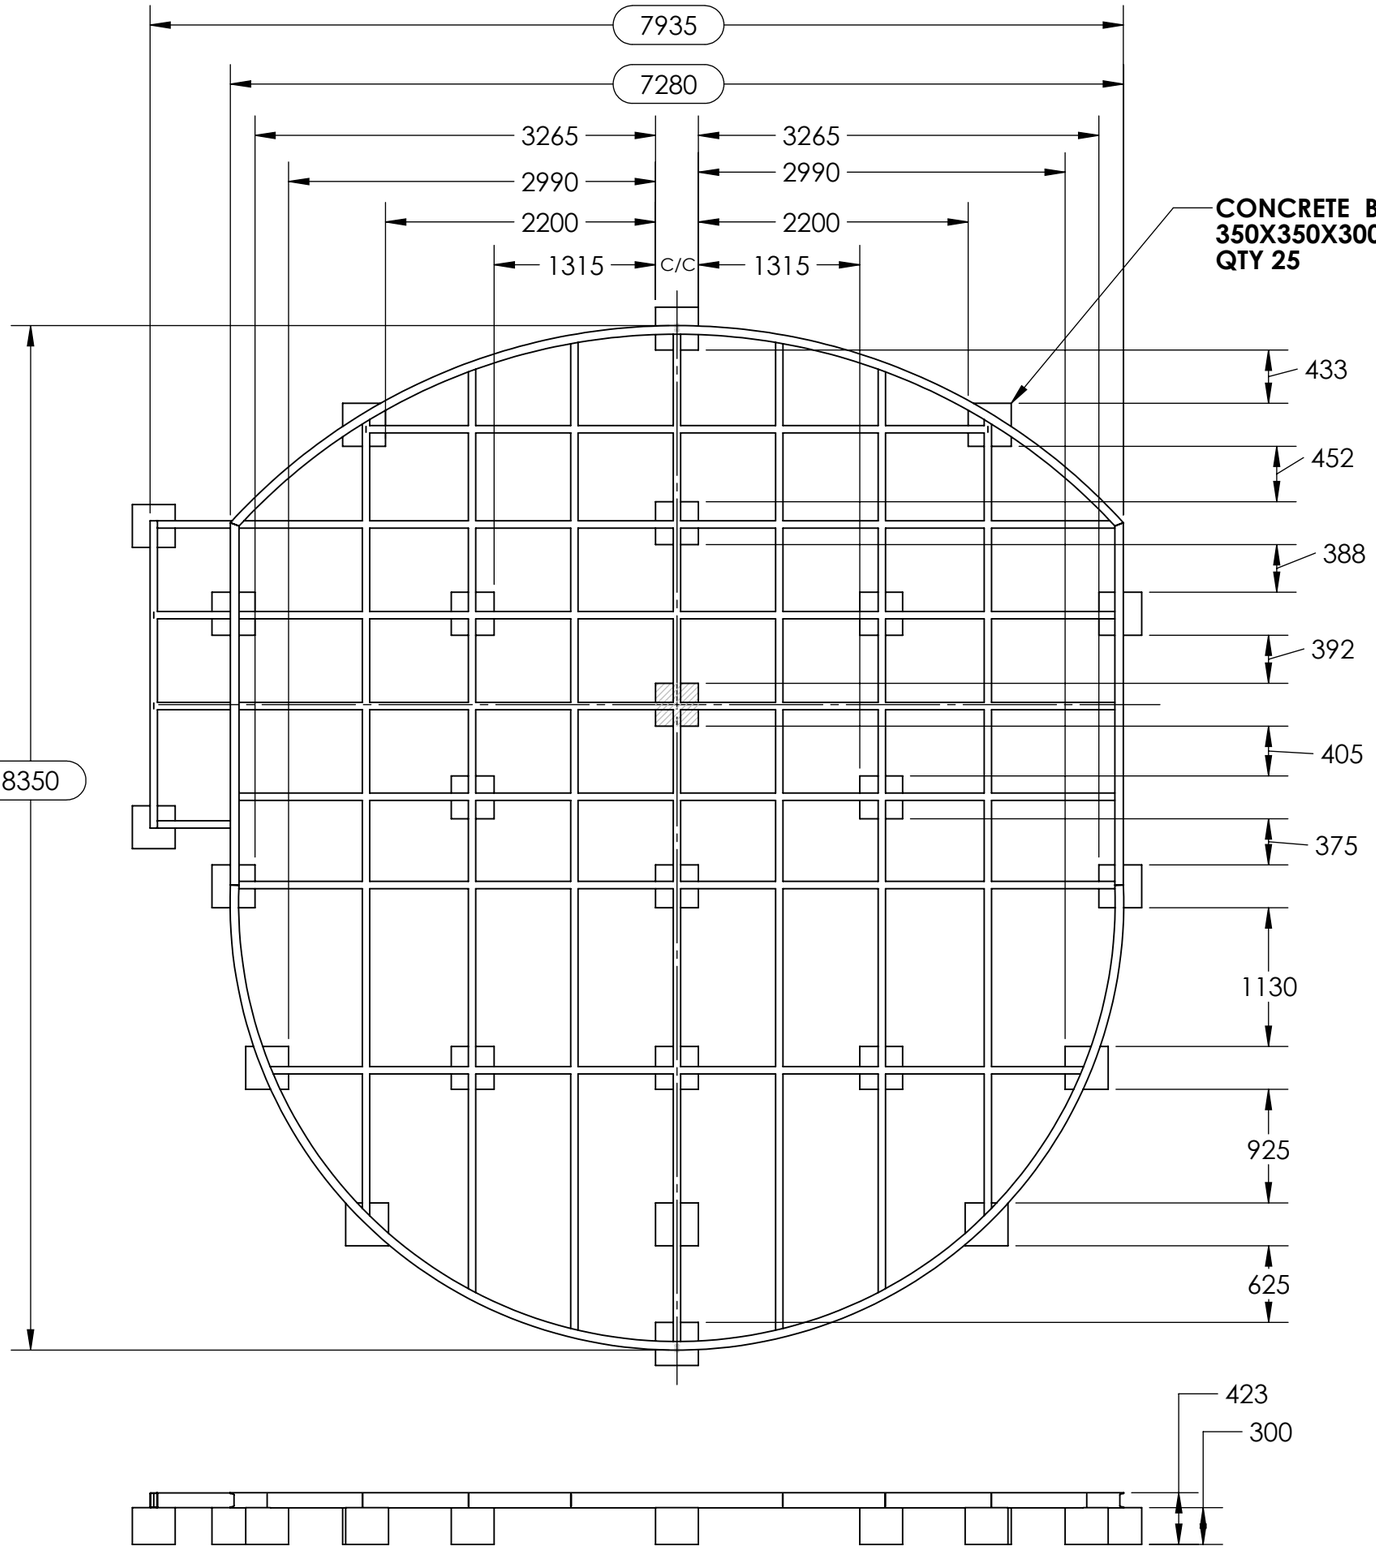


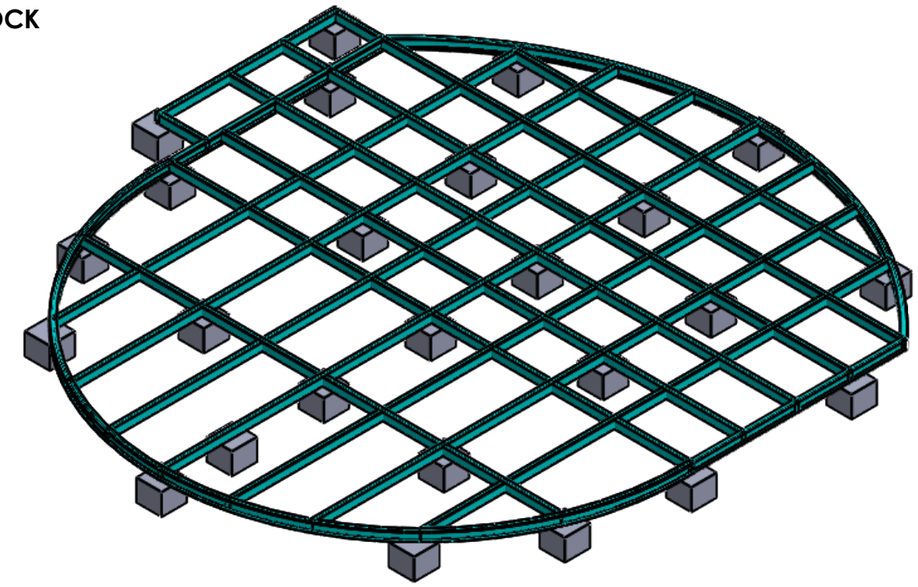

TITLE - BASE FRAME CIVIL SUPPORT				NIHVA TECHNOLOGIES PVT.LTD.PUNE Website - www.nihva.com
	NAME	SIGNATURE	DATE	PROJECT NO -
DRAWN	D.V.		28.11.2023	PRODUCT - DOME
CHK'D	P.M.		28.11.2023	SITE LOCATION -
APPV'D	V.T.		28.11.2023	
if any queries contact - supportautomation@nihva.com				REVISION -
ALL DIMENSION ARE IN mm		A3		SCALE - SHEET 1 OF 2

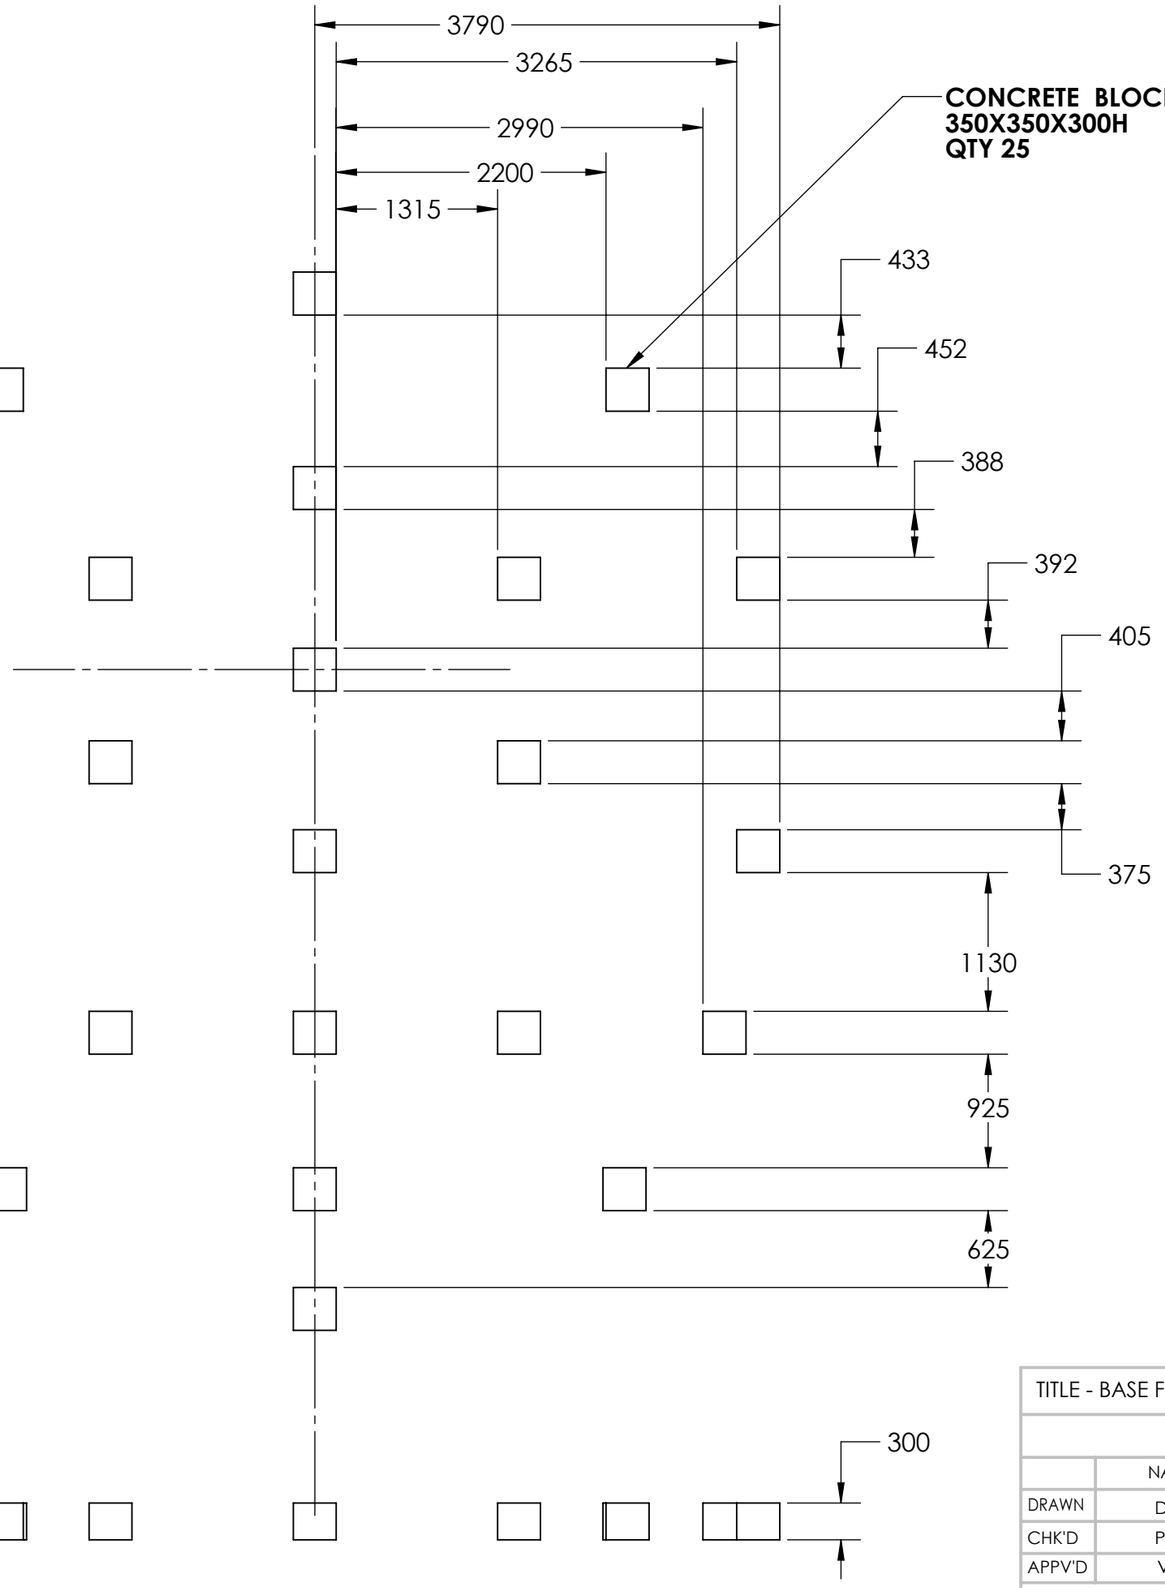

TITLE - BASE FRAME CIVIL SUPPORT				NIHVA TECHNOLOGIES PVT.LTD.PUNE Website - www.nihva.com
	NAME	SIGNATURE	DATE	PROJECT NO -
DRAWN	D.V.		28.11.2023	PRODUCT - DOME
CHK'D	P.M.		28.11.2023	SITE LOCATION -
APPV'D	V.T.		28.11.2023	
if any queries contact - supportautomation@nihva.com				REVISION -
ALL DIMENSION ARE IN mm		A3		SCALE - SHEET 2 OF 2