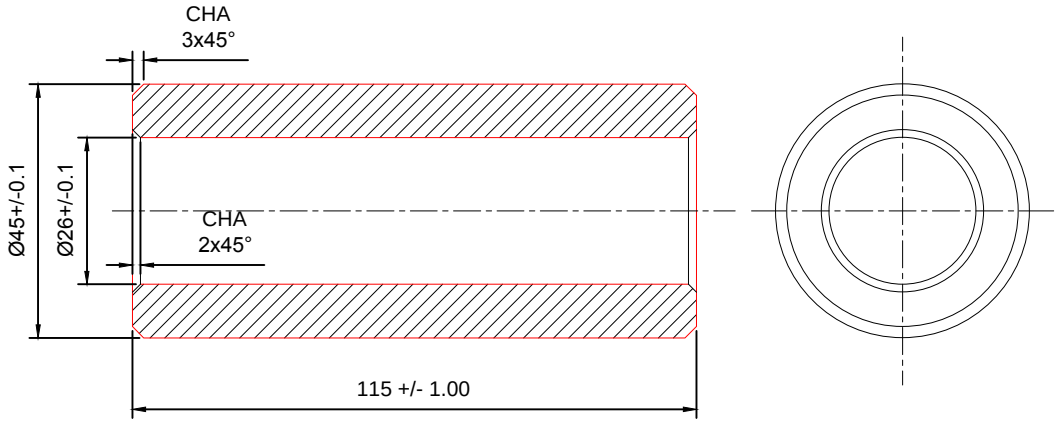


NOTE:~ MTL : MS

BUSH Ø45 X 118L = 18 NOS

NOTE : ~ PLEASE MAINTAIN 7 MM GAP BETWEEN TWO LIP BUSHES.

This drawing & design is the property of NIHVA TECHNOLOGIES. Not to be sold or copied to any other concern.

TITLE

LIP MOUNTING BUSH

NIHVA TECHNOLOGIES PVT. LTD.

NIHVA TECHNOLOGIES PVT. LTD. PUNE
Tel : 020 66304033
Email:- info@nihva.com
Website:- www.nihva.com

	NAME	SIGN	DATE
DRAWN	PRADEEP		02.05.2018
CHECK	PRADEEP		02.05.2018
APPRD.	PRADEEP		02.05.2018

CLIENT -

PROJECT - DLIK1005

SITE LOCATION -

If any queries contact : design@nihva.com

DWG. NO. :NIHVA/18-19/VDR/359

ALL DIMENSION ARE IN mm

SCALE: NTS | WT: | REV- 0