



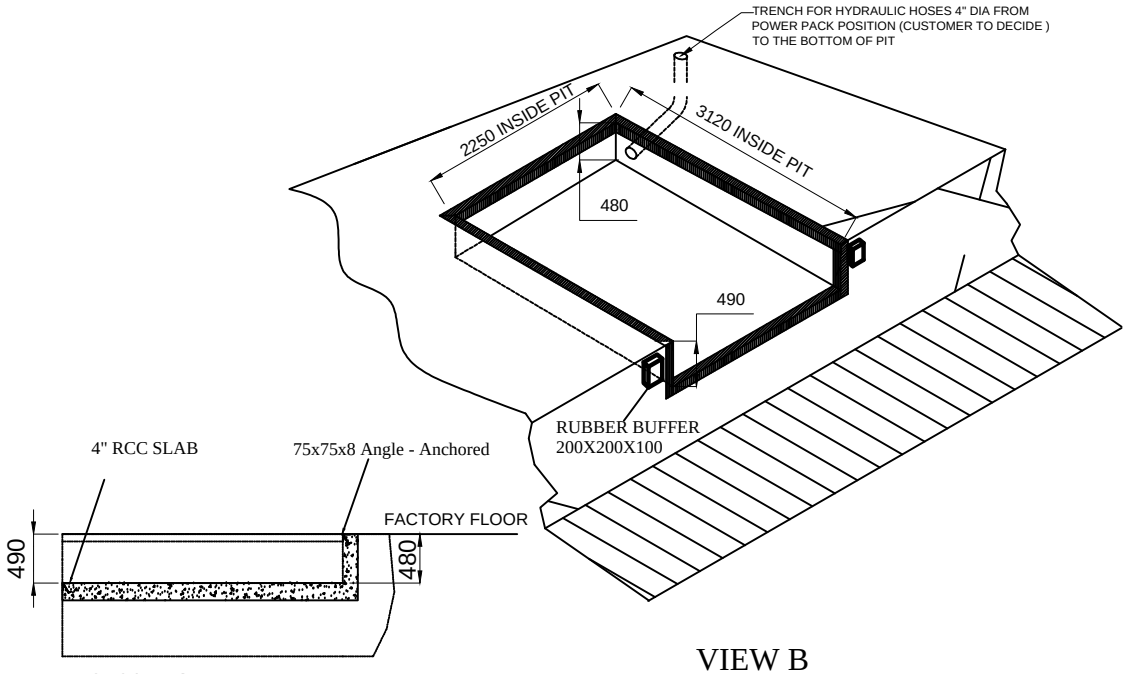


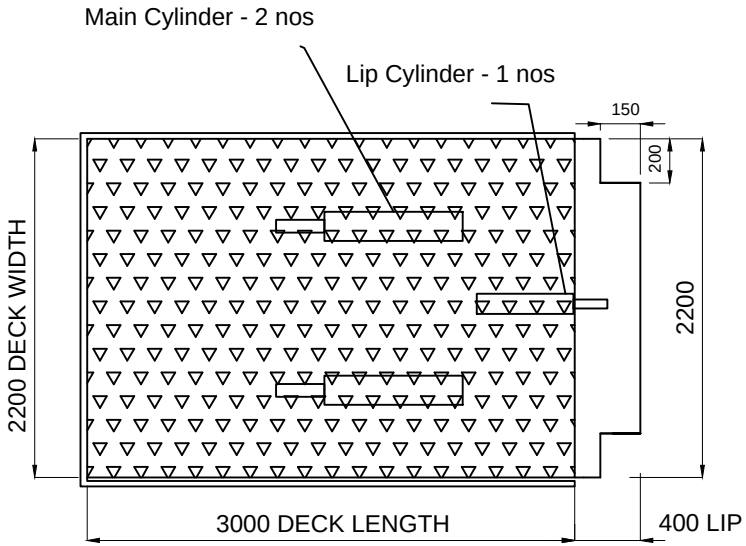

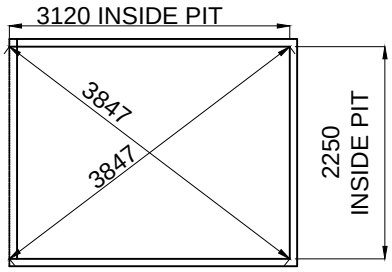

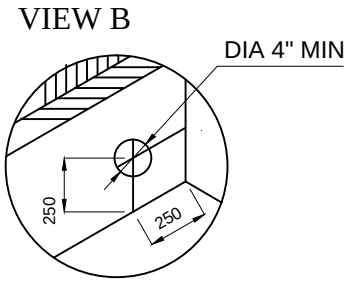

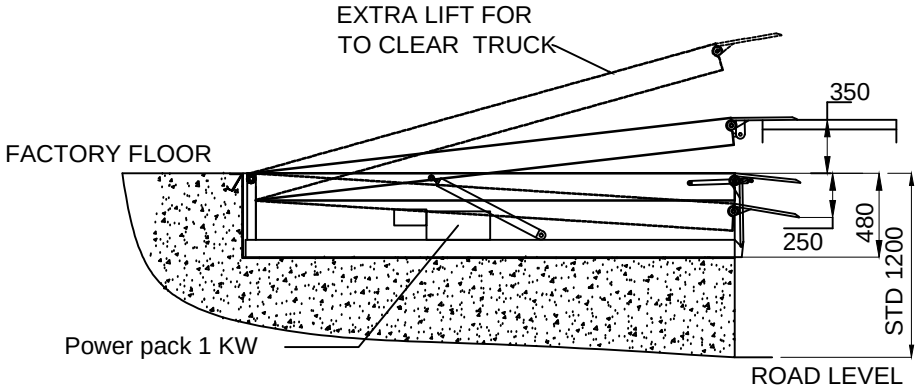

NOTE:

1. PROPER DRAINAGE SHOULD BE DONE
2. TRENCH AS SHOWN SHOULD BE MADE BY DECIDING THE POWER PACK POSITION (SUPPLY HOSE LENGTH STD. 3000 MM)
3. LEVEL OF THE PIT SHOULD BE PLAIN AND SHOULD TAKE AT LEAST 15000 KGB FLOOR LOADING
4. FABRICATION TOLERANCE FOR PLATFORM SIZE WILL BE ± 10 MM .
5. PIT, DUCT FOR HOSES & ALL CIVIL WORK IS IN CLIENT SCOPE .

SPECIFICATIONS OF DOCK LEVELER -

1. PLATFORM SIZE -2200WX3000L
2. LIFT ABOVE- 350 MM
3. LIFT DOWN-250 MM
4. PIT SIZE- 2250WX3120LX480D
5. CAPACITY - 12 TON
6. FINISH - PAINTING GOLDEN YELLOW RAL 1004 (NIHVA STANDARD)
7. QTY - 3 NOS
8. HYDRAULIC POWERPACK - 1kW , 3 PHASE AC , 50 Hz

This drawing & designing is the property of NIHVA TECHNOLOGIES. Not be sold or copy to any other concern.

TITLE			NIHVA TECHNOLOGY PVT. LTD. PUNE
PIT MOUNTED ELECTRO-HYDRAULIC DOCK LEVELER			NIHVA TECHNOLOGIES PVT. LTD. Tel : 020 66304033 Email:- info@nihva.com Website:- www.nihva.com
	SIGN	DATE	
DRAWN	SS	26.7.2021	CLIENT - MAGNA AUTOMOTIVE INDIA PVT LTD
CHECK	VJ		PROJECT -
REV.	AK		SITE -
APPROVAL	VT		DWG. NO. : NIHVA/21-22/047/DL / REV NO - R00
If any queries contact : nihvacare@nihva.com			SCALE: NTS / WT: / SHEET: 01 OF 01
ALL DIMENSION ARE IN mm			