

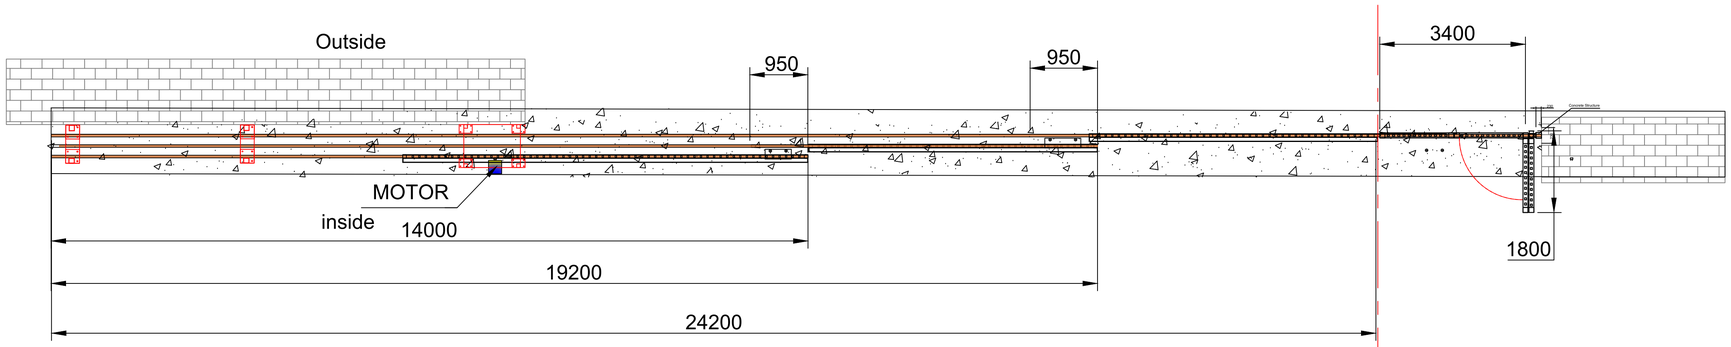


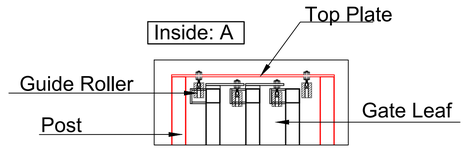


Opening Direction(View from inside)

Opening Direction(View from inside)

Gate Close Position

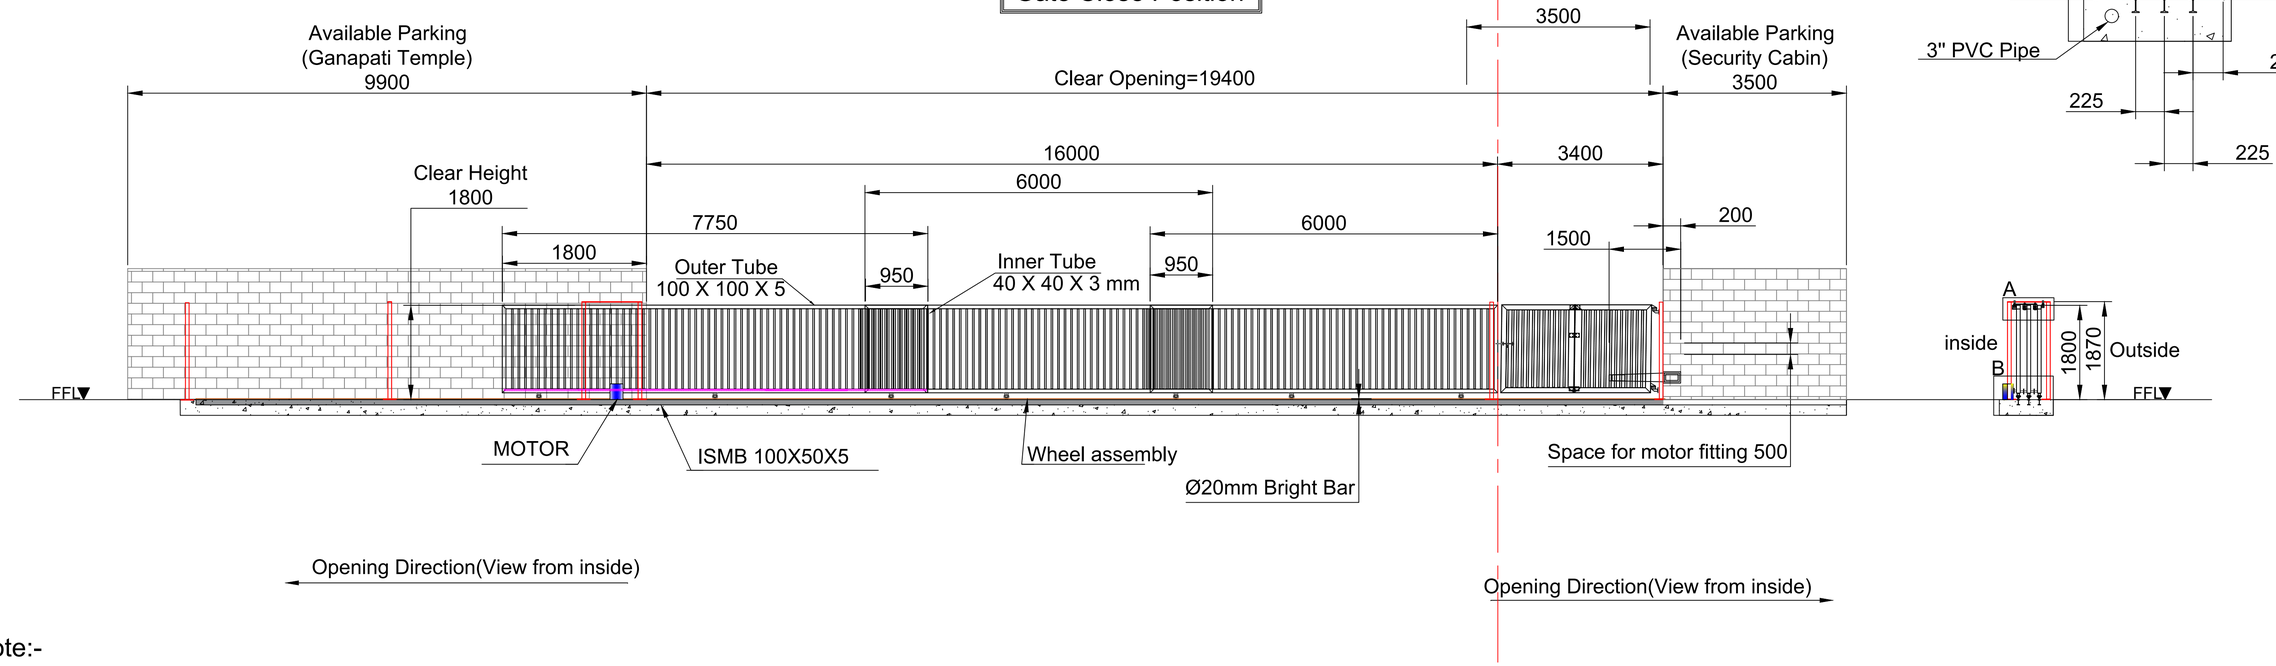

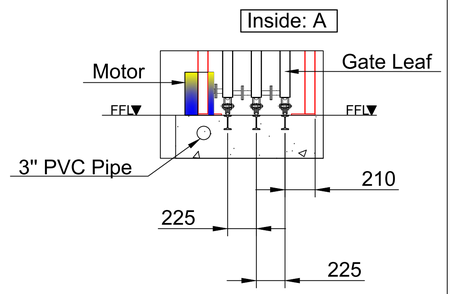

Opening Direction(View from inside)

Opening Direction(View from inside)

Note:-

1.All Dimension are in MM

2.Required All civil work will be in Client scope

3.Installlation and Fabrication tolerance will be ±20mm

4. Required Parking will be 8000 mm

5. Gate Color will be Metalic color,shade stone gray(RAL7030)

Rev No.	Revision	Date	Revised By
01	REVISED WITH FOUNDATION OF FOLDABLE GATE	25/08/2022	MAHESH S.

This drawing & design is the property of NIHVA TECHNOLOGIES. Not to be sold or copied to any other concern.

TITLE:-
Tel.Sliding Gate & Foldable Gate

	NAME	DATE	SIGN
DRAWN	MAHESH.S	09/08/2022	
CHECK	MAHESH.S	09/08/2022	
APPRD.	AMIT.K	09/08/2022	

If any queries contact : design@nihva.com

ALL DIMENSION ARE IN mm

NIHVA
NIHVA TECHNOLOGIES PVT. LTD.

NIHVA TECHNOLOGIES
PVT. LTD. PUNE
Tel : 020 66304033
Email:- info@nihva.com
Website:- www.nihva.com

CLIENT - NAVNEET EDUCATION LTD

LOCATION - PALGHAR

PRODUCT - TEL.SLIDING GATE | QTY-01

DWG NO:- NIHVA/22-23/CLT/0071_6 | REV-01

SCALE: NTS | SCALE:-- 1:1 | SHEET: 01 OF 01