


GOOD FOR CONSTRUCTION
DATE - 06-07-2024

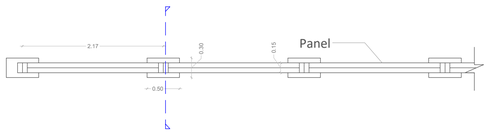


PLAN OF COMPOUND WALL

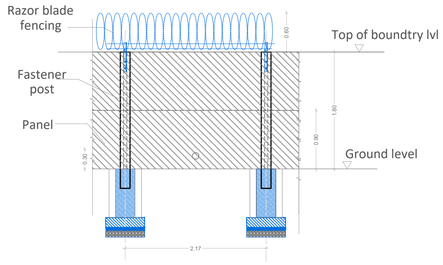


PART ELEVATION OF COMPOUND WALL

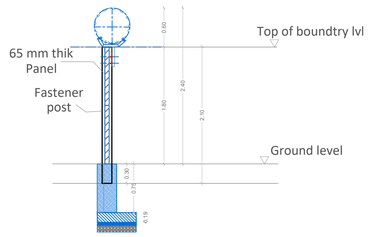


SECTION THROUGH COMPOUND WALL

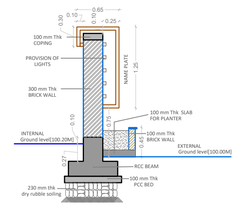


SECTION AA'

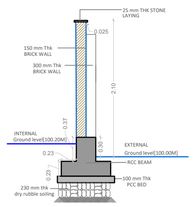

SECTION BB'

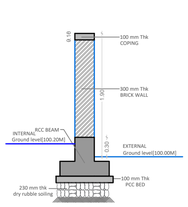

SECTION CC'

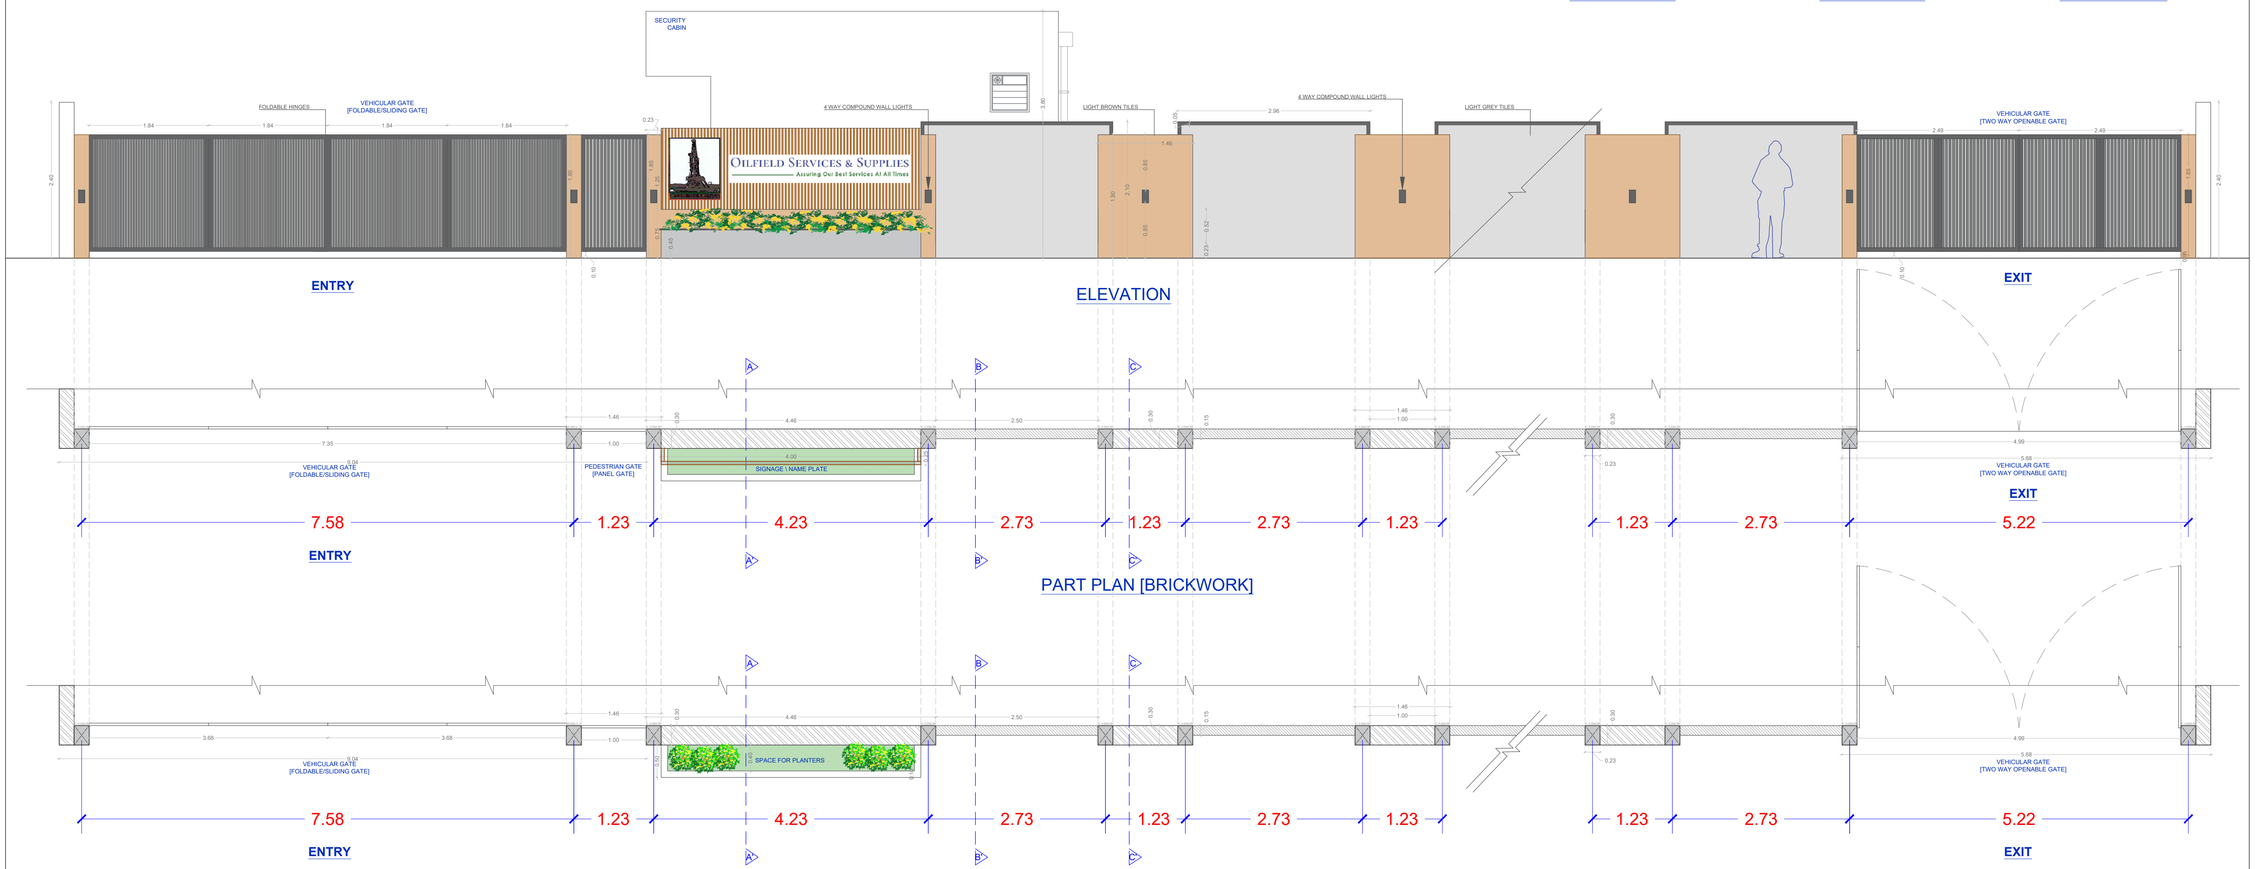

N

COMPOUND WALL DETAILS

SCALE : 1:100

NOTES.

1) ALL DIMENSIONS ARE IN METER.
2) DRAWING NOT TO BE SCALED.
3) ONLY WRITTEN DIMENSIONS TO BE FOLLOWED.
4) FOR COLUMN SIZES REFER RCC DRAWING.
5) ANY AMBIGUITY IN THE DRAWING SHALL BE BROUGHT TO THE NOTICE OF ARCHITECT IMMEDIATELY.
6) FINISHED GROUND LEVEL IS CONSIDERED AS 100.20 LVL & PLINTH LEVEL IS CONSIEDRED AS +100.80 lvl.
7) CONTRACTOR & OWNER TO VERIFY SITE DIMENSIONS BEFORE EXECUTION.
8) TAKE CUBE TEST FOR CASTING OF RCC WORK AND GET CUBE TEST REPORT BEFORE NEXT CASTING CYCLE.

ARCHITECT'S SIGN / SIGNATURE

SPIRO DESIGNS ARCHITECTS & INTERIOR PUNE

AR. SM YADAV
CA/86/9652

FOR M/S. OILFIELD SERVICES AND SUPPLIES PRIVATE LIMITED.
PROPOSED INDUSTRIAL BUILDING ON PLOT No. IZ-08, LODHA INDUSTRIAL & LOGISTIC PARK. PHASE -1, USATANE, & NITLAS

DSG. BY	DRG. BY	CHK. BY	DATE	REVISION
SD	A-PP	SMY	06 JULY 24	R10

TITLE COMPOUND WALL DETAILS

DRG TYPE: **WD - PHASE 1**

DRG NO. 22.

SPIRO DESIGNS,
108, FIRST FLOOR,
MANGALMURTI COMPLEX,
HIRABAG CHAUK,
TILAK ROAD, PUNE - 411002.
PHONE NO. (020) 24474687.