
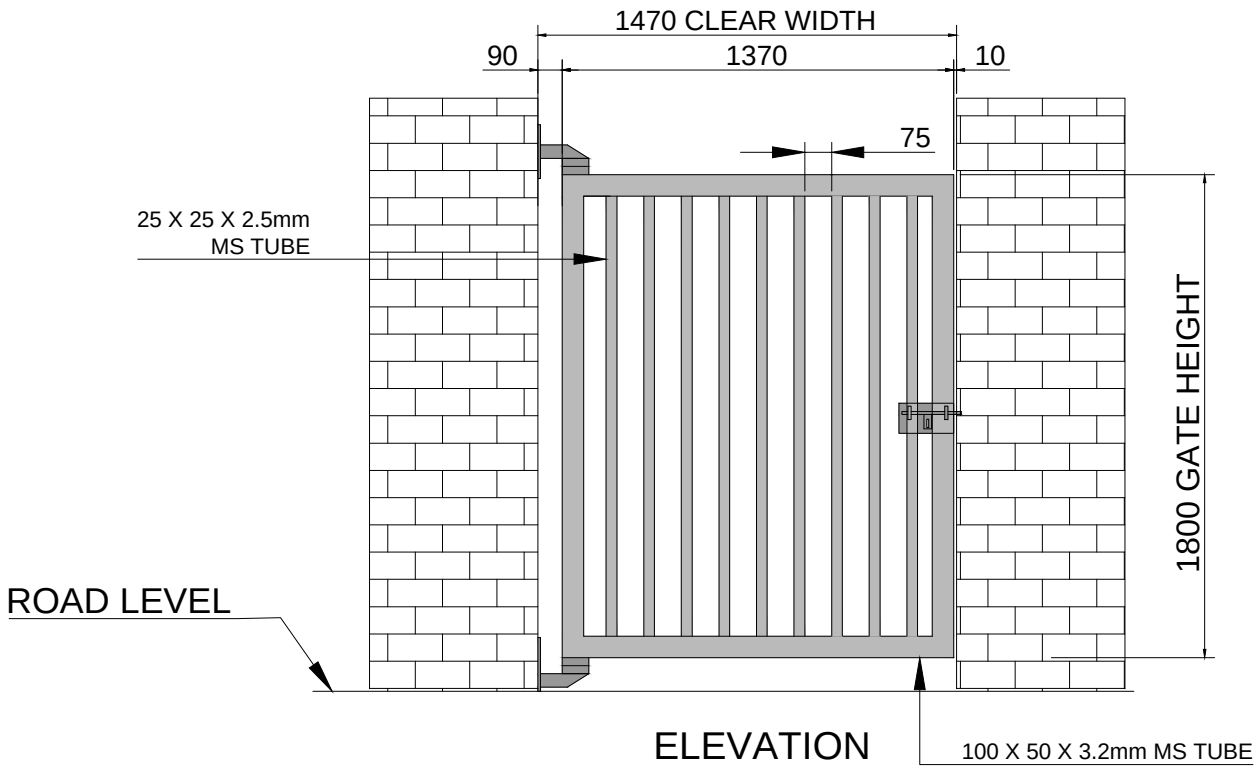


ELEVATION

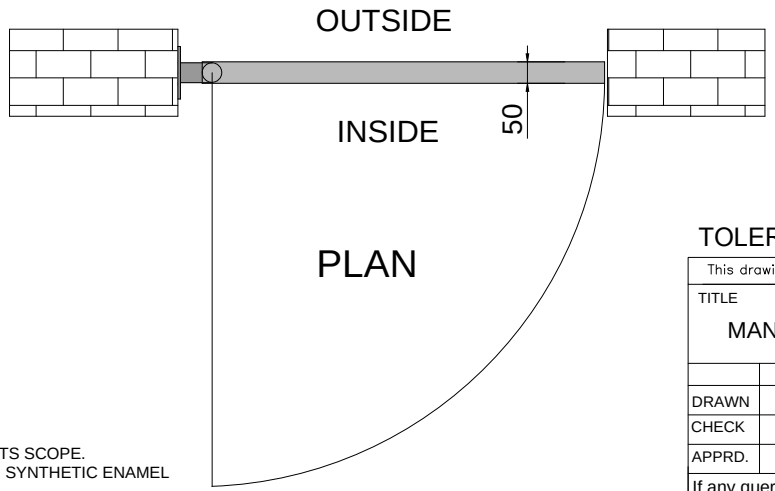

PLAN

QTY : 2 NOS

NOTE-
1. ALL REQUIRED CIVIL WORK WILL BE IN CLIENTS SCOPE.
2. TWO COATS OF PRIMER AND TWO COATS OF SYNTHETIC ENAMEL PAINT OF APPROVE SHADE.

TOLERANCE- ±10mm

This drawing & design is the property of NIHVA TECHNOLOGIES. Not to be sold or copied to any other concern.

TITLE
MANUAL WICKET GATE

	NAME	SIGN	DATE
DRAWN	P.A		23.12.2019
CHECK	G.J		23.12.2019
APPRD.			

NIHVA TECHNOLOGIES PVT. LTD.
NIHVA TECHNOLOGIES PVT. LTD. PUNE
Tel : 020 66304033
Email:- info@nihva.com
Website:- www.nihva.com

CLIENT - DESAI CONSTRUCTIONS
PROJECT -
SITE LOCATION - GUJARAT
If any queries contact : design@nihva.com
DWG. NO. : NIHVA/19-20/0182
REV- R00
ALL DIMENSION ARE IN mm
SCALE: NTS
WT:
SHEET: