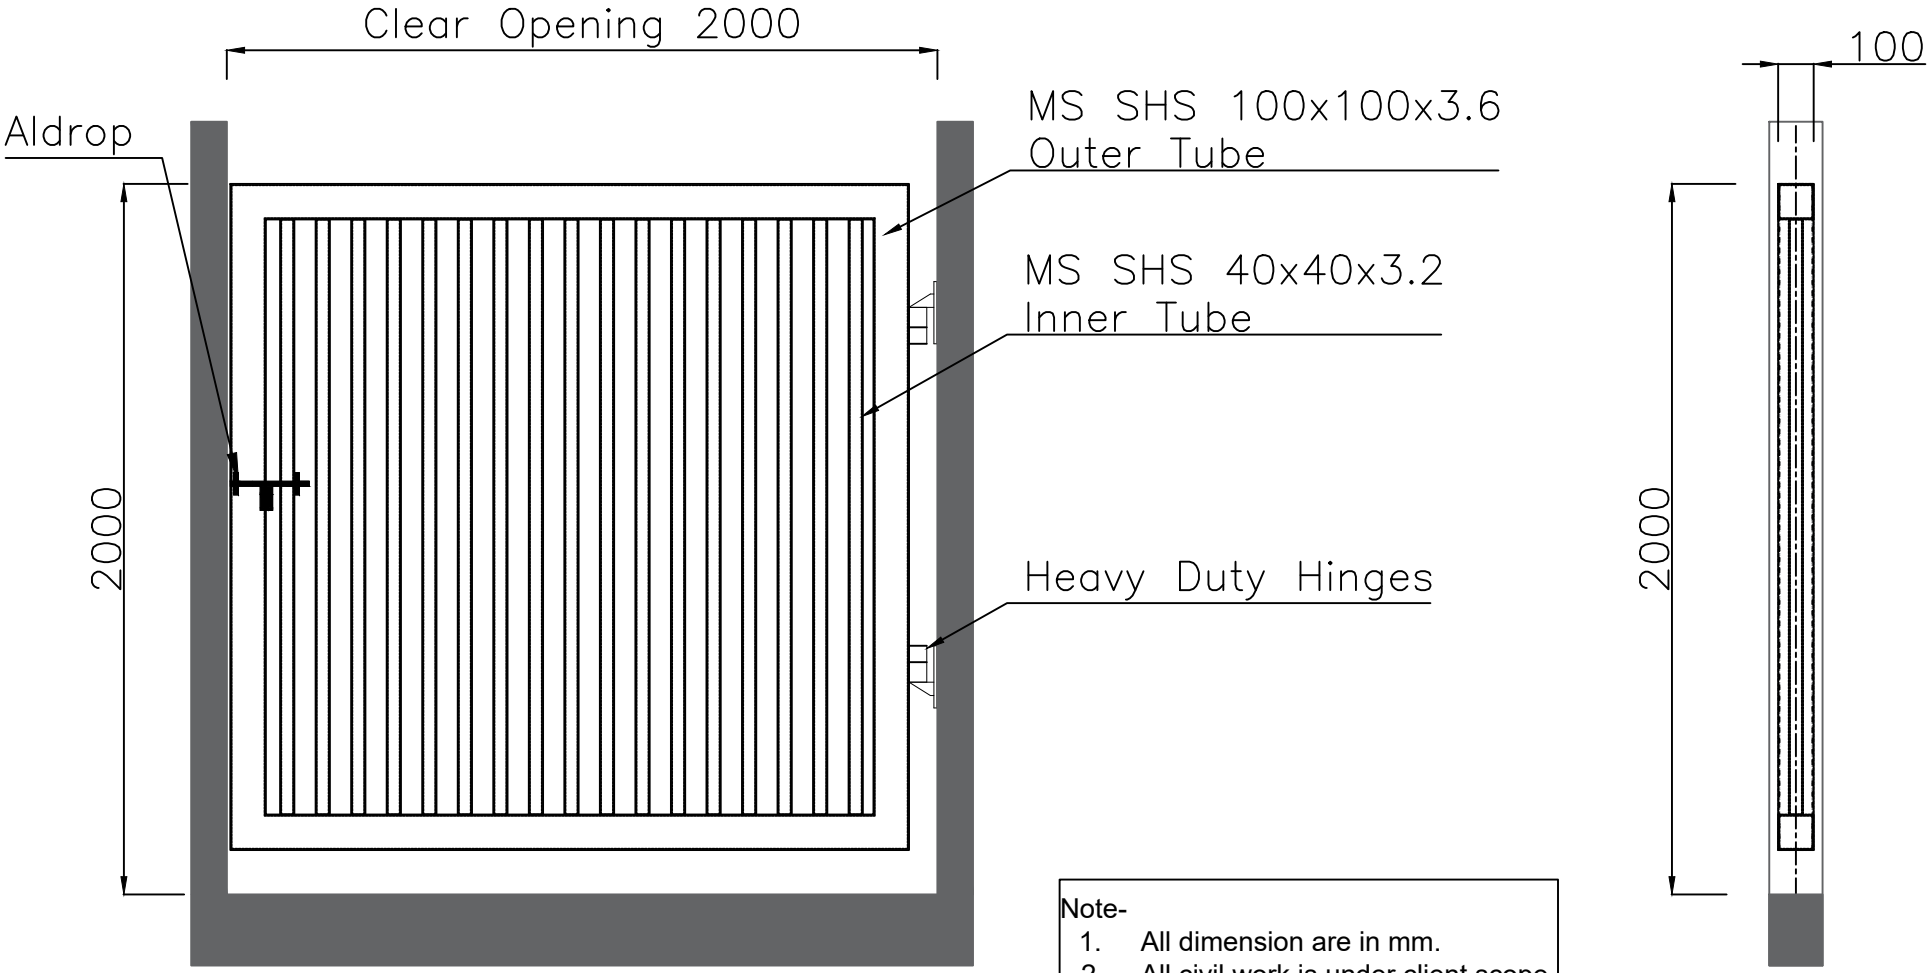


Technical Specs of Swing Gate

1. Opening Width - 2000mm
2. Gate Height - 2000mm
3. Outer tube size - MS SHS 100x100x3.6mm
4. Inner tube size - MS SHS 40x40x3.2mm
5. Pitch between tube - 100mm
6. Total leaf weight ≈ 200 kg
7. Operation - Manual

Note-

1. All dimension are in mm.
2. All civil work is under client scope.

This drawing & design is the property of NIHVA TECHNOLOGIES. Not to be sold or copied to any other concern.

TITLE
SWING GATE

NIHVA
NIHVA TECHNOLOGIES PVT. LTD.

NIHVA TECHNOLOGIES PVT. LTD. PUNE
Tel : 020 66304033
Email:- info@nihva.com
Website:- www.nihva.com

	NAME	SIGN	DATE
DRAWN	G.J.		30.07.21
CHECK	A.K.		30.07.21
APPRD.	V.T.		30.07.21

If any queries contact : projectsautomation@nihva.com

ALL DIMENSION ARE IN mm

CLIENT -M/s FUJI SILVERTECH CONCRETE P. LTD.
LOCATION - AURANGABAD
PRODUCT - SWING GATE 2000x2000
NIHVA\20-21\0198 | REV- 0
SCALE: NTS | SHEET: 01 OF 01