

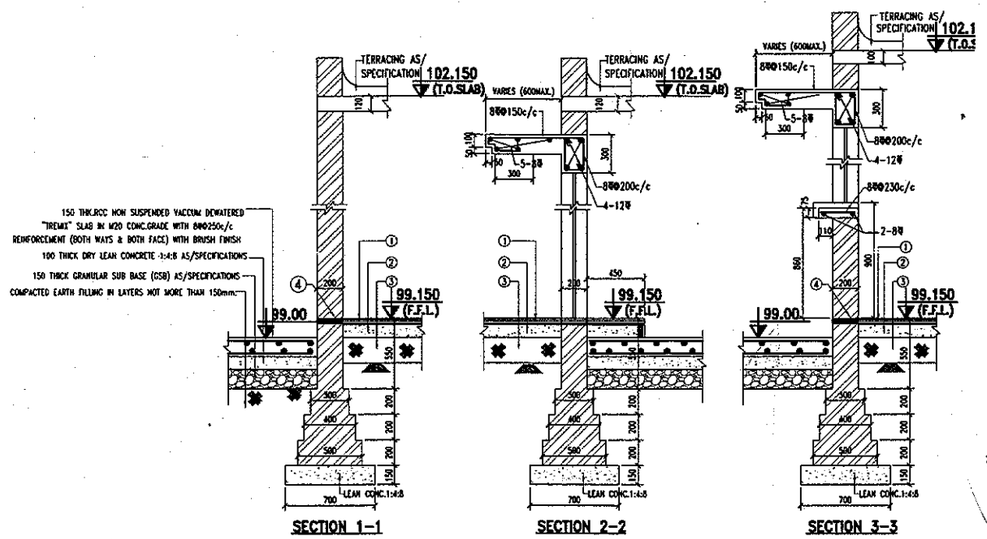


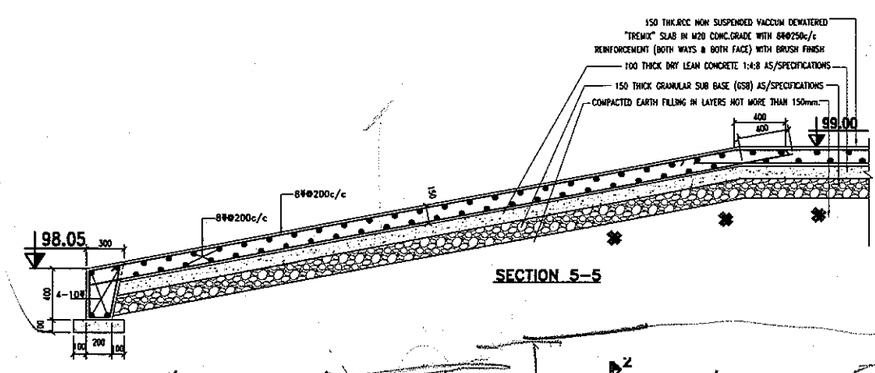

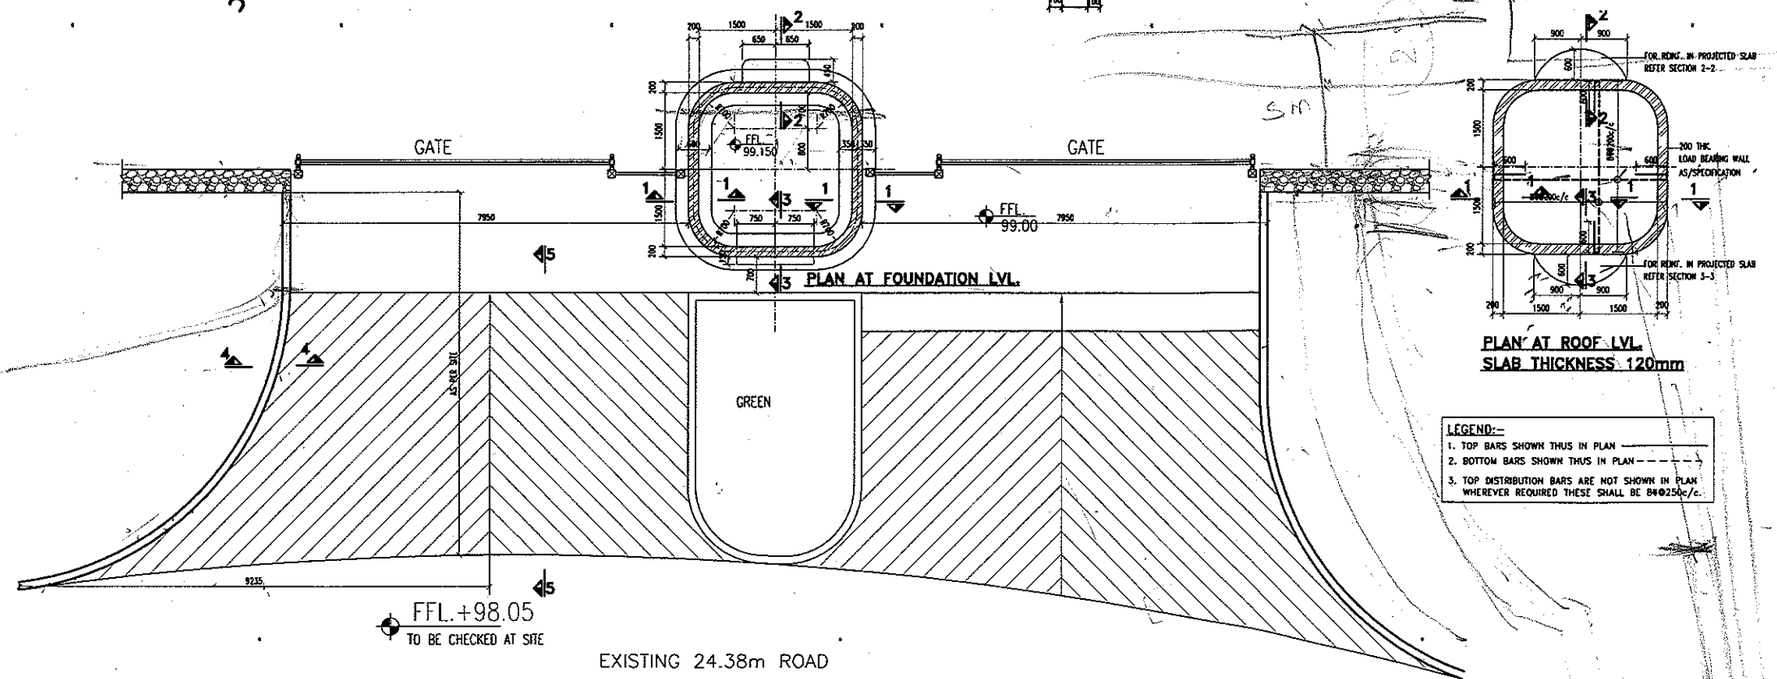

PLAN AT ROOF LVL.
SLAB THICKNESS 120mm

LEGEND:-
1. TOP BARS SHOWN THUS IN PLAN ————
2. BOTTOM BARS SHOWN THUS IN PLAN - - - - - -
3. TOP DISTRIBUTION BARS ARE NOT SHOWN IN PLAN WHEREVER REQUIRED THESE SHALL BE 8#@250c/c.

NORTH POINT

This drawing is a "COPYRIGHT" contents of this drawing or part thereof may not be used or reproduced without the permission of the Architect

NO. OF PRINTS	DATE	ISSUED TO	REMARKS
SOFT COPY	08-08-17	CLIENT	C.F.C

REVISION	DATE	DESCRIPTION	BY

GENERAL NOTES :-

1. All dimensions are in mm unless mentioned otherwise
2. No dimensions are to be scaled from this drawing.
3. Contractors must verify all dimensions on site before commencing any work.

STRUCTURAL NOTES :-

1. Concrete grade will be M 25
2. Cover to outer layer of reinforcement shall be as specified below or dia. of main reinforcement bar whichever is greater (unless specified otherwise)
   a. In footing/raft beam & slab - 50 mm.
   b. In columns - 45 mm.
   c. In beam/slab edges - 30 mm
   d. In beams - 30 mm.
   e. In slabs - 20 mm.
   f. In walls - 40 mm on earth face. 25 mm on inner face.
3. All reinforcement will be Grade Fe 500 conforming to I.S. 1786-1985 or latest unless mentioned otherwise.
4. THIS DRAWING IS TO BE READ IN CONJUNCTION WITH RELEVANT ARCH. DRAWINGS.

S.M. SHARMA
Council of Architecture
Registration No. CA/1999/

for C.P. Kukreja Architects
(S.K. Nandi)
B. Engg, M.Sc. Engg (U.K.), M.I. Struct.E. (London, U.K.
Chartered Structural Engineer
Member: Institution of Structural Engineers, London, U.K.
Membership No. 0200960
Member: Association of Consulting Engineers, India
Membership No. M60
Fellow: Indian Association of Structural Engineers, India
Membership No. F-025

CLIENT
ANDHRA PRADESH INDUSTRIAL INFRASTRUCTURE CORPORATION LTD. (APIIC)

PROJECT
PROPOSED MILLENIUM IT TOWER BUILDING ON PLOT NO:- 16&17 AT HILL NO:-3 MADHURAWADA, VISAKAHPATNAM A.P.

DATE	CHECKED BY	APPROVED BY
AUGUST 2017	S.K.NANDI	S.K NANDI
SCALE	DRAWN BY	ARCHITECT
1:50,1:20	ALICE WILSON	S.M SHARMA

DRAWING TITLE
STRUCTURAL DETAILS OF GATE HOUSE

ARCHITECTS:-
C. P. KUKREJA ARCHITECTS.
ASHIRWAD BUILDING,
D-1,GREEN PARK,
NEW DELHI - 110016
PHONE :- 26563953 FAX :- 26855770
EMAIL-cpke @ cpkukreja .com

CAD FILE NO. 01-S-APHC-IT-GH-01.dwg
REVISION R0
DRAWING NO. 15003/APIIC/ITB/GH/S-01