

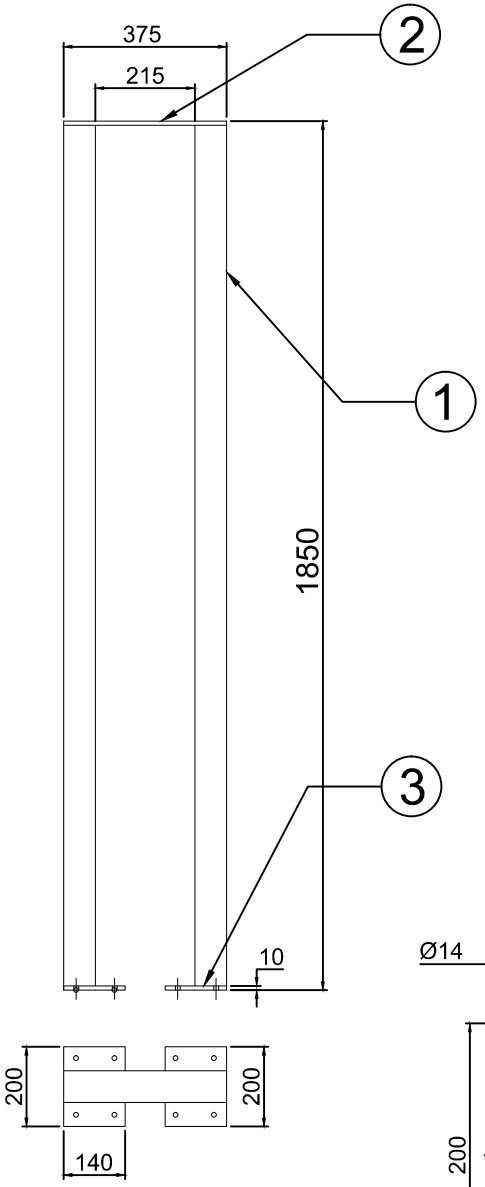


POST

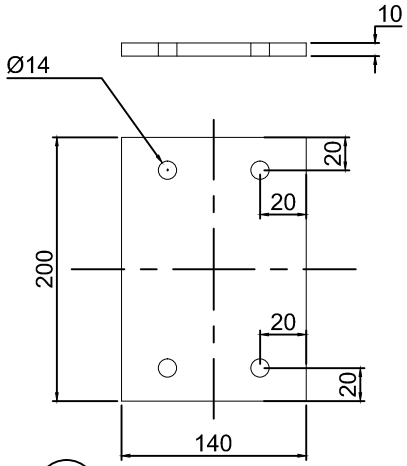

3 BASE PLATE

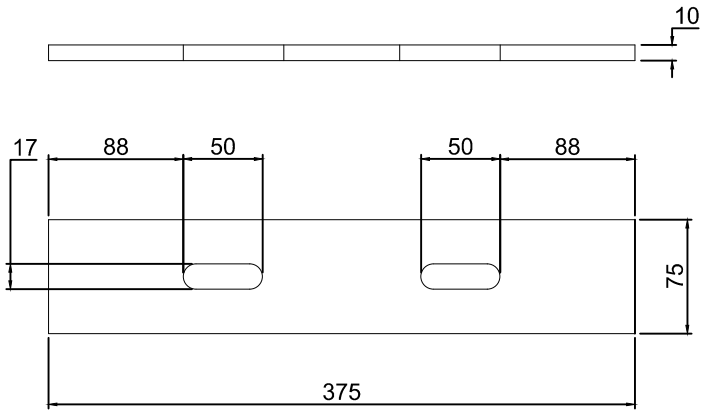

2 TOP PLATE

SR.NO	DESCRIPTION	SPECIFICATION	QTY	WEIGHT
5	NYLON WHEEL	Ø50 X 75L WITH M16 STUD	12 NOS	
4	ANCHOR BOLT	M12 X 150 L	48 NOS	
3	M.S FLAT	140 X 10 X 200L	12 NOS	27 KGS
2	M.S FLAT	75 X 10 X 375L	6 NOS	15 KGS
1	SQ. TUBE	80 X 80 X 3.2 THK X 1830L	12 NOS	180 KGS

This drawing & designing is the property of NIHVA TECHNOLOGIES. Not to be sold or copied to any other concern.

TITLE				
SLIDING GATE POST DRAWING				
	NAME	SIGN	DATE	
DRAWN	P.V.A		31.05.19	
CHECK	V.M.T		31.05.19	
APPROVAL				
If any queries contact : design@nihva.com				
ALL DIMENSION ARE IN mm				

NIHVA TECHNOLOGIES PVT. LTD.
NIHVA TECHNOLOGIES PVT. LTD. PUNE
Tel : 020 66304033
Email:- info@nihva.com
Website:- www.nihva.com

CLIENT -			
PROJECT -			
SITE LOCATION -			
DWG. NO. : NIHVA/19-20/VDR/054			REV.- 0
SCALE: NTS	WT:		SHEET: 01 OF 01