




4 SECTION SCALE 1:100

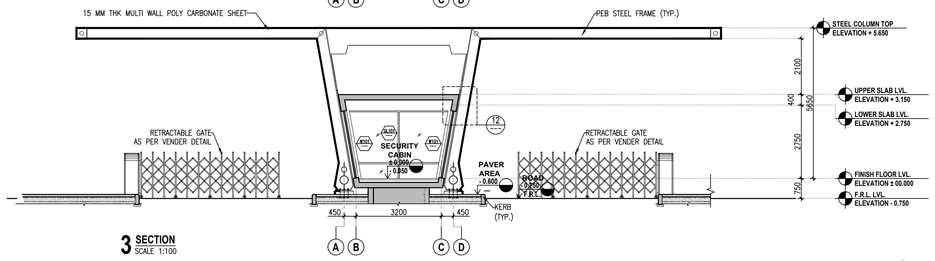


3 SECTION SCALE 1:100

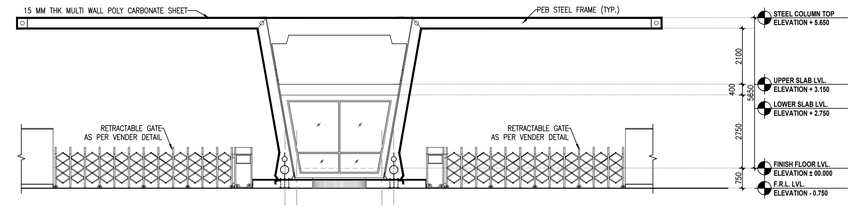


7 ELEVATION SCALE 1:100

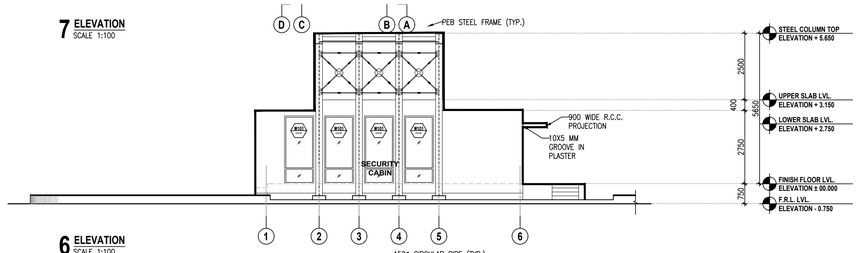


6 ELEVATION SCALE 1:100

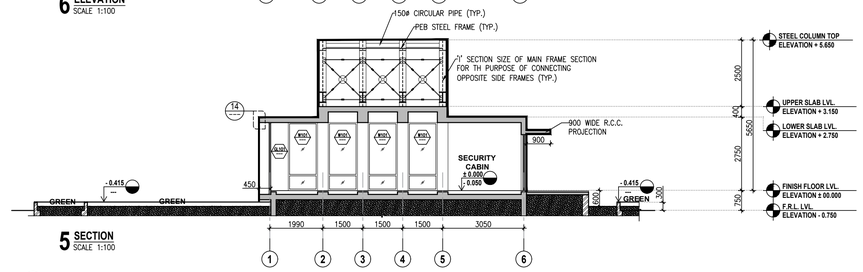


5 SECTION SCALE 1:100

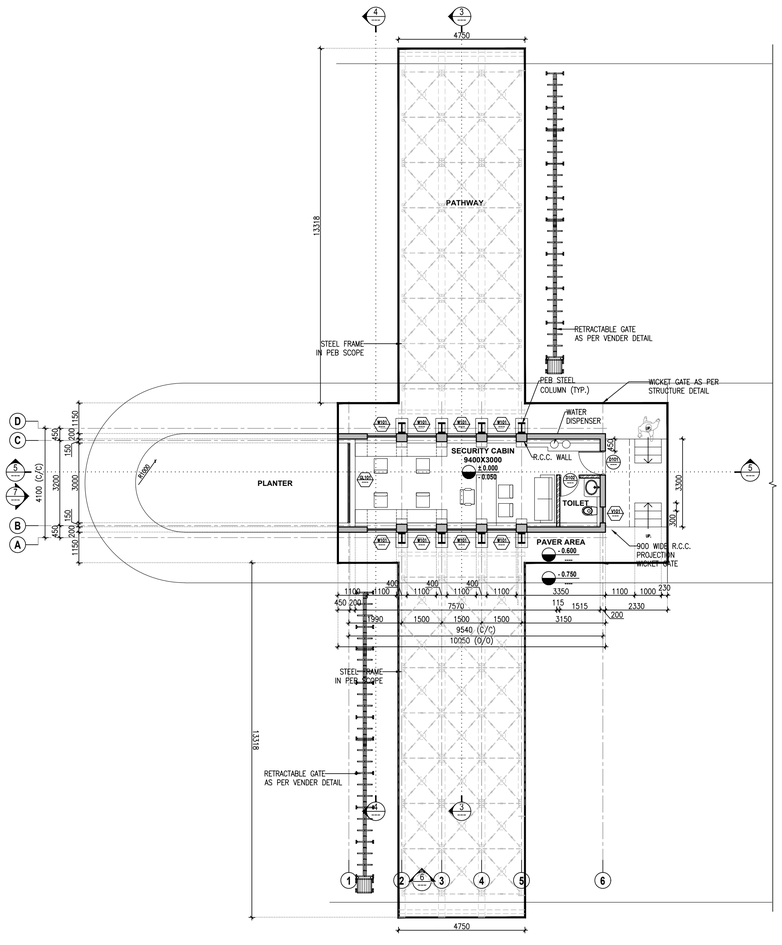

1 GROUND FLOOR PLAN (+ 0.900 LVL) SCALE 1:100

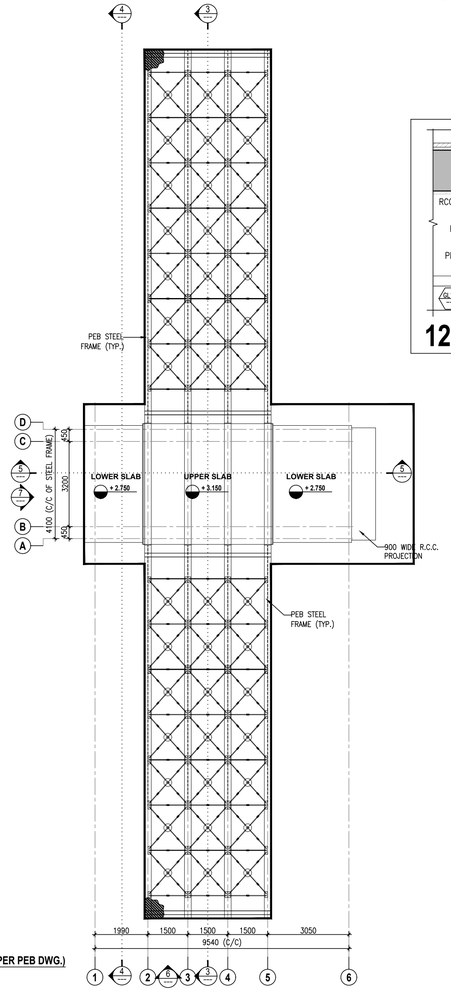

2 TOP PLAN (AS PER PEB DWG.) SCALE 1:100

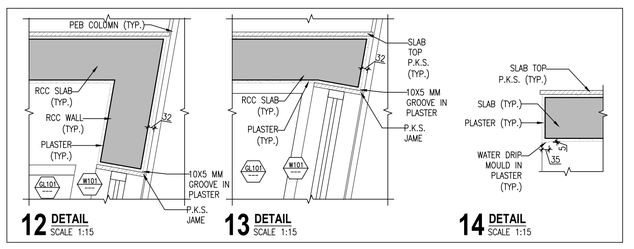

12 DETAIL SCALE 1:15 **13 DETAIL** SCALE 1:15 **14 DETAIL** SCALE 1:15

THIS DRAWING & DESIGN IS THE SOLE PROPERTY OF VMS & SHALL NOT BE COPIED, TRACED OR REPRODUCED BY ANY MEANS WITHOUT PRIOR WRITTEN CONSENT OF THE FIRM.

GENERAL NOTES :

1. ALL THE DIMENSIONS ARE UNFINISHED DIMENSIONS.
2. ALL DIMENSIONS ARE IN MM AND LEVELS ARE IN MT, UNLESS OTHERWISE MENTIONED.
3. ALL THE DIMENSIONS SHALL BE READ & NOT TO BE MEASURED.
4. IN CASE OF ANY DISCREPANCY, BRING IT TO THE NOTICE OF THE ARCHITECT IMMEDIATELY.
5. DETAIL DRAWING PRECEDES THE GENERAL DRAWING

IMPORTANT NOTE :

1. CIVIL CONTRACTOR NEEDS TO SUBMIT THE DETAILED SHOP DRAWING OF GLAZING , DOOR – WINDOW & VENTILATION ALONG WITH NECESSARY JUNCTION & FIXING DETAILS FOR CONSULTANTS APPROVAL PRIOR TO THE EXECUTION

STANDARD DRAWING SYMBOLS:

+ FINISHED LEVEL
+ UNFINISHED LEVEL

SECTION SYMBOL
UPPER HALF INDICATES DIAGRAM NO. (NUMERICAL VALUE) IN DRAWING SHEET & LOWER HALF INDICATES DRAWING NO.

ELEVATION SYMBOL
UPPER HALF INDICATES DIAGRAM NO. IN DRAWING SHEET & LOWER HALF INDICATES DRAWING NO.

WINDOW SYMBOL
UPPER HALF INDICATES WINDOW NO. & LOWER HALF INDICATES DRAWING NO.

DOOR SYMBOL
UPPER HALF INDICATES DOOR NO. & LOWER HALF INDICATES DRAWING NO.

GRAPHIC LEGEND :

MASONRY CUT IN PLAN/SECTION.

RCC COLUMN CUT IN PLAN.

SCHEDULE OF OPENINGS:


MKD.	SIZE	SILL HT.	LINTEL HT.	TOTAL NO.	REMARKS
D101	900x2100	----	2100	1	ALLUMINIUM FRAME WITH GLASS DOOR
D102	750x2100	----	2100	1	ALLUMINIUM FRAME WITH FLUSH DOOR
GL101	2700x2750	----	2750	1	GLAZING
W101	1100x2550	----	2550	8	ALLUMINIUM FRAME WITH PARTLY FIX GLASS & PARTY VERTICAL SLIDING WINDOW
V101	600x600	1500	2100	1	ALLUMINIUM FRAME WITH ALUMINUM LOUVERS

FOR TENDER

NO.	DATE	DESCRIPTION	DRAWN BY	CHECKED BY

REVISION HISTORY

KEY PLAN
SCALE : N.T.S.

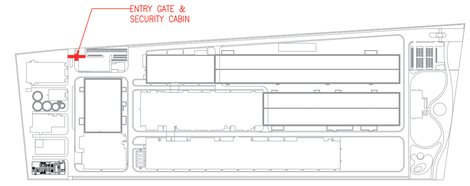

REFERENCE DRAWINGS :

01. ARCHITECTURAL :	-
02. STRUCTURAL :	-
03. HVAC :	-
04. ELECTRICAL :	-
05. UTILITIES :	-

GROUND FLOOR PLAN, SECTION, ELEVATION & DETAIL

MAIN ENTRANCE GATE

AGRAWAL METAL WORKS(P) LTD.

PROJECT NO.	SCALE :	DRAWN :	ASHISH C
3824	AS NOTED	CHECKED:	BHAKTI B
	DATE : 03-12-2024	APPROVED:	DARSH D
		COORDINATION CHECKED:	DARSH D

VMS ENGINEERING & ARCHITECTURE

VMS ENGINEERING & DESIGN SERVICES (P) LTD.
CHITRAKOOT FLATS, BEHIND TIMES OF INDIA, OFF ASHRAM ROAD,
AHMEDABAD-380 009. PHONE: +91 (079) 2658-8829/4488, 40236236
FAX : +91 (079) 2658 3596 WWW.VMSCONSULTANTS.COM

SHEET SIZE	DRAWING NO.	TENDER	REVISION:
A1	T.A.8.101	T	R0