




SIDE VIEW

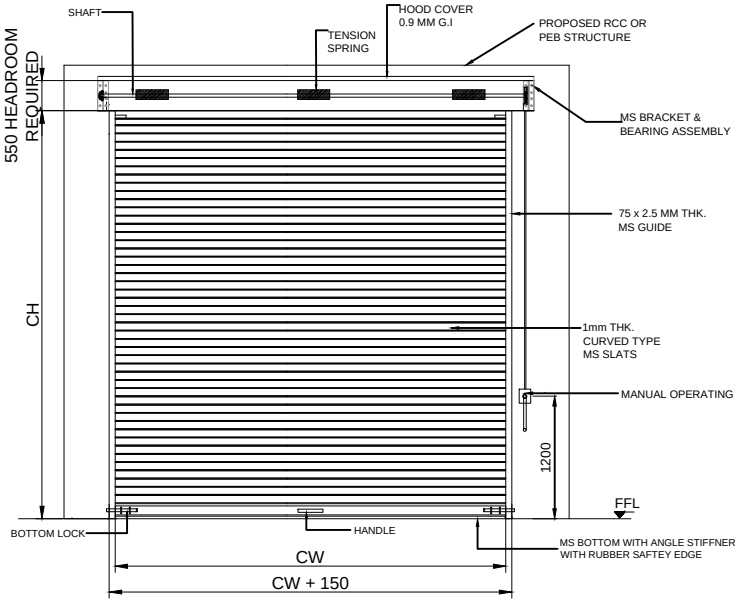


INSIDE ELEVATION

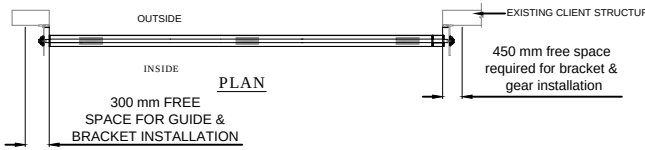


PLAN

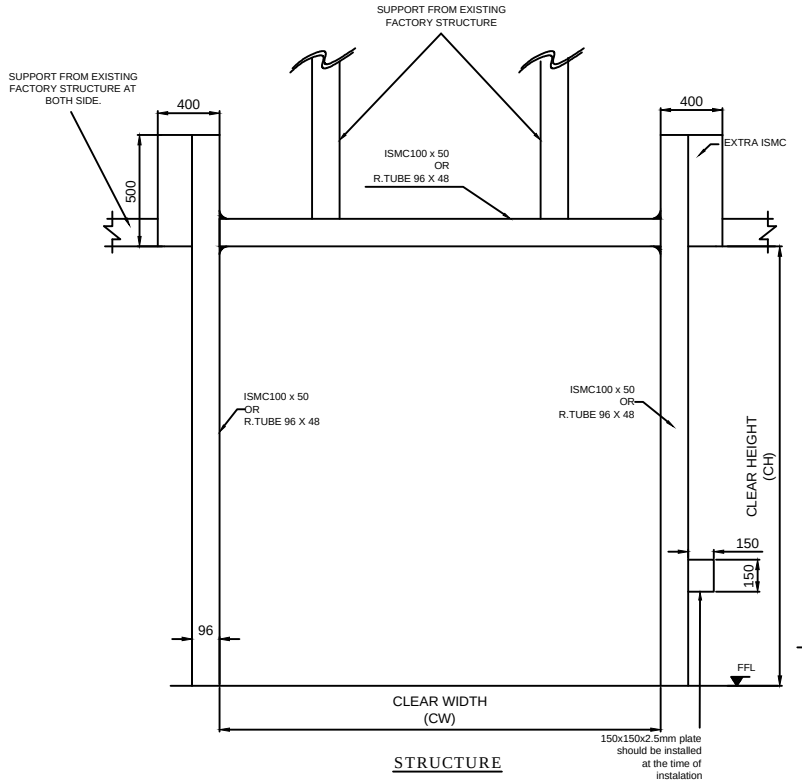

STRUCTURE

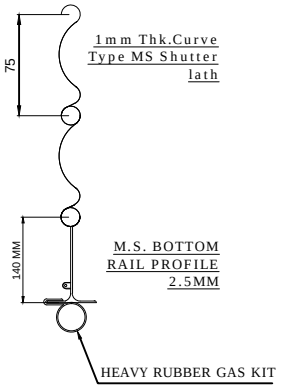

M.S. BOTTOM RAIL PROFILE 2.5MM

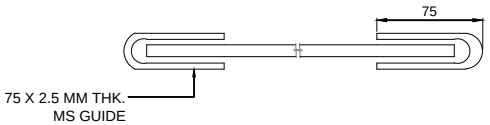

NOTE-
1. ALL CIVIL WORK WILL BE CLIENT'S SCOPE.
2.IF TECHNICAL STRUCTURE REQUIRED FOR SHUTTER IS IN CLIENT'S SCOPE.

SR NO	CLEAR WIDTH (CW)	CLEAR HEIGHT (CH)	QUANTITY
1	2000	3600	01 NO

TOLERANCE - ±10mm

RAL CODE	RAL COLOR	APPROVED
RAL 9007	GREY ALUMINIUM	APPROVED

This drawing & design is the property of NIHVA TECHNOLOGIES. Not to be sold or copied to any other concern.

TITLE
GEAR OPERATED ROLLING SHUTTER

NIHVA TECHNOLOGIES PVT. LTD.

NIHVA TECHNOLOGIES PVT. LTD. PUNE
Tel : 020 66304033
Email:- info@nihva.com
Website:- www.nihva.com

	NAME	SIGN	DATE
DRAWN	P.A		03.09.2020
CHECK	G.J		03.09.2020
APPRD.			

CLIENT - RMK INFRASTRUCTURE
PROJECT -
SITE LOCATION - TALEGAON,PUNE.
If any queries contact : design@nihva.com
DWG. NO. : NIHVA/ 20-21/0048 REV- R00
ALL DIMENSION ARE IN mm
SCALE: NTS WT: SHEET: 01 OF 01