




Opening Direction Left side(View from outside)

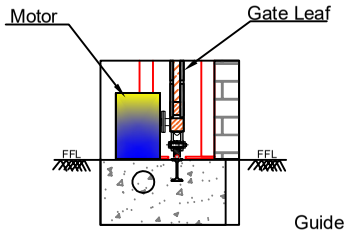


Deatil : A

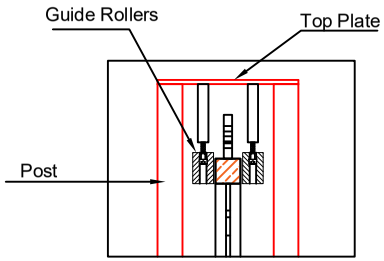

Deatil : B

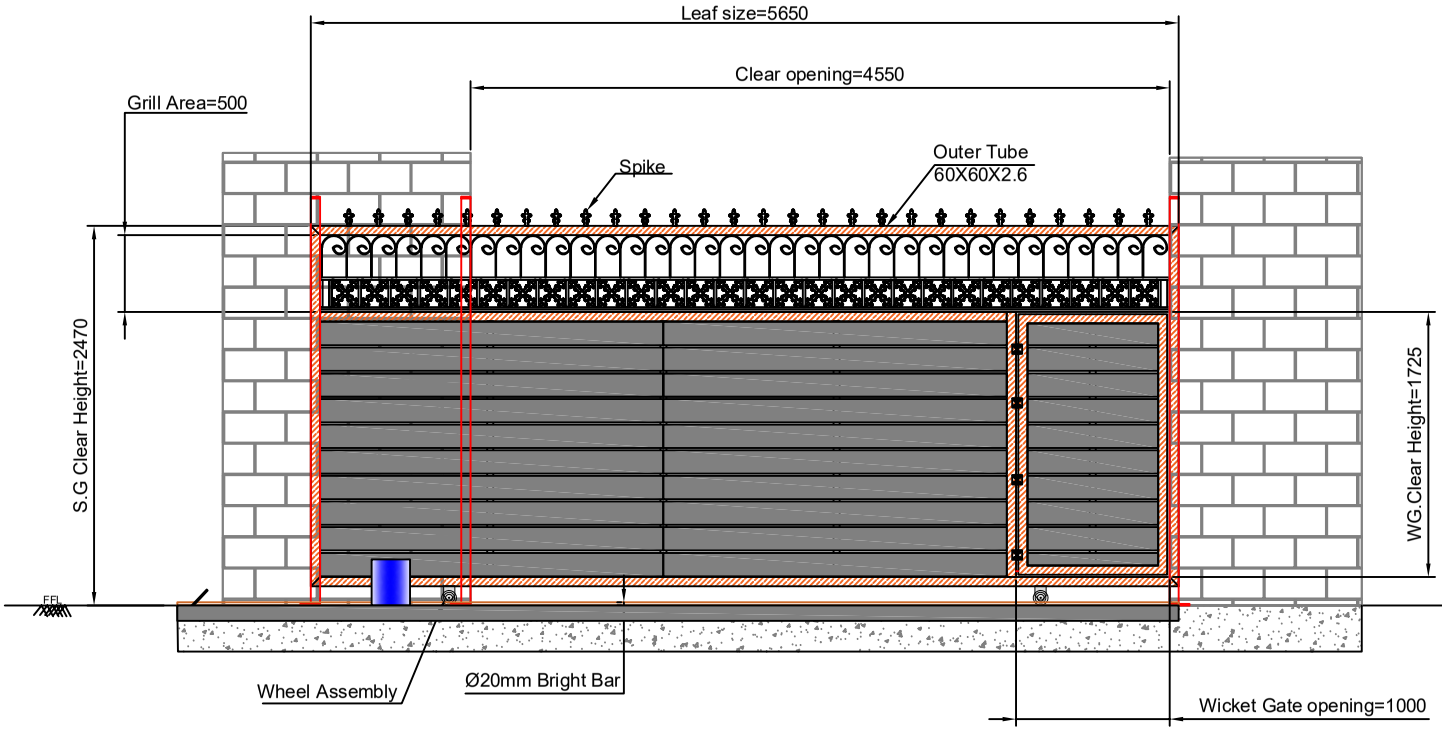

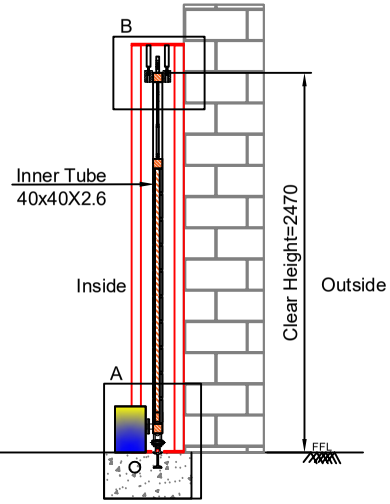

Opening Direction Left side(View from outside)

Note:-

1.All Dimension are in MM.
2.Grill and Spike Deasign may change as per Convenient.
3. Kindly Confirm parking side(Left or Right as per site) i,e view from outside
4. Required all civil work is in Client Scope.
5.Installation and Fabrication tolerance will be ±20mm
6.Required Parking will be 5750
7. Coating : Approved RAL

RAL CODE	SHADE	COLOUR
RAL 9001	CREAM	
RAL 9002	GREY WHITE	
RAL 9010	PURE WHITE	
RAL 5002	ULTRAMARINE BLUE	
RAL 7035	LIGHT GREY	
RAL 7001	SILVER GREY	

Rev No.	Revision	Date	Revised By

This drawing & design is the property of NIHVA TECHNOLOGIES. Not to be sold or copied to any other concern.

TITLE:-
Sliding Gate with Wicket Gate

NIHVA
NIHVA TECHNOLOGIES PVT. LTD.

NIHVA TECHNOLOGIES PVT. PUNE
Tel : 020 66304033
Email:- info@nihva.com
Website:- www.nihva.com

	NAME	DATE	SIGN
DRAWN	SUJATA	26/07/2022	
CHECK	M.S	26/07/2022	
APPRD.	A.K	26/07/2022	

If any queries contact : design@nihva.com

ALL DIMENSION ARE IN mm

CLIENT - Rohit Nair
LOCATION - Undri
PRODUCT - Sliding Gate | QTY-
DWG NO:- NIHVA/22-23/CLT/0073 | REV-00
SCALE: NTS | SCALE:-- 1:1 | SHEET: 01 OF 01