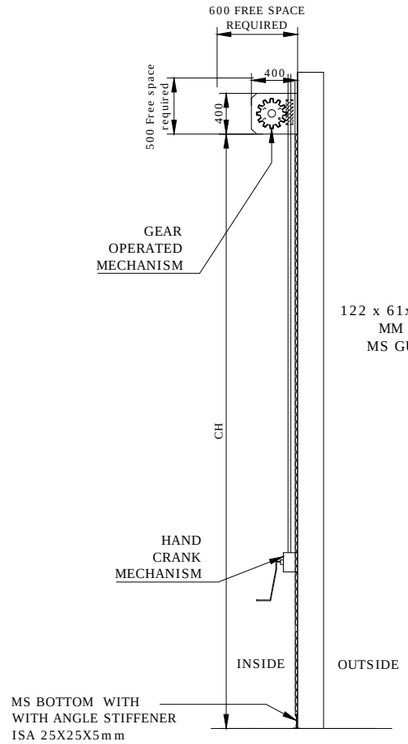
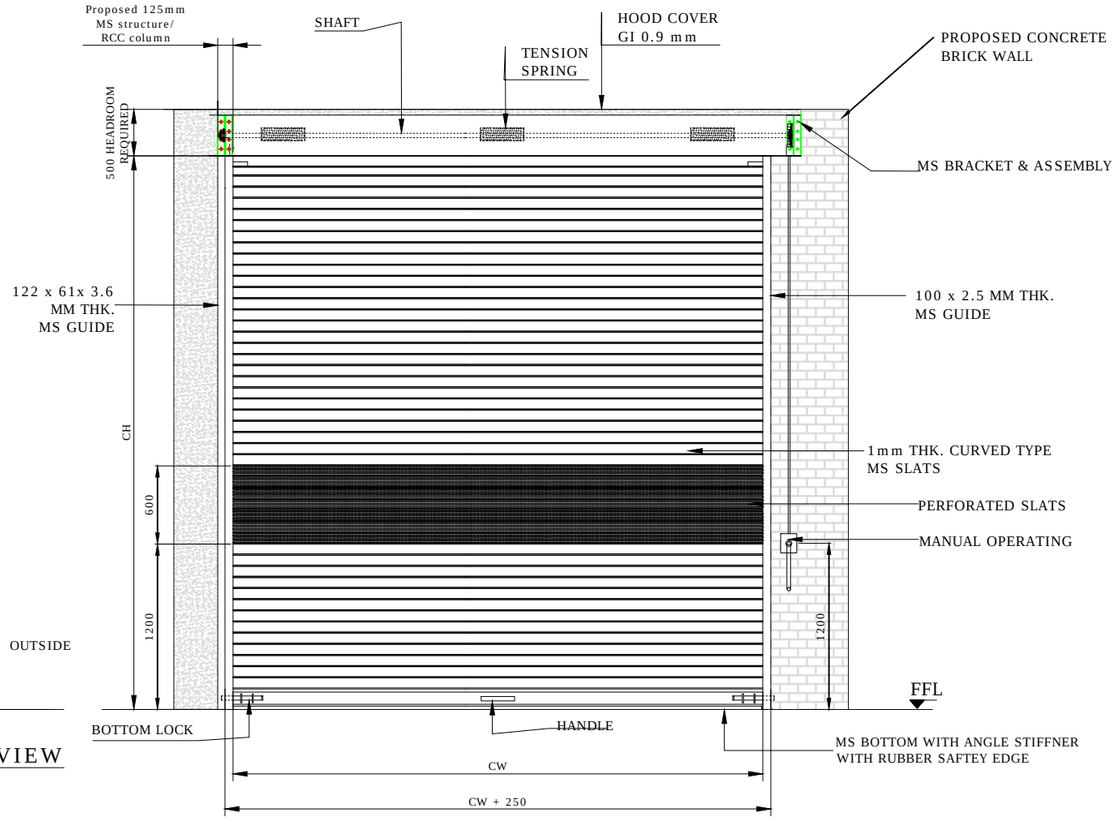
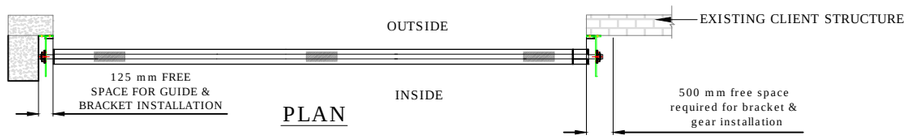


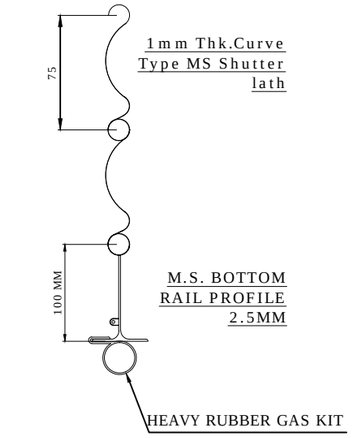

SIDE VIEW



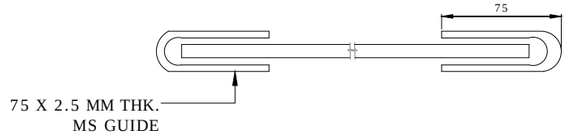

INSIDE ELEVATION




PLAN




M.S. BOTTOM RAIL PROFILE 2.5MM




| | | |
|---|---|---|
| RAL 9007 | GREY AL. | APPROVED |
| RAL 9010 | PURE WHITE | |
| RAL 9002 | GREY WHITE | |
| RAL 7035 | LIGHT GREY | |
| RAL 5002 | ULT. M. BLUE | |
| RAL CODE | RAL COLOR | APPROVAL |

NOTE-
1. MOUNTING LOCATION: INSIDE AREA
2. LEFT GUIDE WILL BE MOUNTED ON STRUCTURE AND RIGHT WILL BE MOUNTED ON CONCRETE WALL.

TOLERANCE - ±10mm

| SR NO | ( CW ) CLEAR WIDTH | ( CH ) CLEAR HEIGHT | QUANTITY |
|---|---|---|---|
| 2 | 3875 | 3300 | 01 NO |
| 1 | 3875 | 3600 | 01 NO |

This drawing & design is the property of NIHVA TECHNOLOGIES. Not to be sold or copied to any other concern.

| | NAME | SIGN | DATE |
|---|---|---|---|
| DRAWN | G.I.P | | 15.04.2022 |
| CHECK | A.K. | | 15.04.2022 |
| APPRD. | | | |

TITLE: GEAR OPERATED ROLLING SHUTTER

NIHVA TECHNOLOGIES PVT. LTD.
Website:- www.nihva.com
NIHVA TECHNOLOGIES PVT. PUNE
Tel : 020 66304033
Email:- info@nihva.com

CLIENT - NIHVA TECHNOLOGIES
PROJECT - ROLLING SHUTTER
SITE LOCATION - PUNE

If any queries contact : design@nihva.com
DWG. NO. : NIHVA/22-23/VDR/0002
REV- R00
ALL DIMENSION ARE IN mm
SCALE: NTS
WT:
SHEET: 01 OF 01