

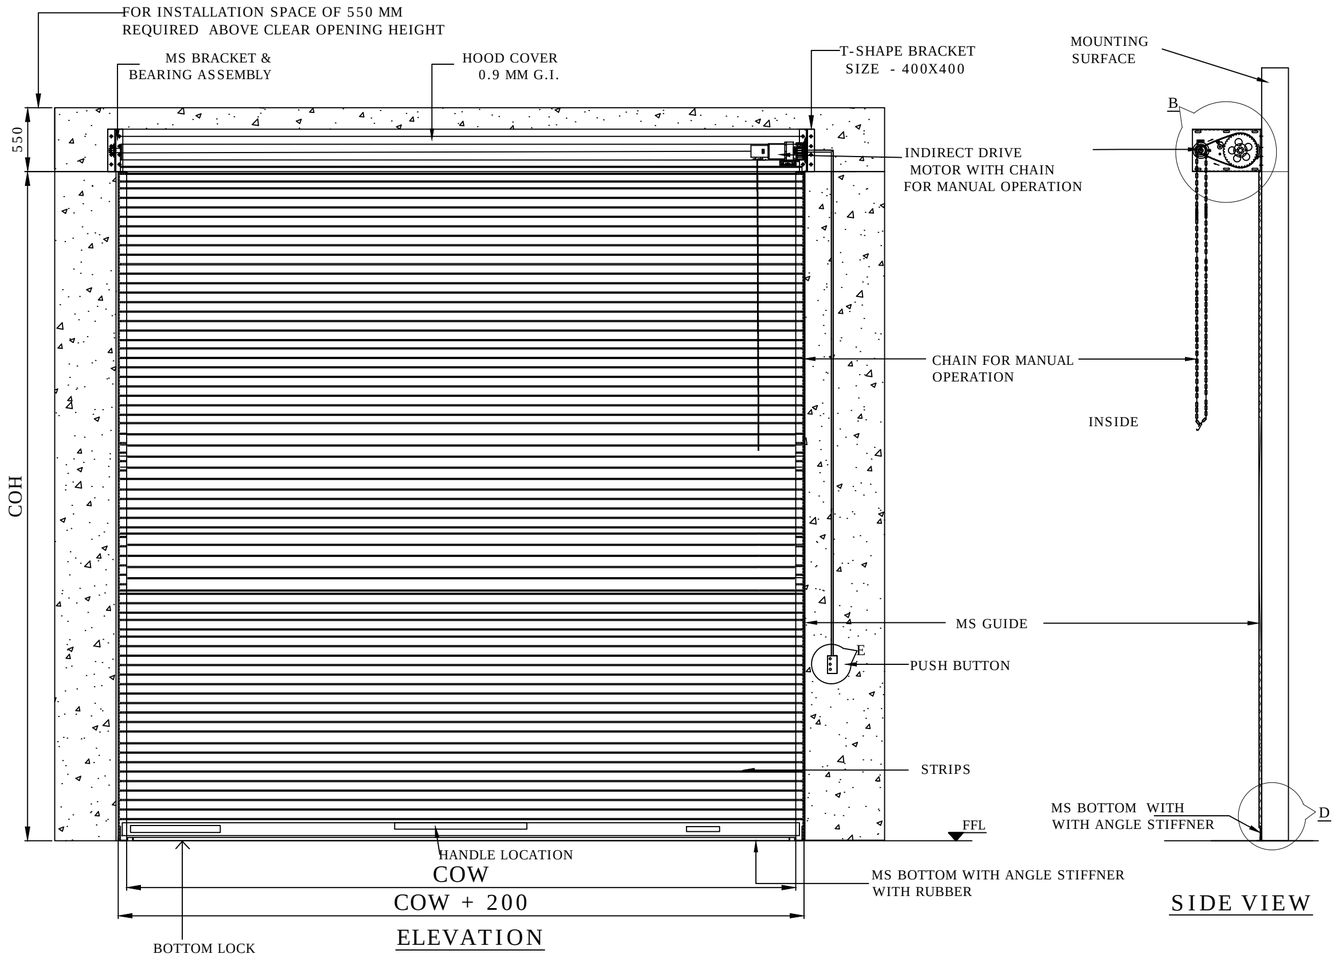


SIDE VIEW

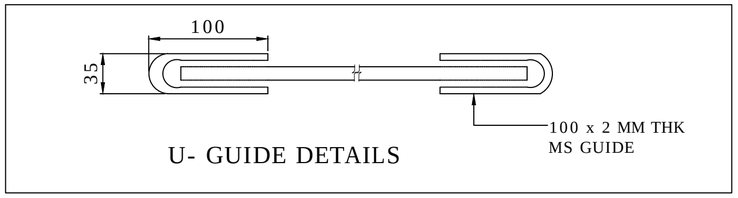


U- GUIDE DETAILS


RAL SHADE FOR POWDER COATING
1. RAL 7016- MEGABLOCK LOCATIONS
2. RAL 7005- FOR LOCATIONS OF COMPRESSOR , DG , WTP & HT PANEL ROOM

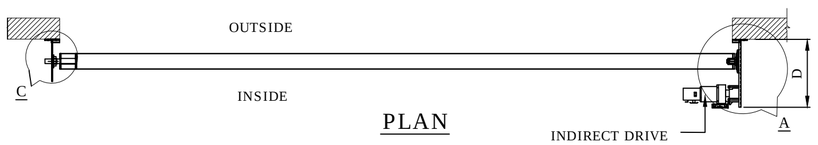


PLAN

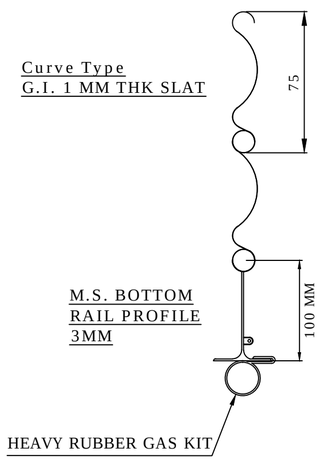

DETAILS : D

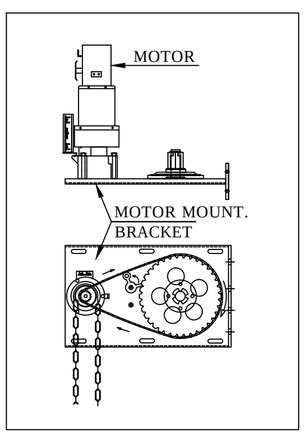

DETAILS : A & B

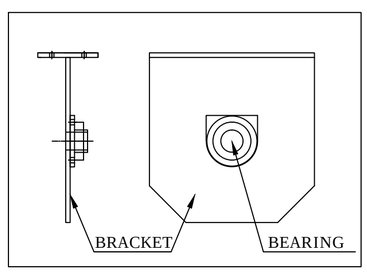

DETAILS : C

SR NO	CLEAR OPENING WIDTH (COW)	CLEAR OPENING HEIGHT (COH)	QUANTITY	LOCATION
5	4000	4000	1 NO	RS3
4	3000	3000	1 NO	RS3
3	3000	3500	1 NO	TRS1
2	3250	3800	1 NO	RS2
1	3000	3500	1 NO	RS1

This drawing & design is the property of NIHVA TECHNOLOGIES. Not to be sold or copied to any other concern.

TITLE GI MOTORIZED ROLLING SHUTTER

	NAME	SIGN	DATE
DRAWN	S.M.S.		24.7.2021
CHECK	S.M.		24.7.2021
APPRD.			

NIHVA TECHNOLOGIES PVT. LTD.
NIHVA TECHNOLOGIES PVT. LTD. PUNE
Tel : 020 66304033
Email:- info@nihva.com
Website:- www.nihva.com

CLIENT - L&T CONSTRUCTIONS

PROJECT -

SITE LOCATION -

If any queries contact :design@nihva.com

DWG. NO. : NIHVA/21-22/046/MRS

REV- R00

ALL DIMENSION ARE IN mm

SCALE: NTS

WT:

SHEET: