



M12X60mm HEX
BOLT SHOULD BE
WELDED TO PLATE BEFORE
INSERTING IN FOUNDATION
(CLIENT'S SCOPE)

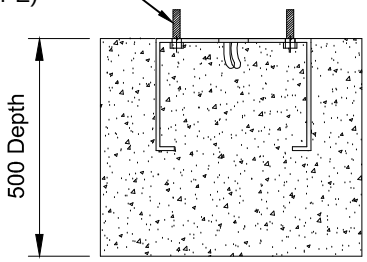

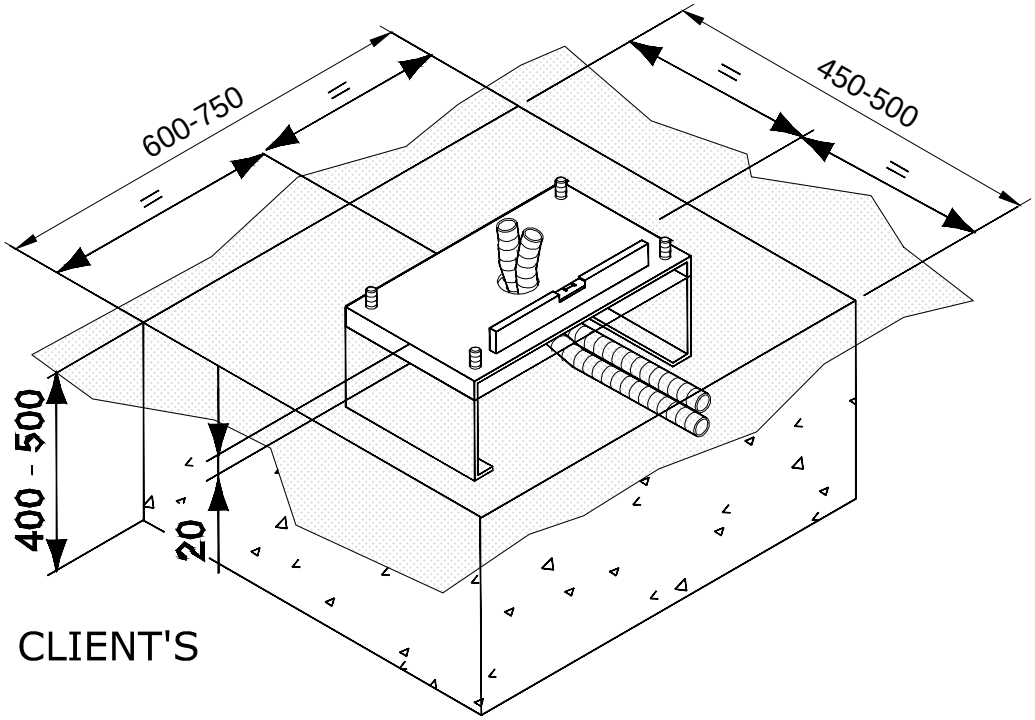

FOUNDATION DETAILS (IN CLIENT'S SCOPE)

TOLERANCE - ±10mm

This drawing & design is the property of NIHVA TECHNOLOGIES. Not to be sold or copied to any other concern.

TITLE: FOUNDATION FOR BOOM BARRIER			NIHVA TECHNOLOGIES PVT. LTD. PUNE Tel : 020 66304033 Email:- info@nihva.com Website:- www.nihva.com
	SIGN	DATE	
DRAWN	OMKAR	17-11-2017	CLIENT - LUPIN LIMITED
CHECK	SHEKHAR.	17-11-2017	PROJECT -
APPROVAL	SHEKHAR	17-11-2017	SITE LOCATION - MIHAN,NAGPUR
			DWG. NO. : NIHVA/17-18/ 0294 REV-0
If any queries contact : projects@nihva.com			SCALE: NTS WT: SHEET: 01 OF 01
ALL DIMENSION ARE IN mm			