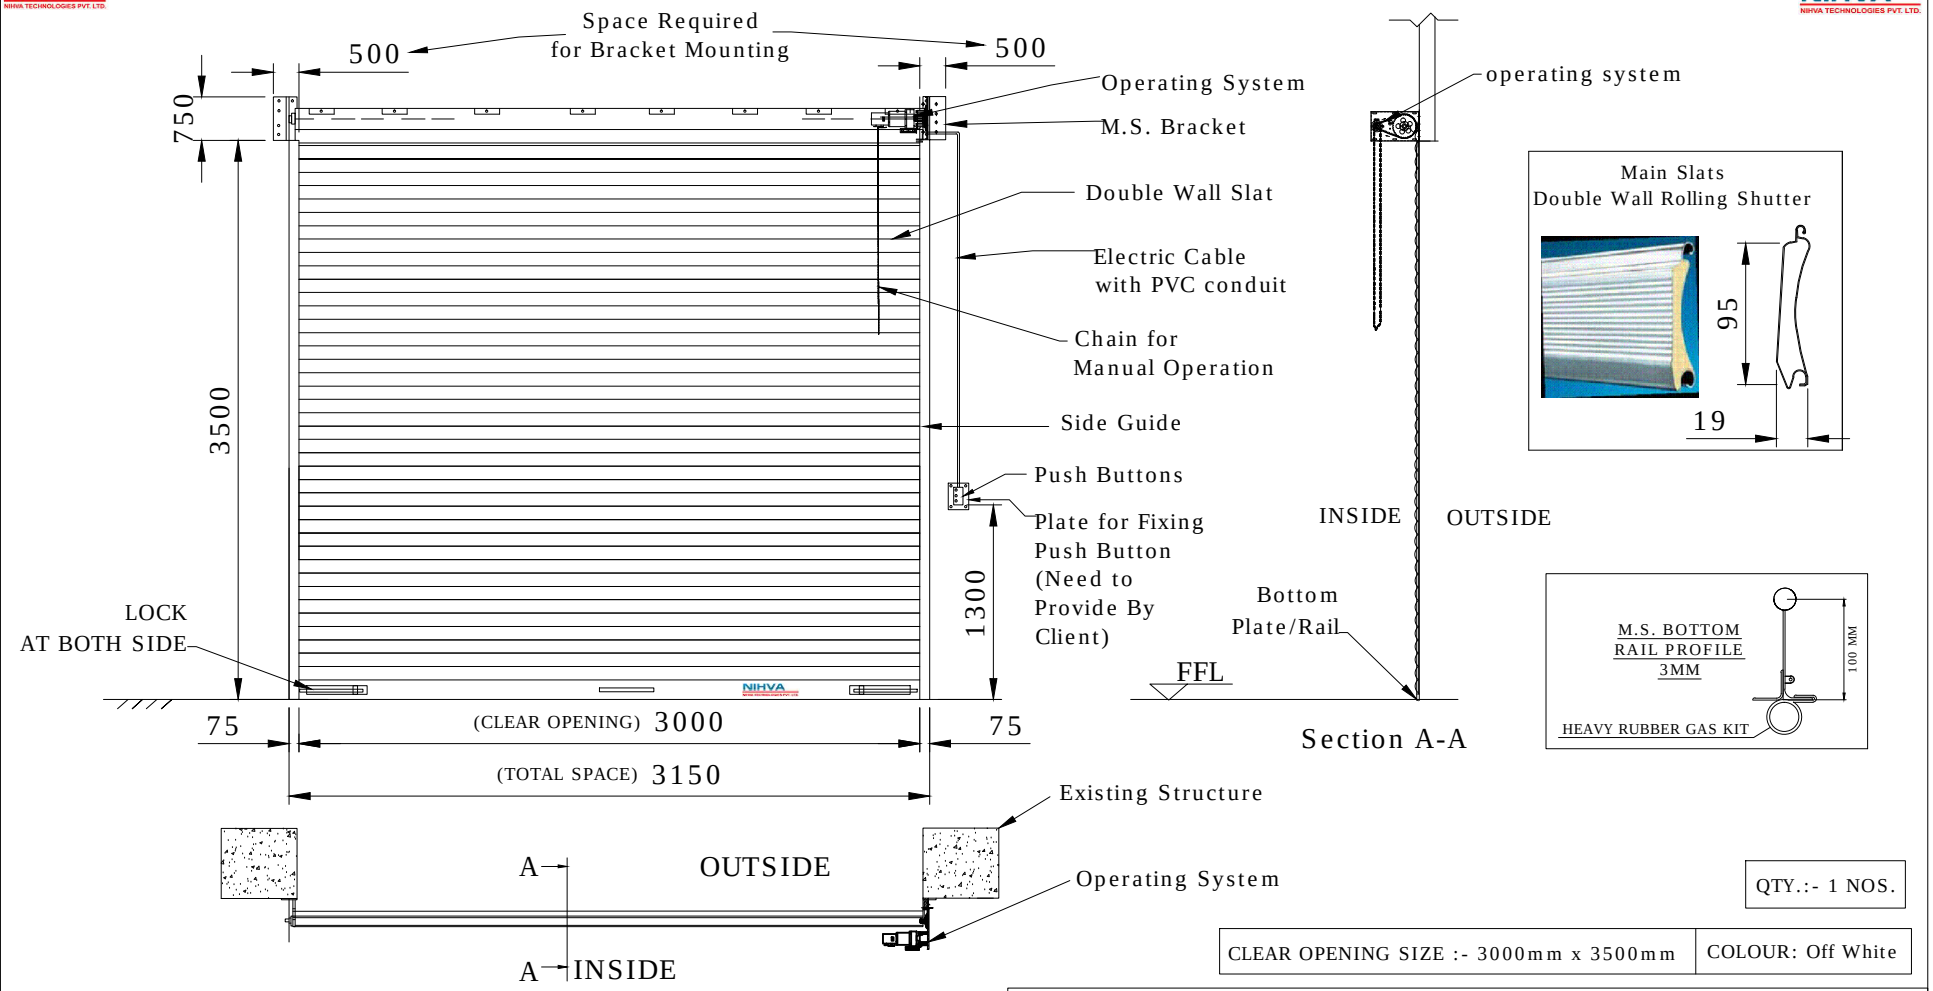



QTY.:- 1 NOS.

| CLEAR OPENING SIZE :- 3000mm x 3500mm | COLOUR: Off White |
|---|---|

| Sr. No. | Details | Specification |
|---|---|---|
| 1) | Slats Profile | 95mm x 19mm with PU filled inside |
| 2) | Guide Channel | 75mm x 40mm |
| 3) | Shaft | 130mm OD with heavy duty flanges and hardware |
| 4) | Bottom Rail | 125mm x3mm thick with extra angle support. Locking arrangement provides |
| 5) | Brackets | 600mmx450mmx3mm thickness |

This drawing & designing is the property of NIHVA TECHNOLOGIES. Not be sold or copy to any other concern.

TITLE:

DOUBLE WALL
ROLLING SHUTTER

CLIENT APPROVAL

ALL DIMENSION ARE IN mm

| | SIGN | DATE |
|---|---|---|
| DRAWN | ABHIJIT | 14/10/15 |
| CHECK | ANIL | 14/10/15 |
| REV. | 00 | |
| APPRD. | | |
| MFG | | |
| Ref. No. | | |

NIHVA TECHNOLOGY
PVT. LTD. PUNE
Tel : 020 66304033
Email:- info@nihva.com
Website:- www.nihva.com

CLIENT - PHENIX

PROJECT - ADANI

SITE - GUJRAT

DWG. NO. -NIHVA/15-16/142

SCALE: 01 | WT: | SHEET: 01 OF 01

If any queries contact : projects@nihva.com