


Shops Flooring Layout - Tower T5,T6 &T7

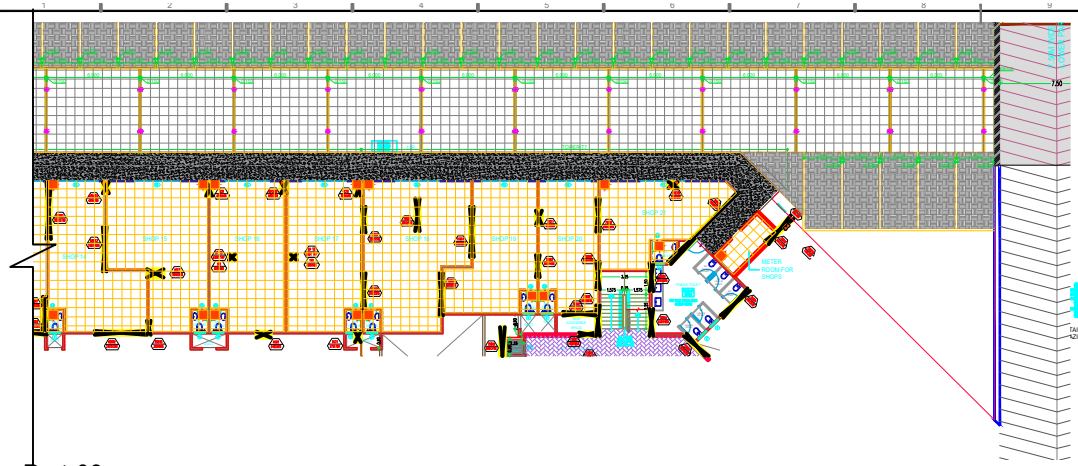

Part-03

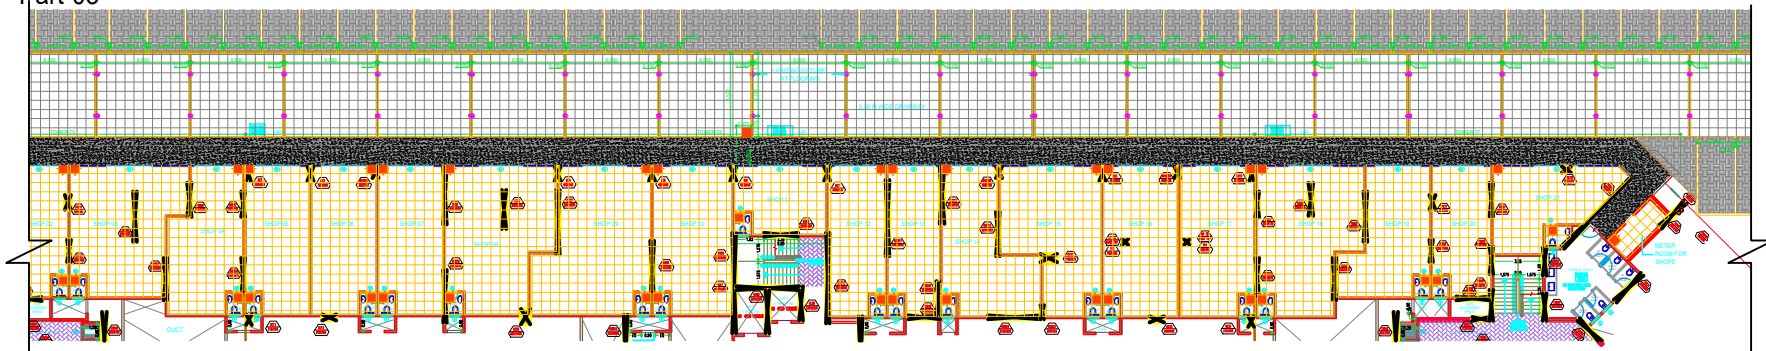

Part-02

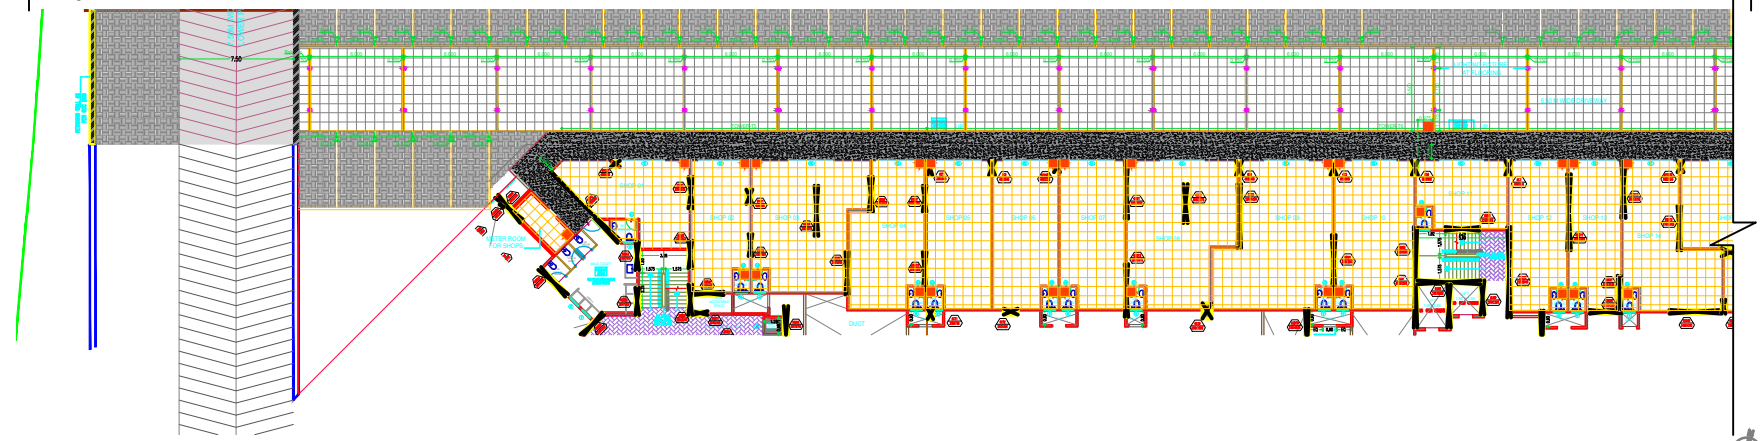


Part-01

Podium-1 Floor Plan T5,T6 & T7





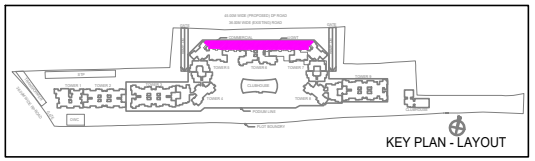

VK:a architecture
5th Floor,Nextgen Avenue,Sr.No.103(p), C.T.S No.2850,S.B.Road,Near ICC Trade Tower,Bahiratwadi, Pune.411016.
P +91 20 6626 8888
E mail@vkarch.com
W www.vkarch.com

Notes:
© VK:a architecture
01 DO NOT SCALE FROM THIS DRAWING, ONLY WRITTEN DIMENSIONS SHOULD BE FOLLOWED.
02 CONTRACTORS MUST CHECK & VERIFY THE DRAWING BEFORE EXECUTION AND DISCREPANCY IF ANY MUST BE REPORTED TO THE ARCHITECT.
03 FOR SIZES OF STRUCTURAL ELEMENTS PLEASE REFER STRUCTURAL CONSULTANTS' CURRENT DRAWINGS.
04 FOR DRAINAGE, PLUMBING, ELECTRICAL & LANDSCAPE DETAILS, PLEASE REFER CONSULTANTS' DRAWINGS.
05 CHANGES/DEVIATIONS MADE ON SITE WITHOUT CONSULTING THE ARCHITECT WILL BE AT THE TOTAL RESPONSIBILITY OF THE CLIENTS.

Structural Consultant: Strudcom Cons Pvt.Ltd.
PHE Consultant: Unicorn MEP Cons. Pvt. Ltd.
Electrical Consultant: Unicorn MEP Cons. Pvt. Ltd.
Fire Consultant: Unicorn MEP Cons. Pvt. Ltd.
Project Management Consultant: Colliers International

-0.60 x 0.60m TILE-
FLAMED GRANITE FLOORING ON PASSAGE & TREAD ON STEPS (AS PER SELECTION)
-START TILE

NOTES:
- TILE MAKE TO BE AS PER CLIENT SELECTION
- FOR TOILET FLOORING DETAILS REFER DRAWING NO..

Legend

50 MM SUNK
SLAB AT BEAM BOTTOM LVL
SLAB AT BEAM TOP LVL
125 THK NON STRUCTURAL WALL
150 THK NON STRUCTURAL WALL
200 THK NON STRUCTURAL WALL
300 THK NON STRUCTURAL WALL
MASS CONCRETE
150 MM THK MASONARY
200 MM THK MASONARY
125 MM THK MASONARY
100 MM THK MASONARY

Client Company's Name: M/s. Mhalunge Land Developers Pvt.Ltd
Mr Atul Chordia

Job Title: Proposed Residential Project at Sector R23, Maan-Mhalunge-Hinjewadi Township, Pune

Drawing Title: Shops Flooring Layout - Tower 5,6 & 7	Scale: 1:75 @ A1 Paper
Drawn by: Chandrakant	Checked by: Raksha
Date: 25/03/25	
Project No: 2218	Drawing No: 689
Revision: -	
Status: Advance Copy	Sign: