


Revision		Date	By
A	Corrected mullion hoist positions, floor pits altered	2022-09-02	EB
B	New measurements, doors redrawn	2022-10-11	EB

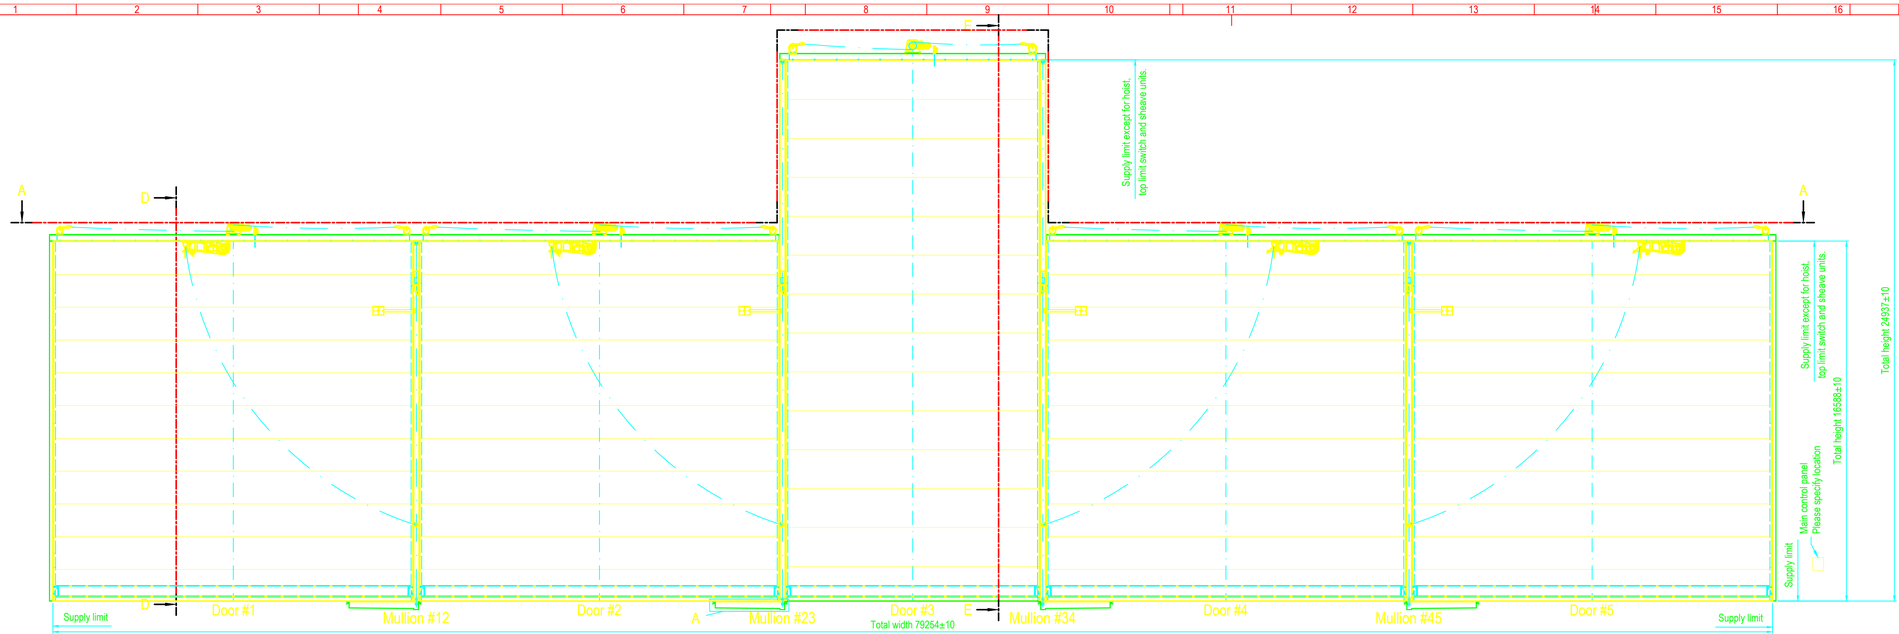

5.9T/27 Door #3

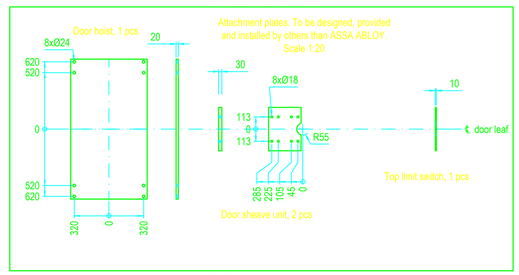

4.9T/27 Door #1, 2, 4 & 5

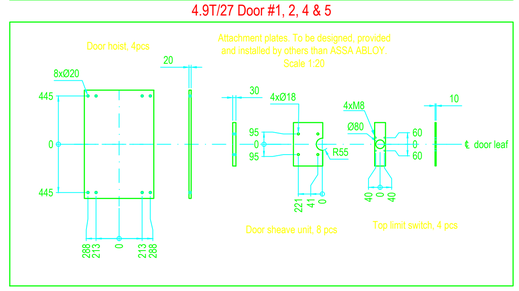

DOOR IDENTITY NUMBER: 84800001

LOAD DIAGRAM & NOTES, ref. to drwng. no. 77446

INTERFACE, SECTIONS ref. to drwng. no. 77445

INTERFACE, PLAN VIEWS ref. to drwng. no. 77444

DESIGNED: EB		SIZE: A1P	SCALE: 1:100
CODE: 84800		If not otherwise stated: Tolerances ISO 2768-m EN ISO 13920-B	
ITEM NO:		Cutting class ISO 9013-442	
DATE: 2022-08-23		Weld class ISO 5817-C	
ASSA ABLOY		Surface finish Smooth raw surface	

GMR Aero Technic Hangar1
India
Megadoor 79014x23000/14000
Interface, Elevation

DRAWING NO: 77443

REVISION: B

PLOT DATE