

SCISSOR LIFT SIZE	WIDTH (W)	LENGTH (L)	HEIGHT (H)	LIP (C) LENGTH
	2000	3000	800	300

PIT DIMENSION	WIDTH (W 1)	LENGTH (L 1)	DEPTH (D)	ALL DIMENSIONS ARE IN mm
	2150	3150	805	

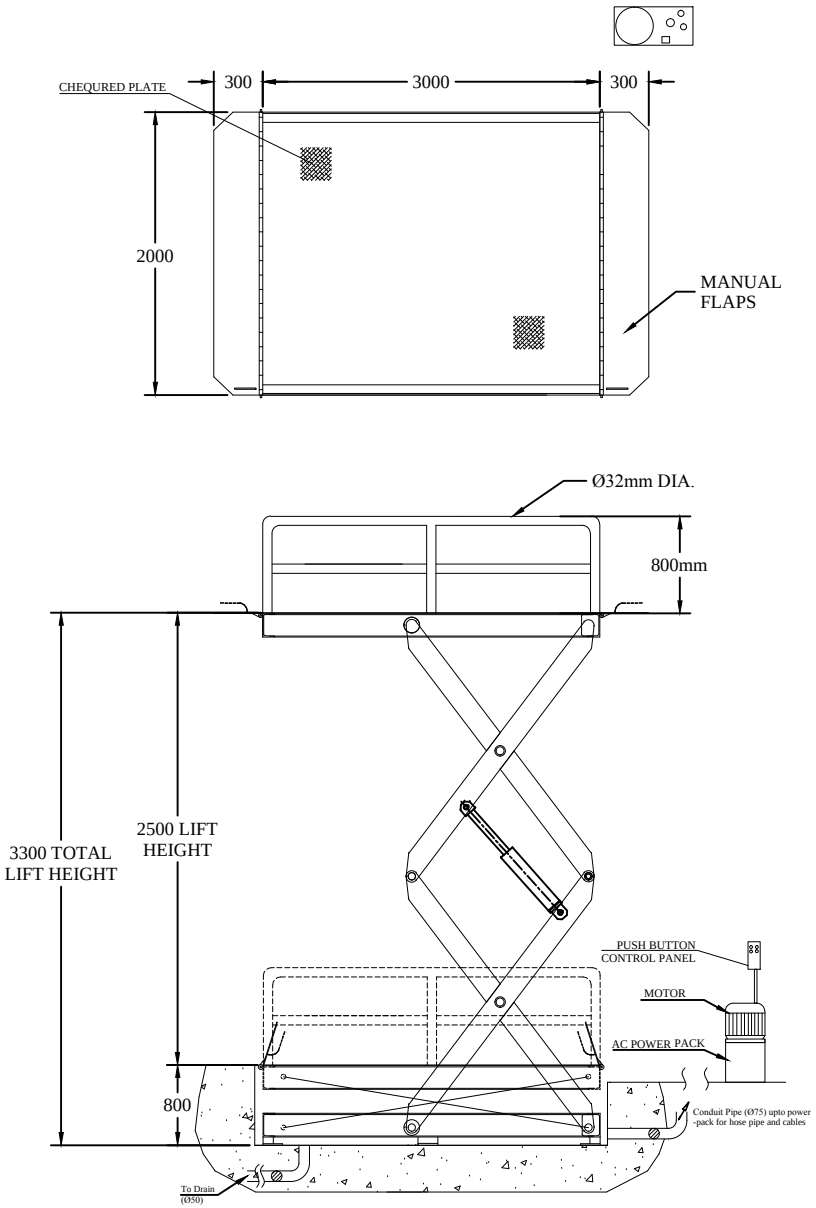

ELEVATION

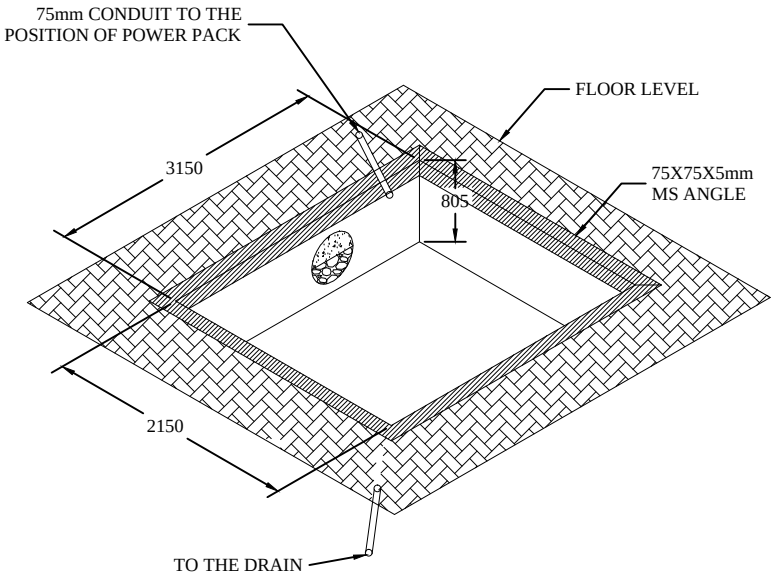

PIT DRAWING

REVISION 1- LIFT HEIGHT REVISED FROM 1800 TO 2500mm.

This drawing & designing is the property of NIHVA TECHNOLOGIES. Not be sold or copy to any other concern.

TITLE: SCISSOR LIFT

NIHVA TECHNOLOGIES PVT. LTD.
NIHVA TECHNOLOGY PVT. LTD. PUNE
Tel : 020 66304033
Email:- info@nihva.com
Website:- www.nihva.com

	SIGN	DATE
DRAWN	OMKAR	19/09/17
CHECK	SHEKHAR	19/09/17
REV.	0	
APPROVAL	SHEKHAR	19/09/17

CLIENT - SHILCHAR TECHNOLOGIES LTD.
PROJECT -
SITE -VADODARA , GUJARAT
DWG. NO. : NIHVA/17-18/0198/R01
If any queries contact : projects@nihva.com
SCALE: NTS | WT: | SHEET: 01 OF 01
ALL DIMENSION ARE IN mm

SCISSOR LIFT- 5000 KG CAPACITY