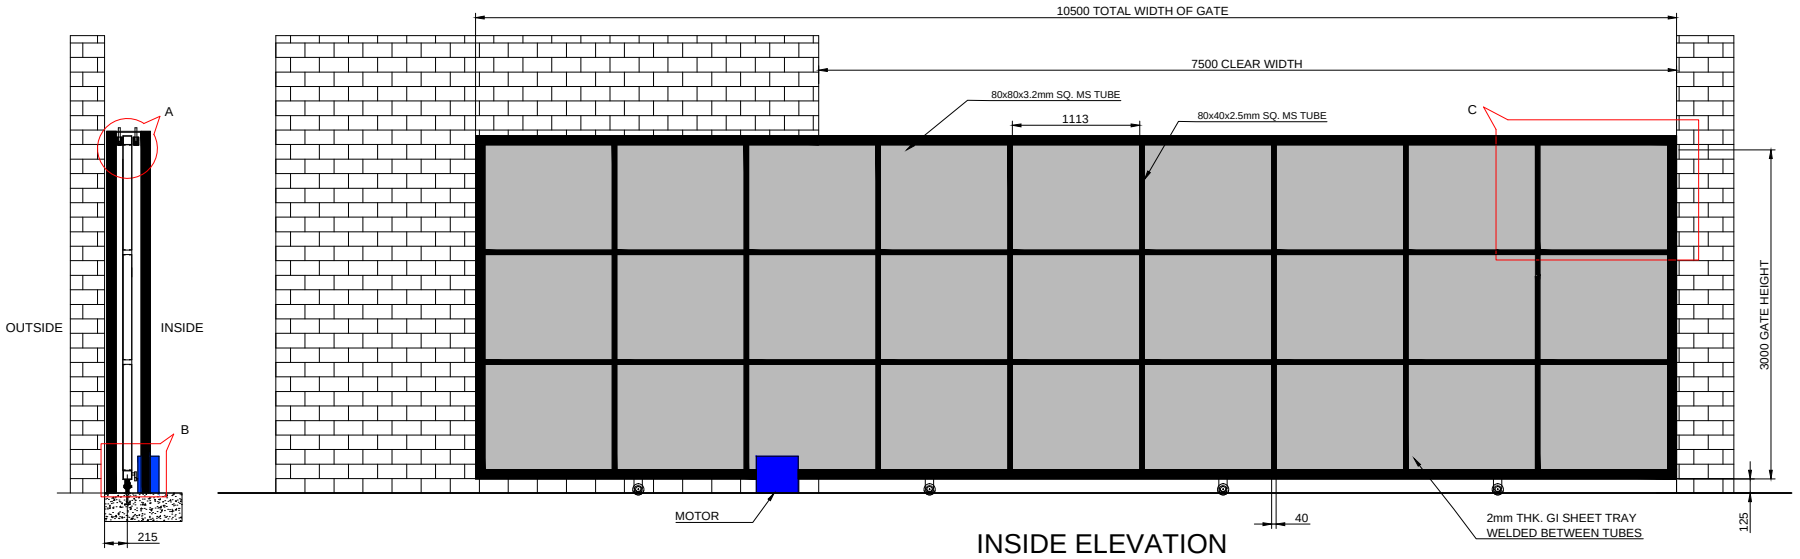

INSIDE ELEVATION

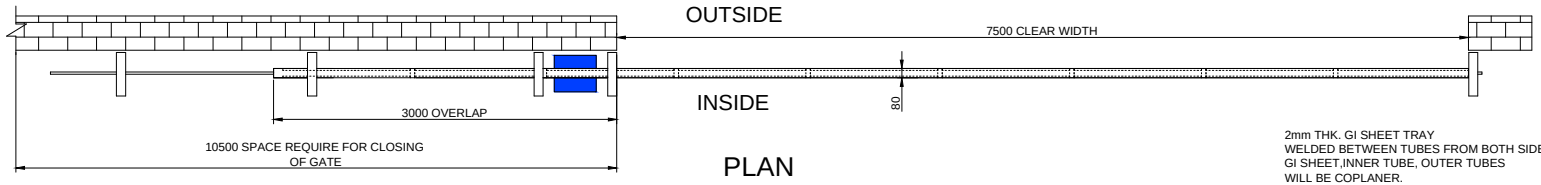

PLAN

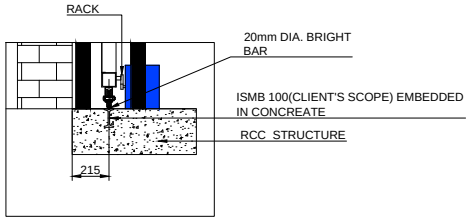

DETAILED VIEW OF A

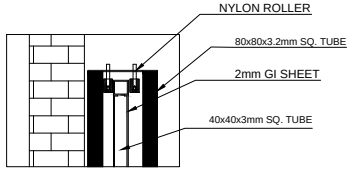

DETAILED VIEW OF B

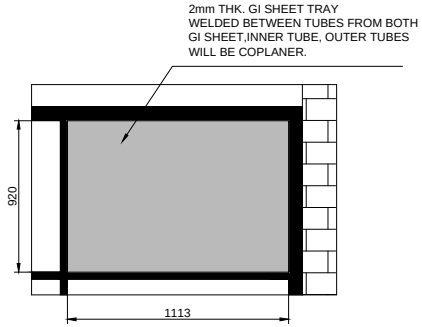

NOTE: NIHVA RECOMMENDS PERFORATION SHEET IN MIDDLE SECTION OF LEAF.

DIMENSION :

CLEAR WIDTH	CLEAR HEIGHT	QUANTITY
7500 mm	3000 mm	1 NOS.

MATERIAL :

THICKNESS :

NOTE: ALL REQUIRED CIVIL WORK WILL BE IN CLIENT'S SCOPE.
ISMB 100 WILL BE CLIENTS SCOPE.

NIHVA TECHNOLOGIES PVT. LTD.
NIHVA TECHNOLOGY PVT. LTD. PUNE
Email:- info@nihva.com
Website:- www.nihva.com

TITLE:

SINGLE LEAF SLIDING GATE

CLIENT'S APPROVAL :

CLIENT - WILO MATHER & PLATT PUMPS PVT. LTD.

PROJECT -

SITE LOCATION -

DWG. NO. : NIHVA/16-17/0072/R01

SCALE: NTS	WT:	SHEET:1 OF 1

DRAWN BY: OMKAR	DATE: 08-09-2016
CHECK : ANIL	DATE: 08-09-2016

If any queries contact : projects@nihva.com

NOTE: ALL DIMENSION ARE IN mm

THIS DRAWING & DESIGNING IS THE PROPERTY OF NIHVA TECHNOLOGIES. NOT BE SOLD OR COPY TO ANY OTHER CONCERN.