


PRODUCED BY AN AUTODESK EDUCATIONAL PRODUCT

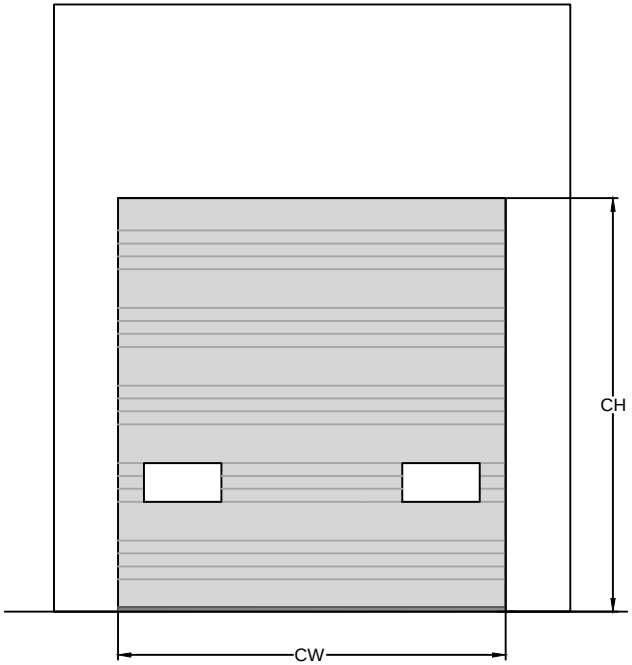


OUTSIDE ELEVATION

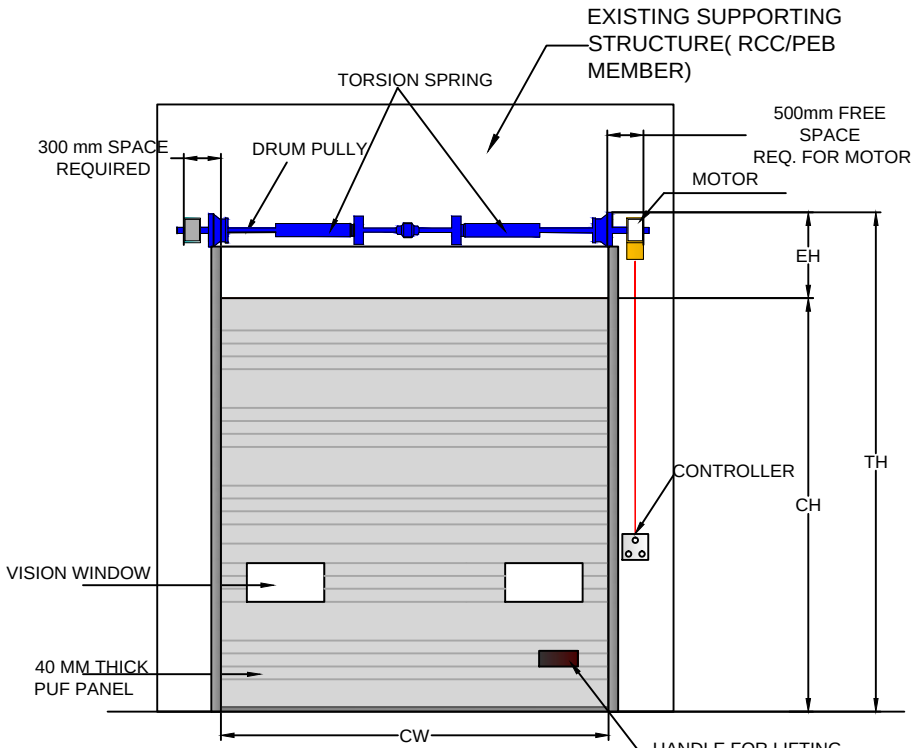

INSIDE ELEVATION

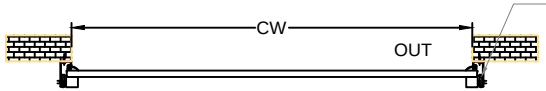

PLAN IN

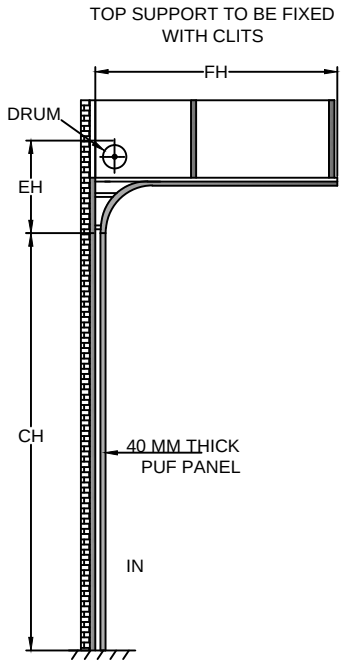

SIDE VIEW

COLORS -1. RAL 9010 (Pure White)
2. RAL 7016 (Anthracite Gray)
3. RAL 9006 (White Aluminum)

SR NO	CLEAR WIDTH (CW)	CLEAR HEIGHT (CH)	QUANTITY	EH	FH	TH	LOCATION
1	3000	3000	1	1000	3000	4000	
2	3000	3000	1	1000	3000	4000	
3	5000	4000	1	1000	4000	5000	
4	5000	5000	1	1000	5000	6000	
5	5000	5000	1	1000	5000	6000	
6	5000	5000	1	1000	5000	6000	
7	5000	5000	1	1000	5000	6000	

This drawing & design is the property of NIHVA TECHNOLOGIES. Not be sold or copy to any other concern.

TITLE: SECTIONAL DOOR (MOTORIZED)

NIHVA TECHNOLOGIES PVT. LTD.
NIHVA TECHNOLOGIES PVT. LTD. PUNE
Tel : 020 66304033
Email:- info@nihva.com
Website:- www.nihva.com

	SIGN	DATE
DRAWN	OMKAR	14/04/17
CHECK	SAGAR P.	14/04/17
REV.		
APPROVAL		

CLIENT - SCON PROJECTS
PROJECT - BEKAERT INDUSTRIES PVT. LTD.
SITE - RAJANGAON, MIDC
DWG. NO. : NIHVA/17-18/0015

If any queries contact : projects@nihva.com

SCALE: NTS | WT: | SHEET: 01 OF 01

ALL DIMENSION ARE IN mm

PRODUCED BY AN AUTODESK EDUCATIONAL PRODUCT

PRODUCED BY AN AUTODESK EDUCATIONAL PRODUCT