
LEGEND:-

9" WALL

4.5" WALL

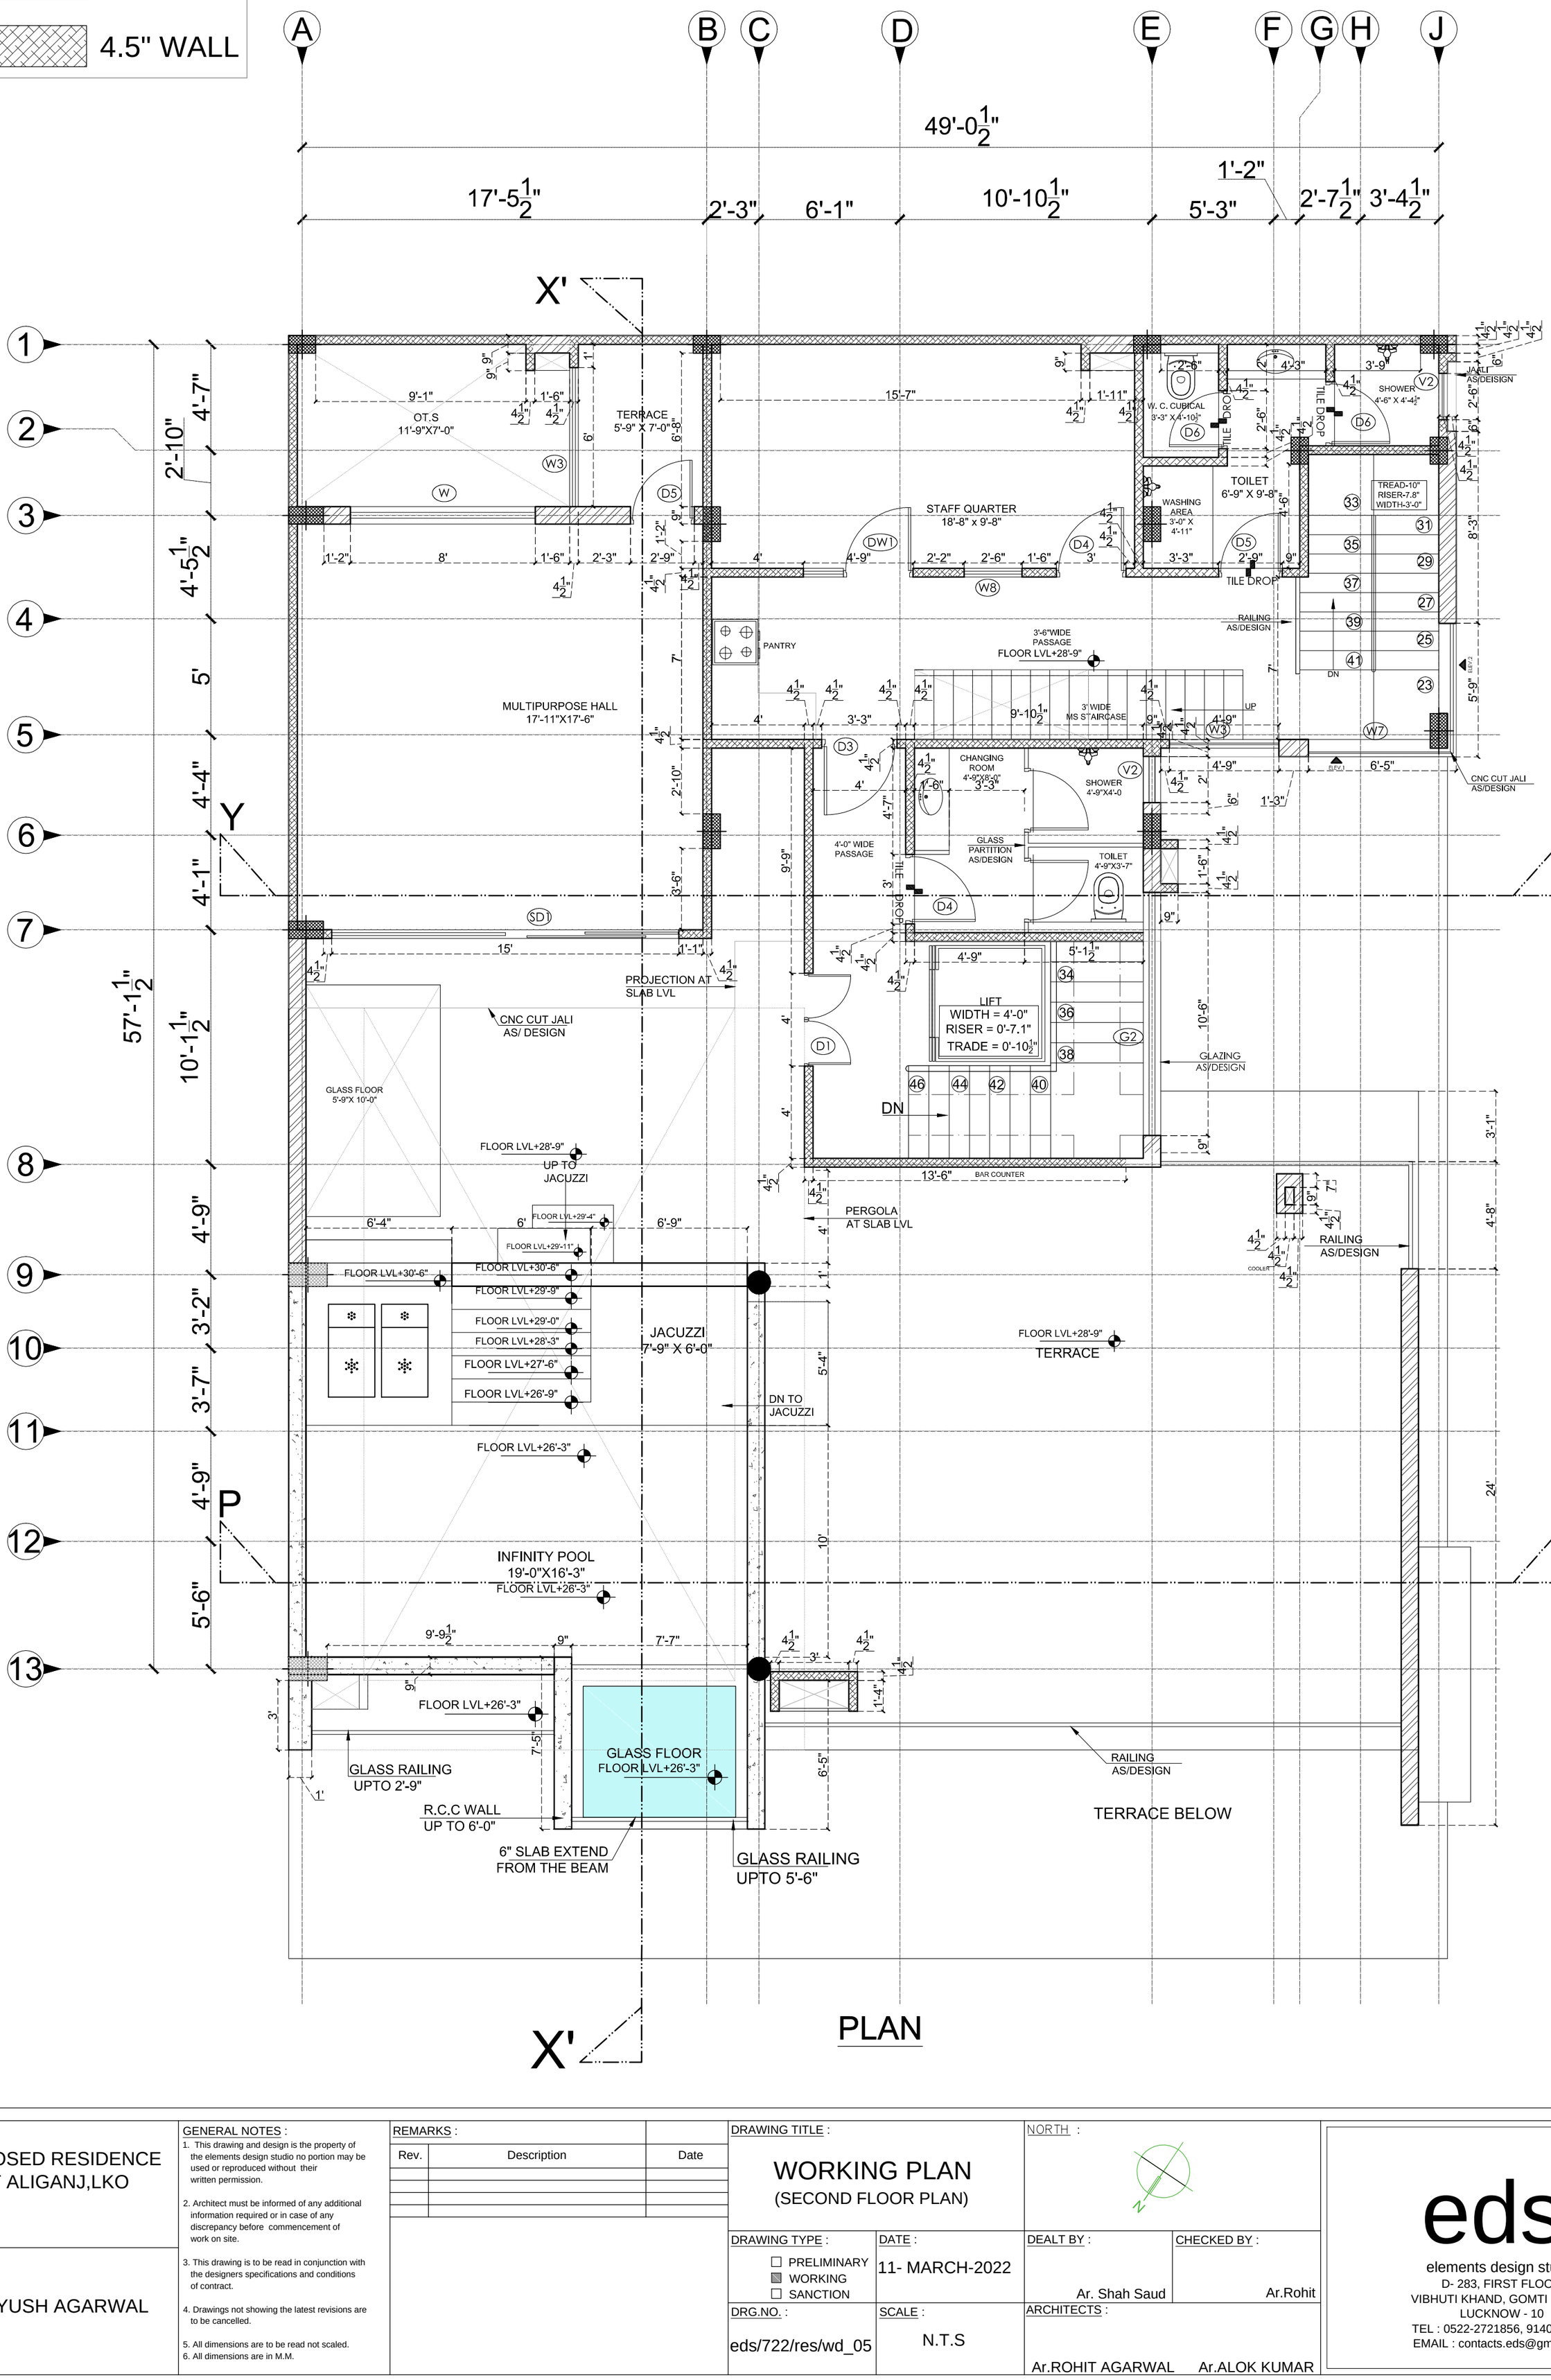

PLAN

PROJECT :

PROPOSED RESIDENCE AT ALIGANJ,LKO

CLIENT :

MR. PIYUSH AGARWAL

GENERAL NOTES :

1. This drawing and design is the property of the elements design studio no portion may be used or reproduced without their written permission.
2. Architect must be informed of any additional information required or in case of any discrepancy before commencement of work on site.
3. This drawing is to be read in conjunction with the designers specifications and conditions of contract.
4. Drawings not showing the latest revisions are to be cancelled.
5. All dimensions are to be read not scaled.
6. All dimensions are in M.M.

REMARKS :

Rev.	Description	Date

DRAWING TITLE :

WORKING PLAN
(SECOND FLOOR PLAN)

NORTH :

DRAWING TYPE :

- ☐ PRELIMINARY
- ▨ WORKING
- ☐ SANCTION

DATE :

11- MARCH-2022

DEALT BY :

Ar. Shah Saud

CHECKED BY :

Ar.Rohit

DRG.NO. :

eds/722/res/wd_05

SCALE :

N.T.S

ARCHITECTS :

Ar.ROHIT AGARWAL Ar.ALOK KUMAR

eds.

elements design studio
D- 283, FIRST FLOOR
VIBHUTI KHAND, GOMTI NAGAR
LUCKNOW - 10
TEL : 0522-2721856, 9140512183
EMAIL : contacts.eds@gmail.com