

ESPIC Commented
06/Nov/2014

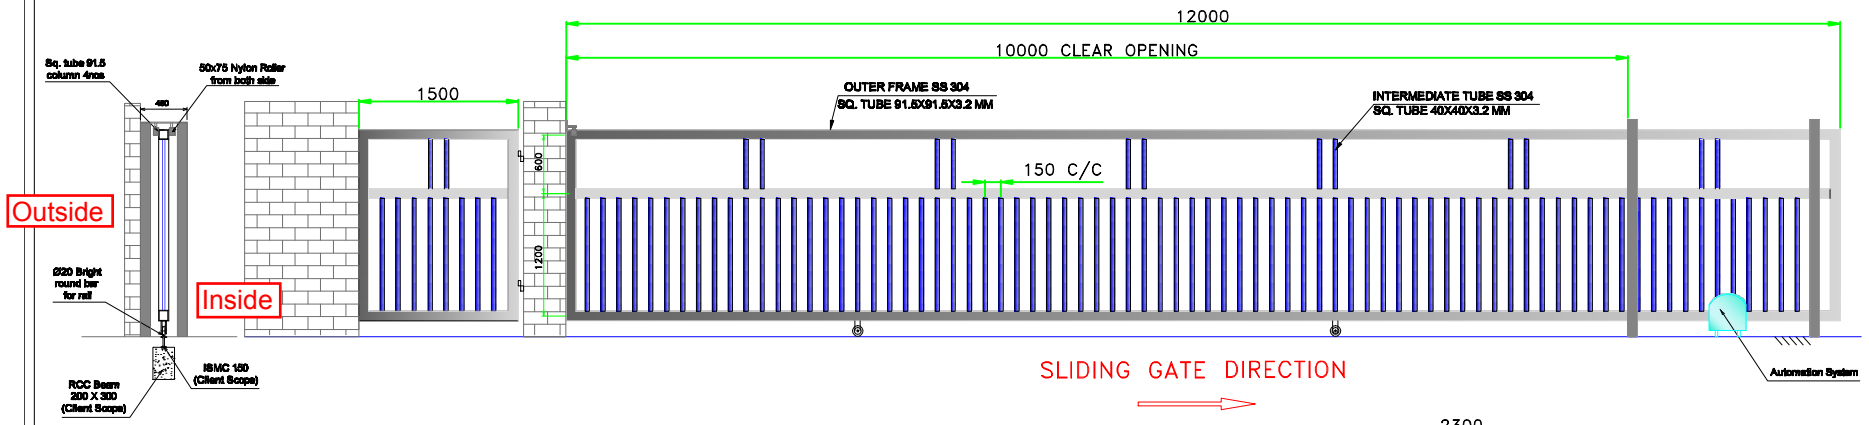

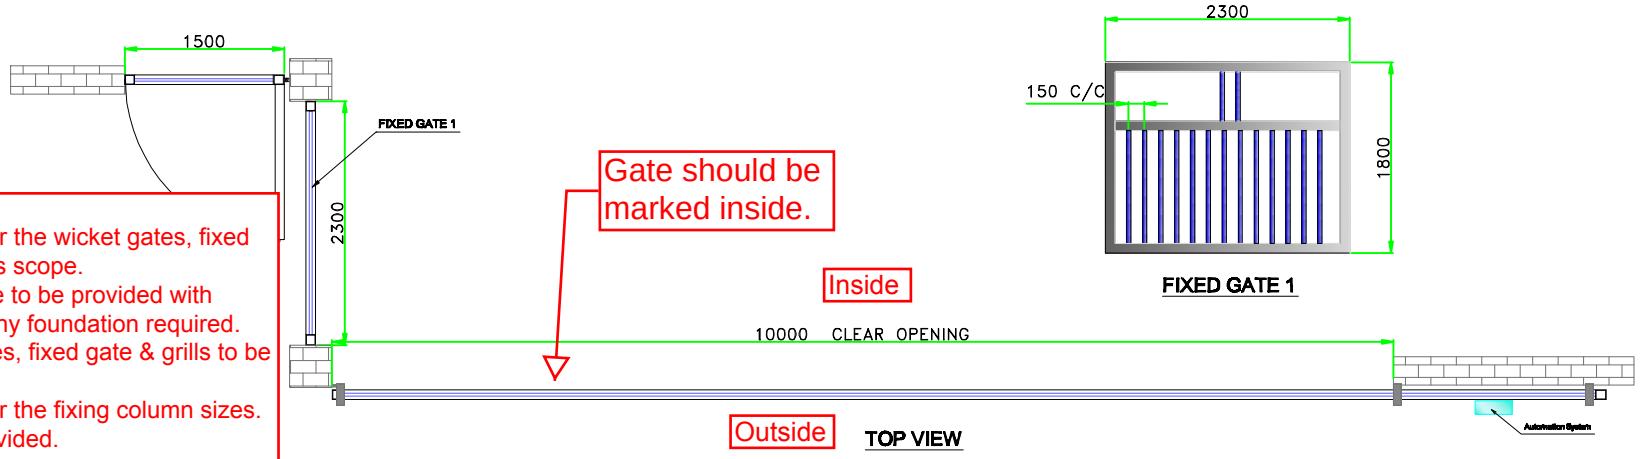

Common For All Drawings:-
1.) Fixing arrangement / clamps for the wicket gates, fixed gate and grills shall be in supplier's scope.
2.) Fixing details of the sliding gate to be provided with details of the vertical support for any foundation required.
3.) Fixing details of the wicket gates, fixed gate & grills to be provided.
4.) Size may slightly change as per the fixing column sizes.
5.) Weight of each items to be provided.

SLIDING GATE SIZE = 12000 (W) X 1800 (H), QTY = 1NOS..
CLEAR OPENING = 10,000 (W) X 1800 (H)
WICKET GATE SIZE = 1500(W) X 1800 (H), QTY = 1NOS.
FIXED GATE SIZE = 2300(W) X 1800(H), QTY = 1NOS.
OUTER FRAME = 91.5 X 91.5 X 3.2 mm
INNER FRAME = 40 X 40 X 2 mm
GAP B/W FRAME = 150 c/c
MATERIAL = SS 304
C' COLUMN VERTICAL SUPPORT = 4 NOS.

40X40X3.2 mm

This drawing & designing is the property of NIHVA TECHNOLOGIES. Not be sold or copy to any other concern.

TITLE: SLIDING GATE	ALL DIMENSION ARE IN mm		NIHVA TECHNOLOGIES PVT. LTD. / NIHVA TECHNOLOGY PVT. LTD. PUNE Tel : 020 66304033 Email:- info@nihva.com Website:- www.nihva.com
	SIGN	DATE	
DRAWN	ABHIJIT	05/11/14	CLIENT - JSW
CHECK	ANIL	05/11/14	PROJECT -
REV.	02		SITE - KHED
APPRD.			DWG. NO. - NVA/JSW/D1/1 of 3
MFG			SCALE: 01 / WT: / SHEET: 0101
Ref. No.			If any queries contact : projects@nihva.com

CLIENT APPROVAL