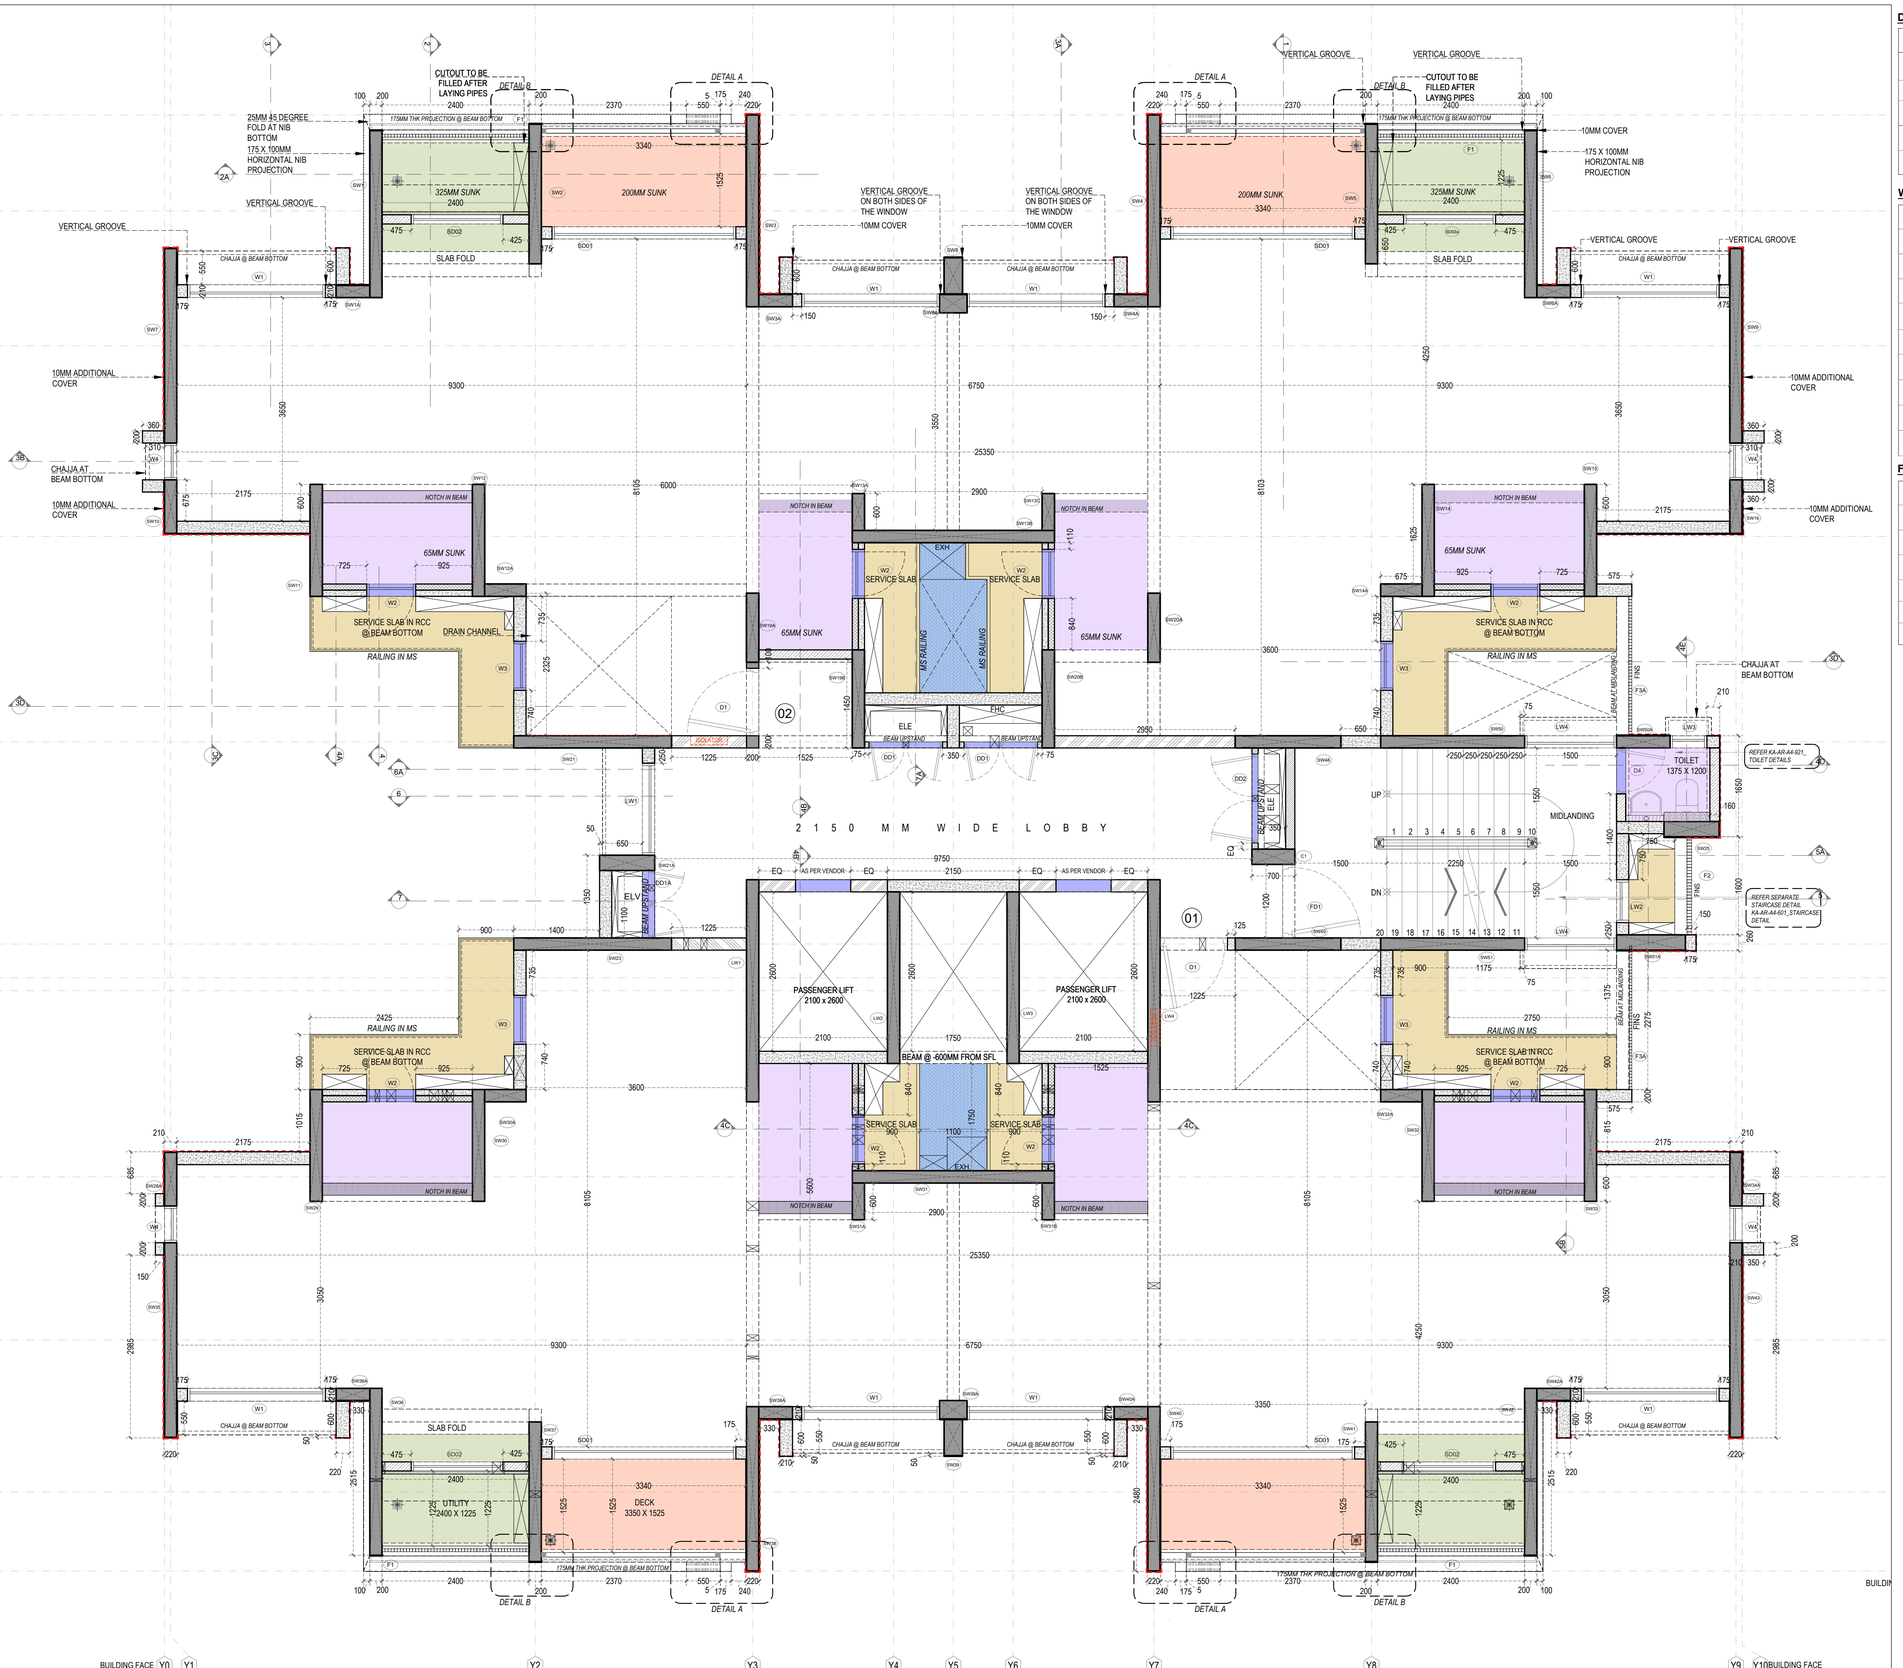


DOOR SCHEDULE FOR PENTHOUSE

NO.	LOCATION	WIDTH (CIVIL OPENING)	LINTEL (FRM SFL)	CILL (FRM SFL)	DESCRIPTION
D1	FLAT ENTRY	1100	2400	-	SINGLE LEAF FIRE RATED WOODEN FLUSH DOOR
D4	MIDLANDING TOILET	750	2250	-	SINGLE LEAF WOODEN FLUSH DOOR
FD1	STAIRCASE	1200	2400	-	SINGLE LEAF FIRE RATED METAL DOOR (DETAIL AS PER VENDOR)
DD1	F.H.C/ ELE SHAFTS	1200X1975 (W X H)	2400	425 (UPTEND BEAM)	DOUBLE LEAF FIRE RATED METAL DOOR (DETAIL AS PER VENDOR)
DD1A	ELV SHAFT	1100X1975 (W X H)	2400	425 (UPTEND BEAM)	DOUBLE LEAF FIRE RATED METAL DOOR (DETAIL AS PER VENDOR)

WINDOW SCHEDULE

NO.	LOCATION	CIVIL OPENING (W X H)	LINTEL (FRM SFL)	CILL (FRM SFL)	DESCRIPTION
SD01	LIVING ROOM	3050X2400	2400	-	3 TRACK ALUMINUM SLIDING WINDOW WITH LAMINATED GLASS
SD02	KITCHEN	1500X2400	2400	-	3 TRACK ALUMINUM SLIDING WINDOW WITH LAMINATED GLASS
W1	BEDROOM	2250X2275	2400	125	2 TRACK ALUMINUM SLIDING WINDOW WITH BOTTOM FIXED IN LAMINATED GLASS
W2	TOILET	800X1050	2250	1200	SINGLE LEAF OPENABLE GLASS PANEL WINDOW
W3	BEDROOM 3	800X2125	2250	125	SINGLE LEAF OPENABLE GLASS PANEL WINDOW
W4	MASTER BEDROOM	600X1200	2400	1200	SINGLE LEAF OPENABLE GLASS PANEL WINDOW
LW1	LOBBY WINDOW	1500 X1200	2400	1200	2 TRACK ALUMINUM SLIDING WINDOW
LW2	STAIRCASE WINDOW	700 X1200	2400 (FROM MID.AXIS)	1200 (FROM MID.AXIS)	2 TRACK ALUMINUM SLIDING WINDOW
LW3	STAIRCASE TOILET	600X1200	2400 (FROM MID.AXIS)	1200 (FROM MID.AXIS)	SINGLE LEAF OPENABLE GLASS PANEL WINDOW


FINS SCHEDULE

NO.	LOCATION	CIVIL OPENING (W X H)	DESCRIPTION
F1	UTILITY	2400X2275	FINS AS PER DETAIL
F2	STAIRCASE TOILET SHAFT	1590X2985	FINS AS PER DETAIL
F3	SERVICE AREAS	2265X2985	FINS AS PER DETAIL
F4	SERVICE AREAS	2265X2985	FINS AS PER DETAIL
F5	SERVICE AREAS	1200X1150	FINS AS PER DETAIL
F6	SERVICE AREAS	1200X1150	FINS AS PER DETAIL

LEGEND - SUNK	
SUNK DEPTH	HATCH
200 MM	
300 MM	
65 MM	
450 MM	

LEGEND	
TYPE	HATCH
DRIP MOULD	
GROOVES AT BEAM BOTTOM	
VERTICAL GROOVES	
SLEEVES @ SLAB	
SLEEVES @ CEILING	

WALL & SUNK HATCH SCHEDULE
R.C.C WALL & COLUMN
200 MM NON STRUCTURAL WALL
150 MM NON STRUCTURAL WALL
200 MM BLOCK WORK
100 MM BLOCK WORK
150 MM LEDGE WALL IN BLOCKWORK
100 MM LEDGE WALL IN BLOCKWORK
METAL GRATING SERVICE SLAB
RCC SERVICE SLAB

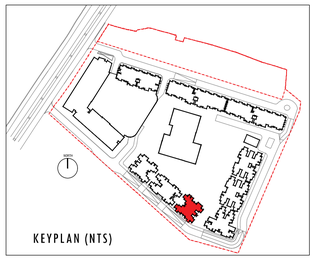

GENERAL NOTES

1 : All dimensions are in millimeters and levels in meters unless specified otherwise.
2 : Do not scale the drawing; follow written dimensions.
3 : All dimensions are unfinished dimensions unless specified otherwise.
4 : Any discrepancies should be brought to the notice of the Architect prior to execution of job / procuring materials at site.
5 : This drawing is the property of Kapadia Associates and should not be reproduced, copied, handed over to a third party or used for any purpose other than for which it has been issued.
6 : This drawing is to be read in conjunction with all relevant structural & services drawings.

NOTE:

1. PLEASE READ IN CONJUNCTION WITH KITCHEN DETAIL,TOILET DETAIL, FIN DETAIL & RAILING DETAIL, STARICASE DETAILS.
2. 10MM ADDITIONAL COVER HAS BEEN INCLUDED IN THE SHEAR WALL THICKNESS, WHEREVER REQUIRED FOR GROOVE.

REVISION INDEX

REV. NO.	DATE	REMARKS
R00	30-06-2026	VFC ISSUED

CLIENT

LODHA GROUP

PROJECT TITLE

LODHA RISERVO - A4

VIKHROLI,MUMBAI

DRAWING TITLE & NO.

AR-KA-A4-210-PENTHOUSE FLOOR PLAN

DRAWING STAGE

WORKING DRAWING

SCALE	REV. NO.	REV. DATE
1:50	R00	30-06-2026

STAMP & SIGNATURE

Jagadishponraj Nadar

Digitally signed by: Jagadishponraj Nadar
DN: CN = Jagadishponraj Nadar OU = Lodha Users
Date: 2026.07.01 16:07:04 +06'30'

Vaibhav Shimpi

Digitally signed by Vaibhav Shimpi
DN: CN = Vaibhav Shimpi OU = Lodha Users
Date: 2026.07.01 16:08:33 +06'30'

Digitally signed by: SUPRIYA UKIDAVE
Date: 2026.07.01 11:57:11 +06'30'

KAPADIA ASSOCIATES
architecture • urban design
112-114, Peninsula Centre,Dr. S.S. Rao Road,Parel East, Mumbai 400012
Tel : 91-22-6660 2638 / 39 E-mail : kapl@kapl.in Website : www.kapl.in