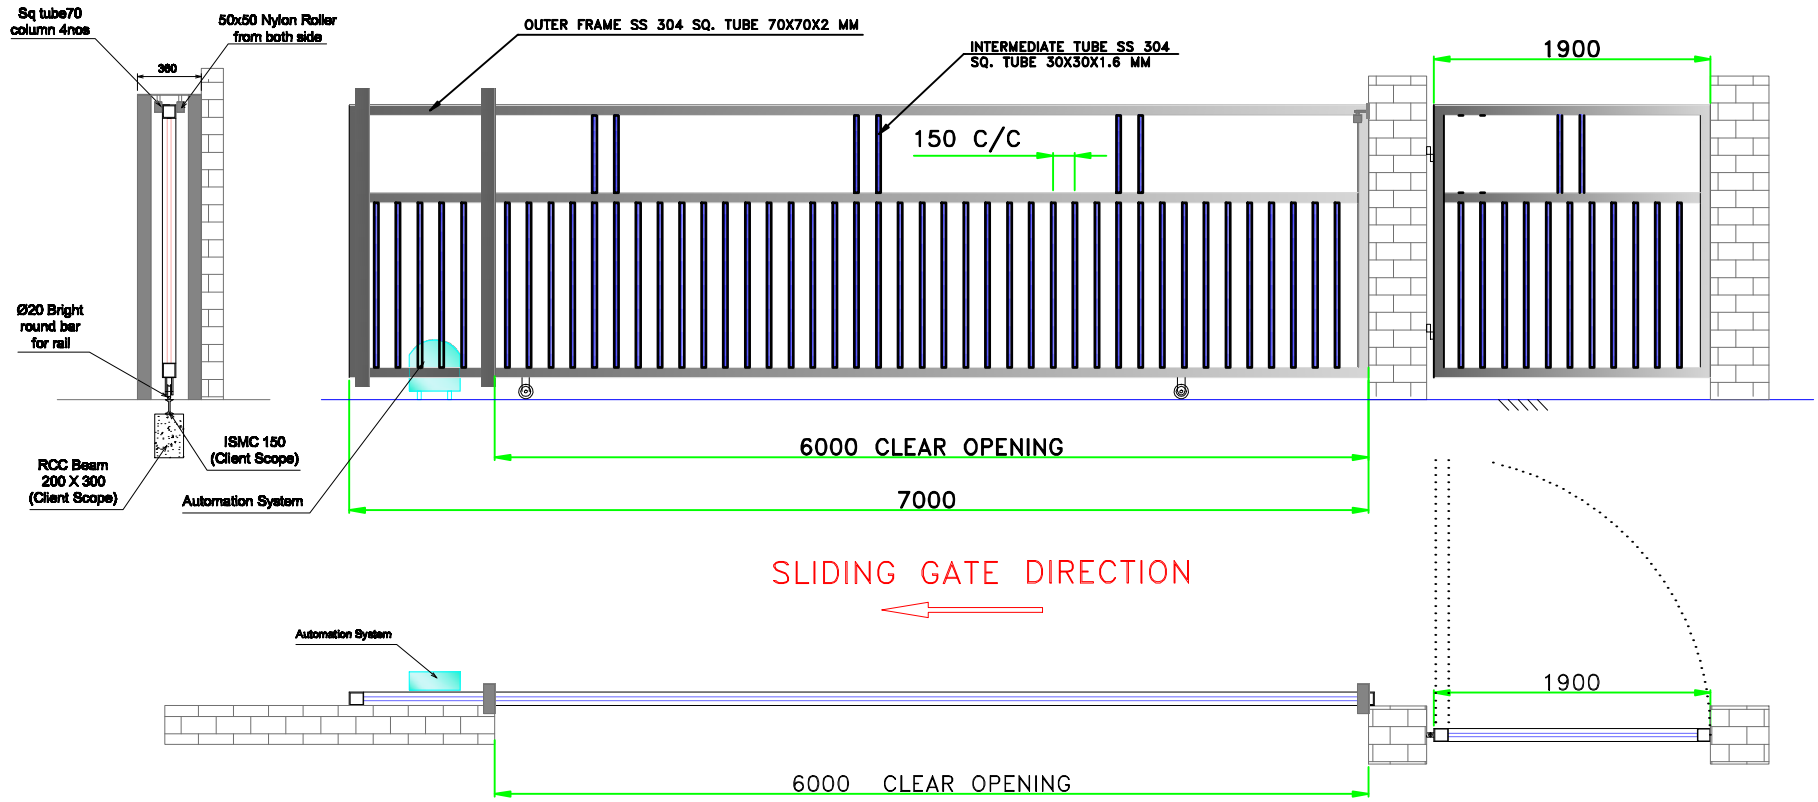


SLIDING GATE SIZE = 7000 (W) X 1800 (H), QTY = 1NOS.
CLEAR OPENING = 6,000 (W) X 1800 (H)
WICKET GATE SIZE = 1900(W) X 1800 (H), QTY = 1NOS.
OUTER FRAME = 70 X 70 X 2 mm
INNER FRAME = 30 X 30 X 1.6 mm
GAP B/W FRAME = 150 c/c
MATERIAL = SS 304
C' COLUMN VERTICAL SUPPORT = 4 NOS.
ALL DIMENSIONS ARE IN MM

This drawing & designing is the property of NIHVA TECHNOLOGIES. Not be sold or copy to any other concern.

TITLE	ALL DIMENSION ARE IN mm			NIHVA TECHNOLOGY PVT. LTD. PUNE
SLIDING GATE		SIGN	DATE	NIHVA TECHNOLOGIES PVT. LTD. Tel : 020 66304033 Email:- info@nihva.com Website:- www.nihva.com
CLIENT APPROVAL	DRAWN	ABHIJIT	05/11/14	CLIENT - JSW
	CHECK	ANIL	05/11/14	PROJECT -
	REV.	02		SITE - KHED
	APPRD.			DWG. NO. - NVA/JSW/D1/ 2 of 3
	MFG			SCALE: 01 | WT: | SHEET: 0101
	Ref. No.			If any queries contact : projects@nihva.com