

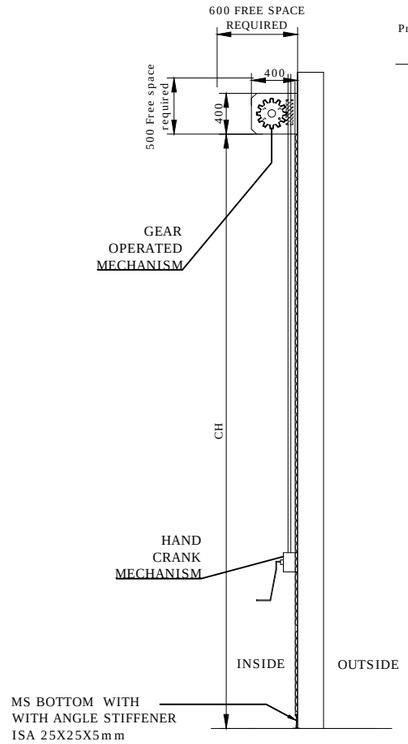



SIDE VIEW

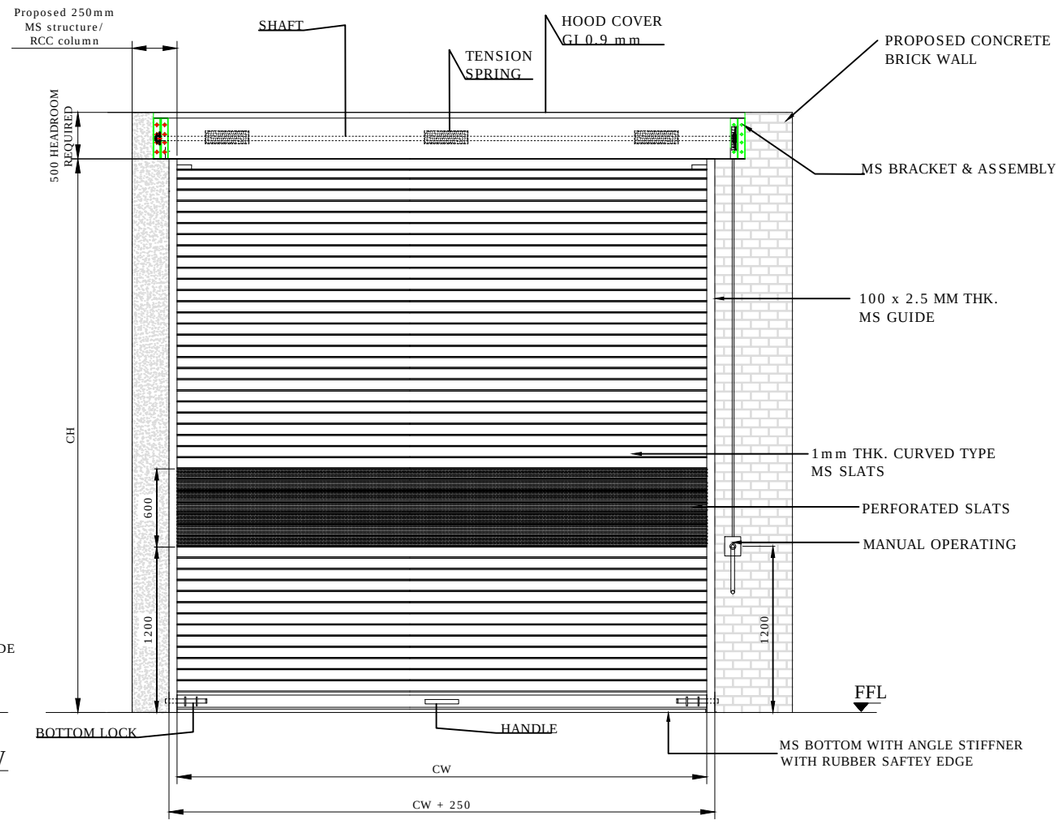


INSIDE ELEVATION

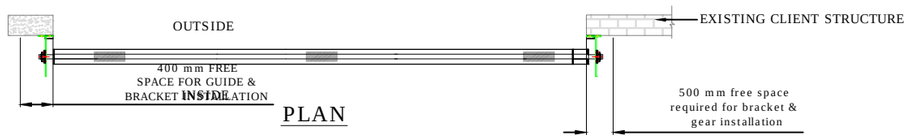

PLAN

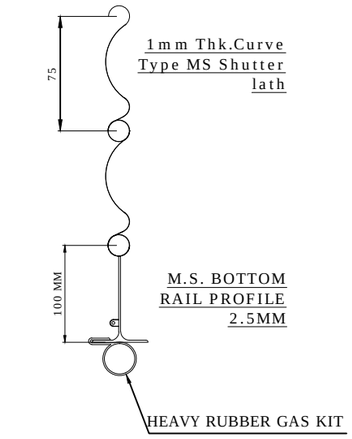

M.S. BOTTOM RAIL PROFILE 2.5MM

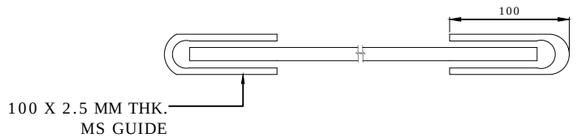

NOTE-
1. ALL CIVIL WORK WILL BE CLIENT'S SCOPE.
2.IF STRUCTURE REQUIRED FOR SHUTTER IS IN CLIENT'S SCOPE.
3. MOUNTING LOCATION: INSIDE AREA
4. MOUNTING SURFACE ON CONCRETE BRICK WALL.

REV 01- (14/02/2022)
1. ADDED APPROVED RAL COLOR.
2. MENTIONED MOUNTING OF SHUTTER ON BRICK WALL.
3. MENTIONED MOUNTING LOCATION INSIDE.
4. BOTTOM BRACKET SIZE CHANGED TO 100 MM.

REV 02- (23/02/2022)
1. CLEAR OPENING SIZES REDUCED FOR SHUTTER 1.
CW- 3600 & CH-3600.
2. MOUNTING FOR LEFT GUIDE WILL BE STRUCTURE/ RCC COLUMN.
3. HEADROOM REDUCED TO 500MM FROM 650MM.

REV 03- (08/03/2022)
1. CLEAR OPENING SIZES REDUCED FOR SHUTTER 1-
(3750 x 3600) AND SHUTTER 2- (3750 x 3300)

SR NO	(CW) CLEAR WIDTH	(CH) CLEAR HEIGHT	QUANTITY
2	3750	3300	01 NO
1	3750	3600	01 NO

RAL 9007	GREY AL.
RAL 9010	PURE WHITE
RAL 9002	GREY WHITE
RAL 7035	LIGHT GREY
RAL 5002	ULT. M. BLUE
RAL CODE	RAL COLOR

APPROVED

TOLERANCE - ±10mm

This drawing & design is the property of NIHVA TECHNOLOGIES. Not to be sold or copied to any other concern.

TITLE
GEAR OPERATED ROLLING SHUTTER

	NAME	SIGN	DATE
DRAWN	G.I.P		17.01.2022
CHECK	A.K.		17.01.2022
APPRD.			

If any queries contact : design@nihva.com

ALL DIMENSION ARE IN mm

NIHVA
NIHVA TECHNOLOGIES PVT. LTD.
Website:- www.nihva.com

NIHVA TECHNOLOGIES PVT. LTD. PUNE
Tel : 020 66304033
Email:- info@nihva.com

CLIENT -SCON PROJECTS
PROJECT - ROLLING SHUTTER
SITE LOCATION - NASHIK
DWG. NO. : NIHVA/21-22/CLT/0313 REV- R03
SCALE: NTS WT: SHEET: 01 OF 01