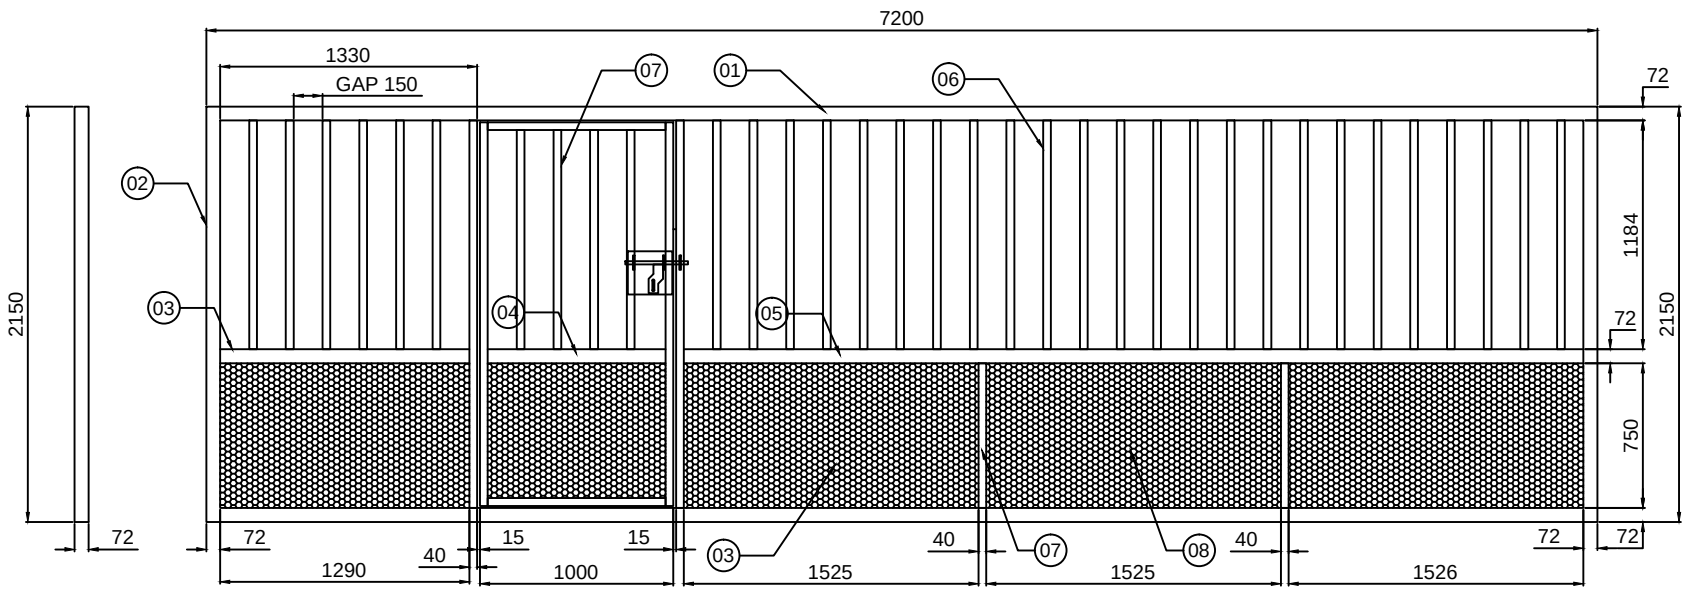


SR NO	DESCRIPTION	SPECIFICATION	QTY
09	RACK	MODULE 4, 12X30mm	7 MTR
08	PERFORATED SHEET	AS PER DRAWING	5 NOS
07	SQ. TUBE	40 X 40 X 2.5 THK X 750L	2 NOS
06	SQ. TUBE	40 X 40 X 2.5 THK X 1184L	30 NOS
05	SQ. TUBE	72 X 72 X 2.5 THK X 4655L	1 NO
04	SQ. TUBE	72 X 72 X 2.5 THK X 920L	1 NO
03	SQ. TUBE	72 X 72 X 2.5 THK X 1290L	1 NO
02	SQ. TUBE	72 X 72 X 2.5 THK X 2150L	2 NOS
01	SQ. TUBE	72 X 72 X 2.5 THK X 7200L	2 NOS

This drawing & design is the property of NIHVA TECHNOLOGIES. Not to be sold or copied to any other concern.

TITLE: MAIN LEAF

NIHVA TECHNOLOGIES PVT. LTD.
NIHVA TECHNOLOGIES PVT. LTD. PUNE
Tel : 020 66304033
Email:- info@nihva.com
Website:- www.nihva.com

	NAME	SIGN	DATE
DRAWN	P.V.A		27.02.19
CHECK	V.M.T		27.02.19
APPRD.			

If any queries contact : design@nihva.com

ALL DIMENSION ARE IN mm

CLIENT -

PROJECT -

SITE LOCATION -

DWG. NO. : NIHVA/18-19/VDR/38 4

SCALE: NTS | WT: | REV- 00