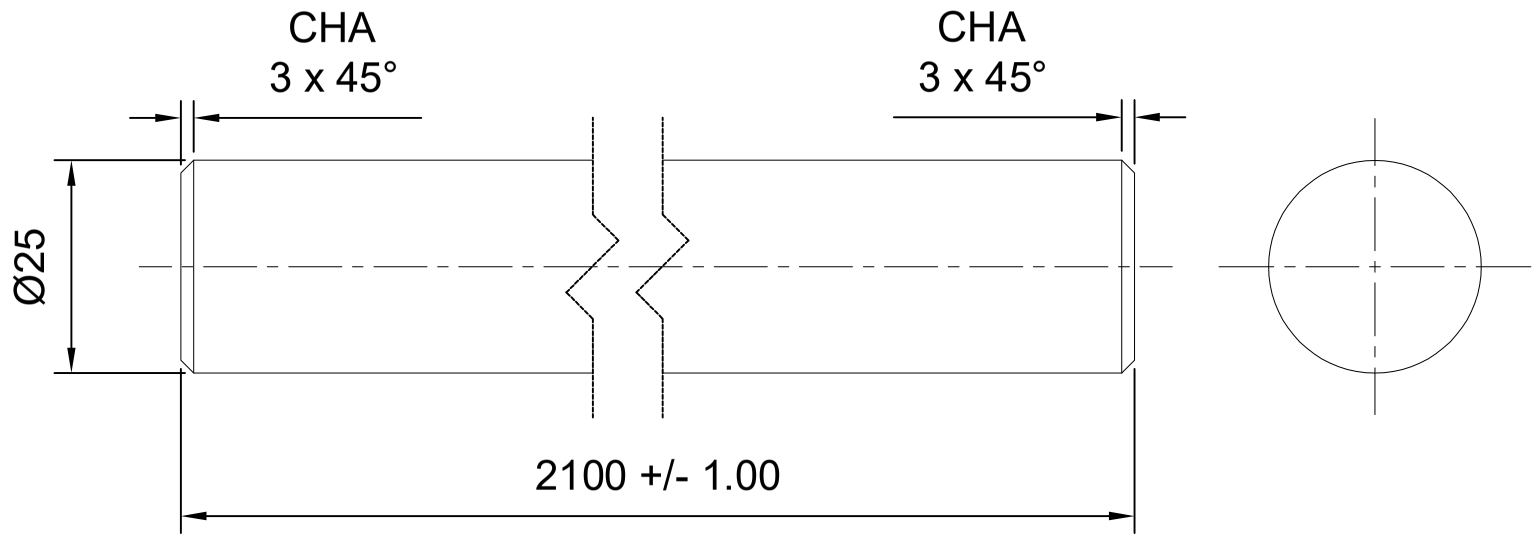


NOTE:~ MTL : EN8

LIP PIN Ø25 X 2100L = 2 NO

#. IF CHAMFER IS NOT POSSIBLE THEN PIN WILL BE GRINDING AT BOTH ENDS.

This drawing & design is the property of NIHVA TECHNOLOGIES. Not to be sold or copied to any other concern.

TITLE				NIHVA TECHNOLOGIES PVT. LTD. PUNE Tel : 020 66304033 Email:- info@nihva.com Website:- www.nihva.com	
LIP PIN					
	NAME	DATE	SIGN		
DRAWN	SUJATA	22/04/2022		CLIENT - NIHVA TECHNOLOGIES	
CHECK	M.SUTAR	22/04/2022		PROJECT -DOCK LEVELER	
APPRD.				SITE LOCATION -PUNE	
If any queries contact : design@nihva.com				DWG. NO. : NIHVA/22-23/VDR/0009	
ALL DIMENSION ARE IN mm				SCALE: NTS	WT: REV- 0