


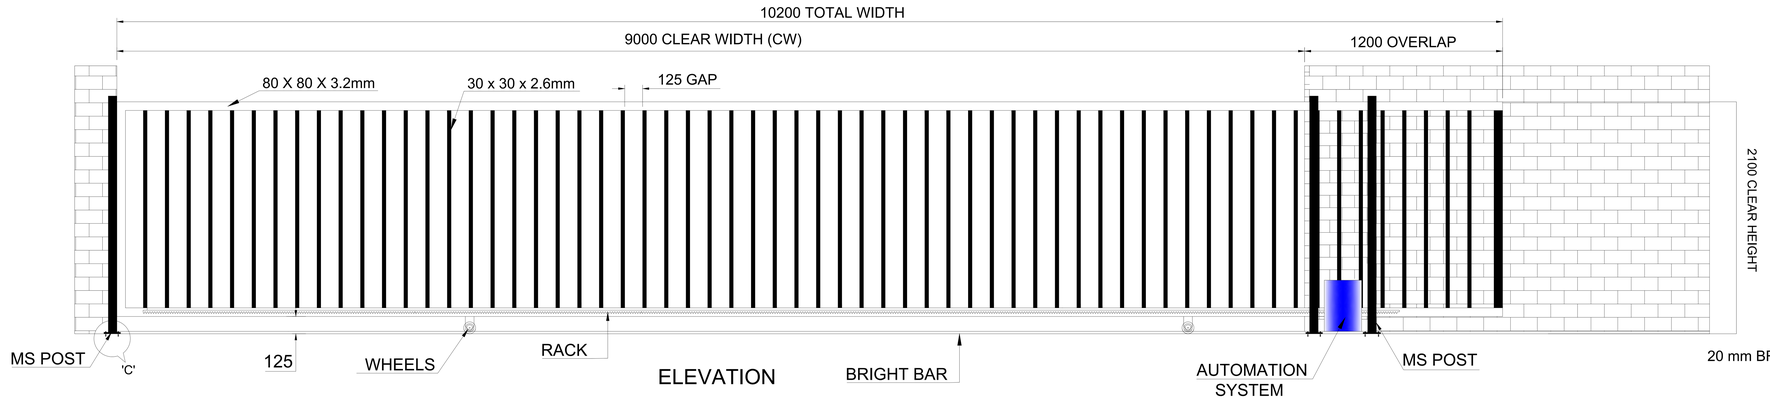


ELEVATION

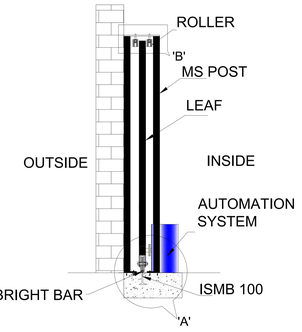


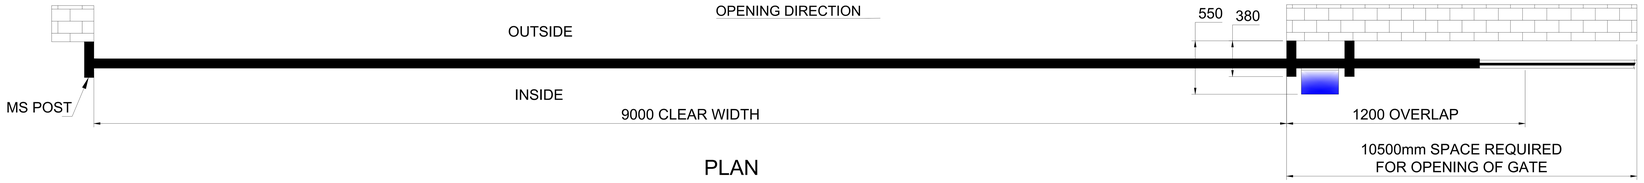

PLAN

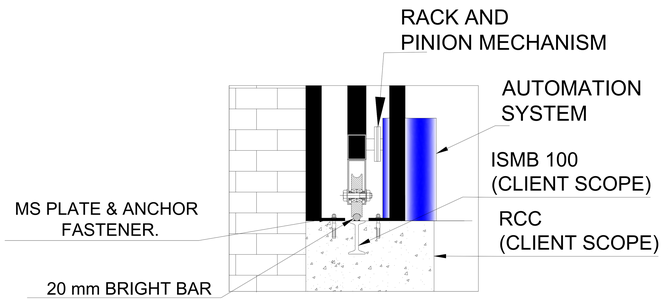

DETAIL VIEW OF A

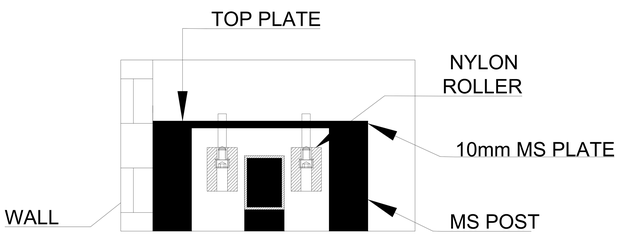

DETAIL VIEW OF B

NOTE-
1. ALL REQUIRED CIVIL WORK WILL BE IN CLIENTS SCOPE.
2.IN NECESSARY GATE LEAF WILL BE IN TWO OR THREE PARTS FOR TRANSPORTATION AND WILL BE WELDED TOGETHER ON SITE.

9000 mm	1800 mm	1 NO
CLEAR WIDTH	CLEAR HEIGHT	QUANTITY

SR.NO	RAL CODE	RAL COLOR
04	RAL 7035	LIGHT GREY
03	RAL 5002	ULTRAMARINE BLUE
02	RAL 9002	GREY WHITE
01	RAL 1004	GOLDEN YELLOW

TOLERANCE ± 10 MM.

This drawing & design is the property of NIHVA TECHNOLOGIES. Not to be sold or copied to any other concern.

TITLE
AUTOMATIC SLIDING GATE

NIHVA TECHNOLOGIES PVT. LTD.

NIHVA TECHNOLOGIES PVT. LTD. PUNE
Tel : 020 66304033
Email:- info@nihva.com
Website:- www.nihva.com

	NAME	SIGN	DATE
DRAWN	P.A		08.09.2020
CHECK	G.J		08.09.2020
APPRD.			

CLIENT - HIRANANDANI
PROJECT - VESTAS
SITE LOCATION - CHENNAI

If any queries contact : design@nihva.com
DWG. NO. : NIHVA/20-21/0052
REV- 0
ALL DIMENSION ARE IN mm
SCALE: NTS
WT:
SHEET: 01 OF 01