



General drawing Rapid Protect RP300

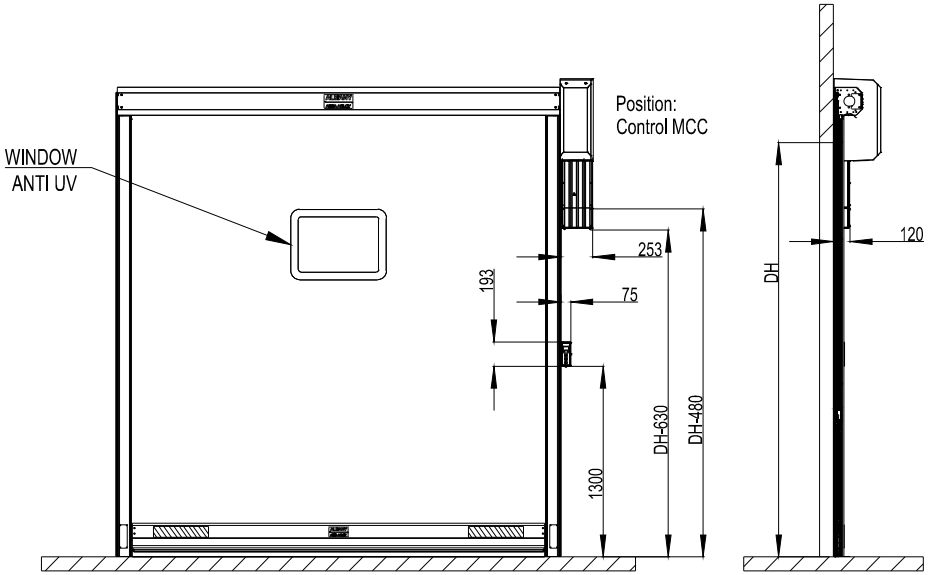

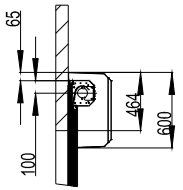

with cover

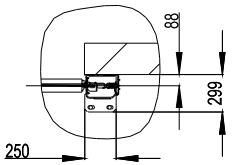

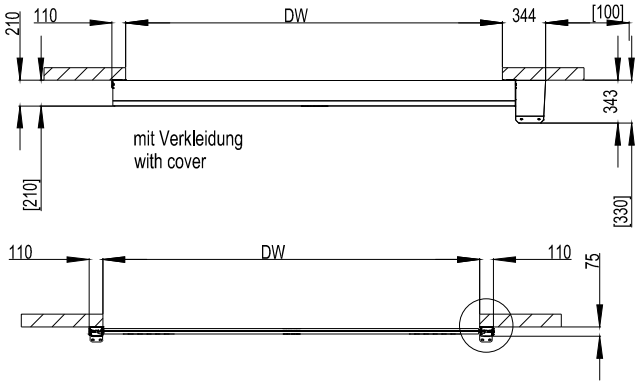

ROLTEX PLUS CURTAIN WITH RAL BLUE 5002

4000	2500	2 NOS	M.S. STRUCTURE	R.H.
CLEAR OPENING WIDTH	CLEAR OPENING HEIGHT	QTY	MOUNTING SURFACE	MOTOR

NOTES-

1. REQUIRED M.S. STRUCTURE , FITTING & ALL CIVIL WORK IS IN CLIENT SCOPE .

This drawing & design is the property of NIHVA TECHNOLOGIES. Not to be sold or copied to any other concern.

TITLE ASSA ABLOY RP 300			NIHVA TECHNOLOGIES PVT. LTD.
	NAME	SIGN	DATE
DRAWN	S.M.S.		17.2.2021
CHECK	S.M.S.		17.2.2021
APPRD.			
If any queries contact : projectsupport@nihva.com			
ALL DIMENSION ARE IN mm			

NIHVA TECHNOLOGIES PVT. LTD. PUNE
Tel : 020 66304033
Email:- info@nihva.com
Website:- www.nihva.com

CLIENT - ABB INDIA LIMITED			
PROJECT -			
SITE LOCATION - PEENYA , BENGLARU			
DWG. NO. : NIHVA/20-21/0162			REV- R00
SCALE: NTS	WT:	SHEET: 1 OF 2	