



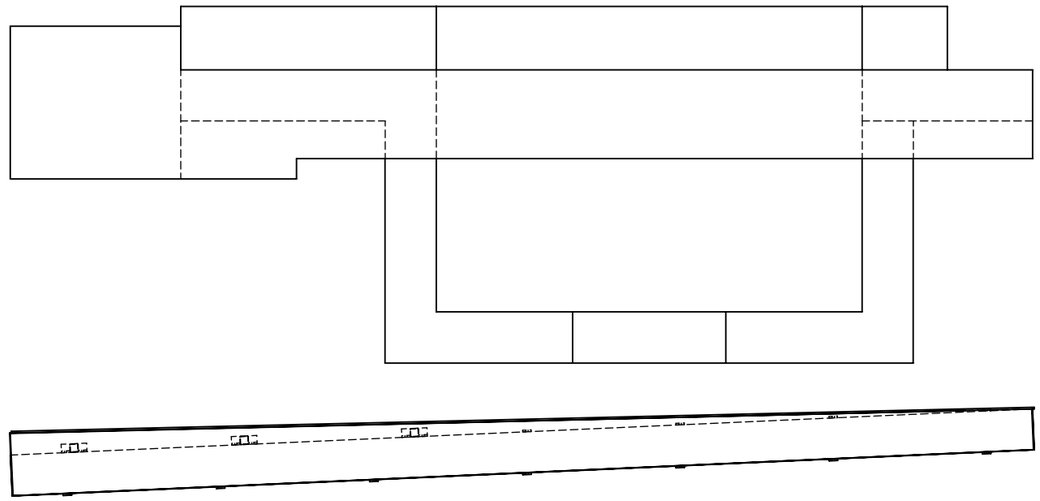


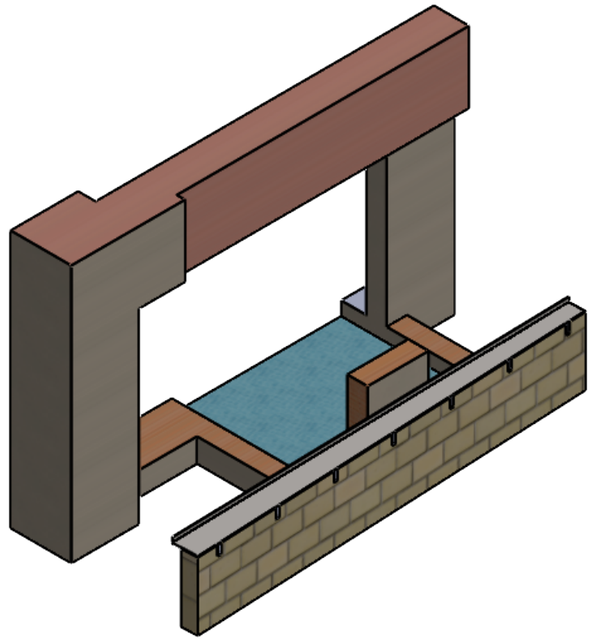


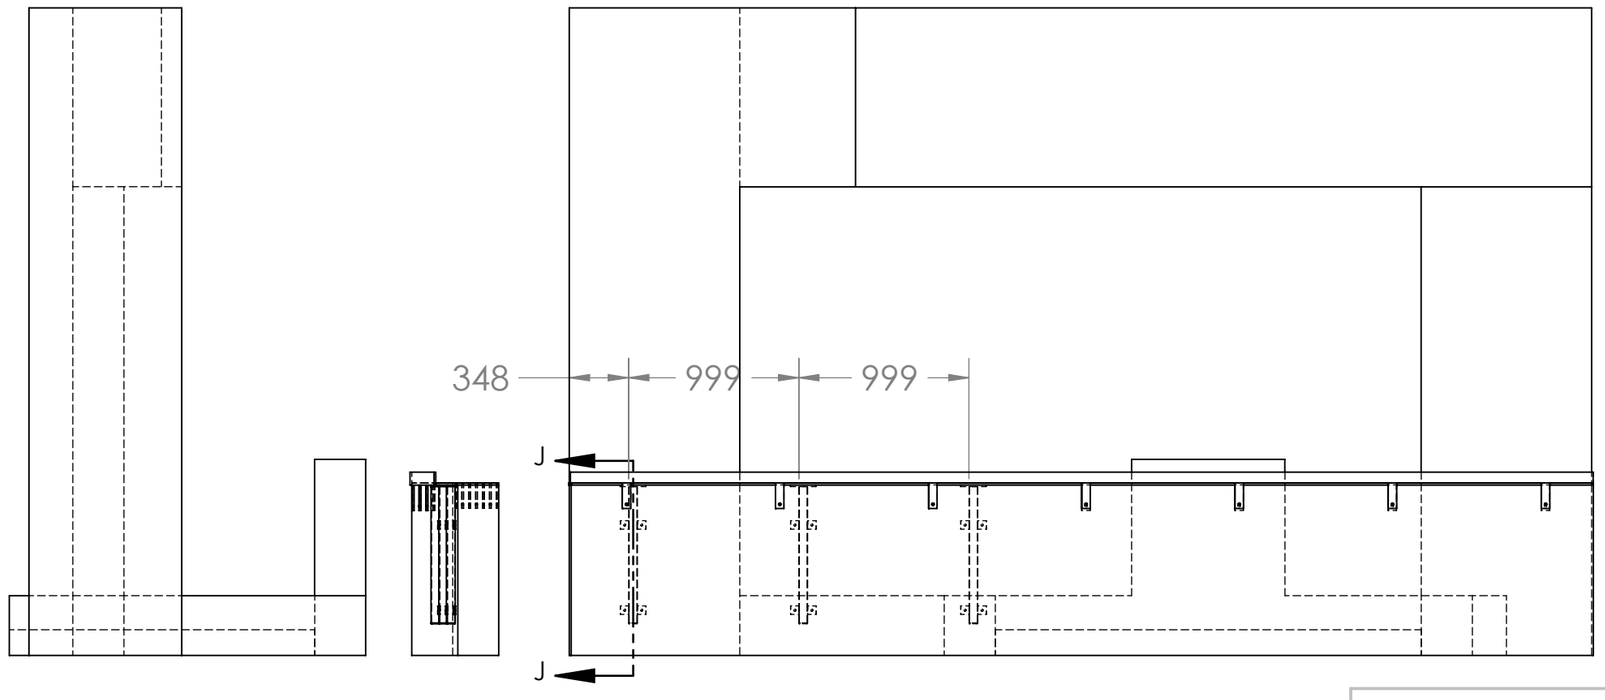

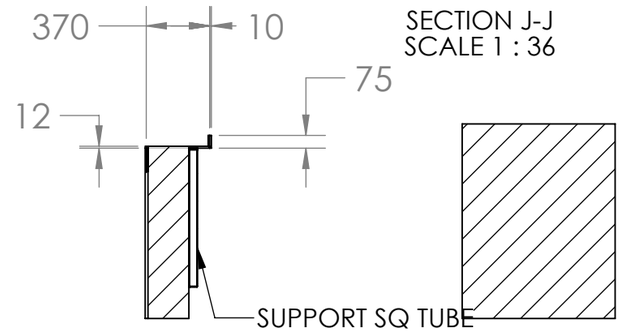


TITLE - PANEL NO - 03				NIHVA TECHNOLOGIES PVT.LTD.PUNE Website - www.nihva.com
DWG NO - NTPL234-PANEL03			QTY - 1	
	NAME	SIGNATURE	DATE	PROJECT NO - NTPL234
DRAWN	B.B		02.07.2024	PRODUCT - BALCONY ENCLOSURE
CHK'D	B.B.		02.07.2024	SITE LOCATION -
APPV'D	V.T.		02.07.2024	
if any queries contact - supportautomation@nihva.com				REVISION -
ALL DIMENSION ARE IN mm			A3	SCALE - SHEET 1 OF 2

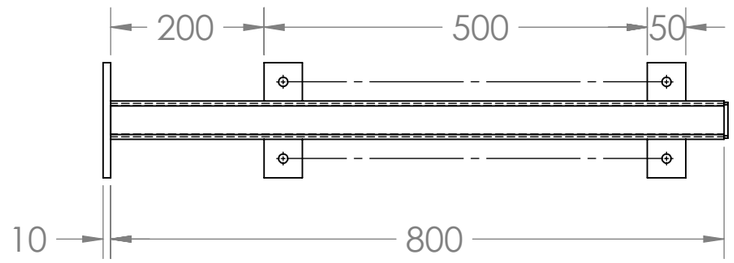


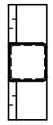


PART NO - 04

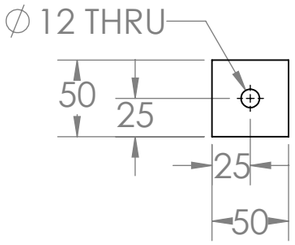


PART NO - 01

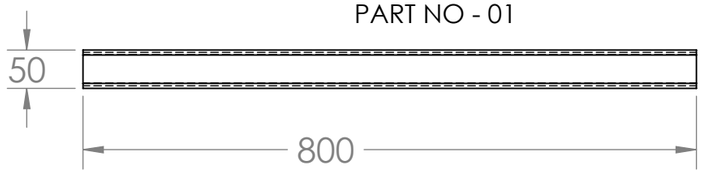


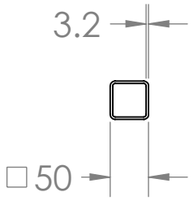

PART NO - 02

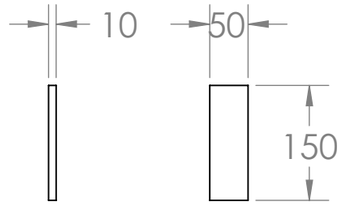

SR, NO.	DESCRIPTION	SIZE	QTY
1	SQ, TUBE	50X50X3THKX800L	03
2	FLAT	50X10THKX150L	03
3	FLAT	50X5THKX50L	03
4	FLAT	50X10THKX50L	12

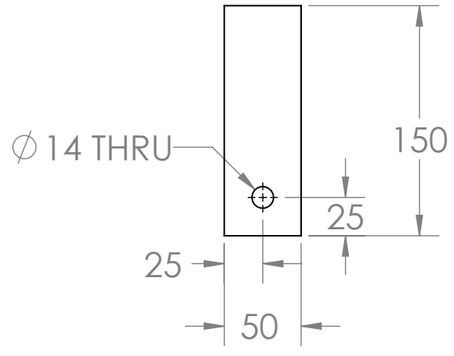


SR, NO.	DESCRIPTION	SIZE	QTY
1	FLAT	50X10THKX150L	10
2	-	-	-
3	-	-	

PART NO - 01



MTL -MS
THK -12MM
QTY-01

PART NO - 02

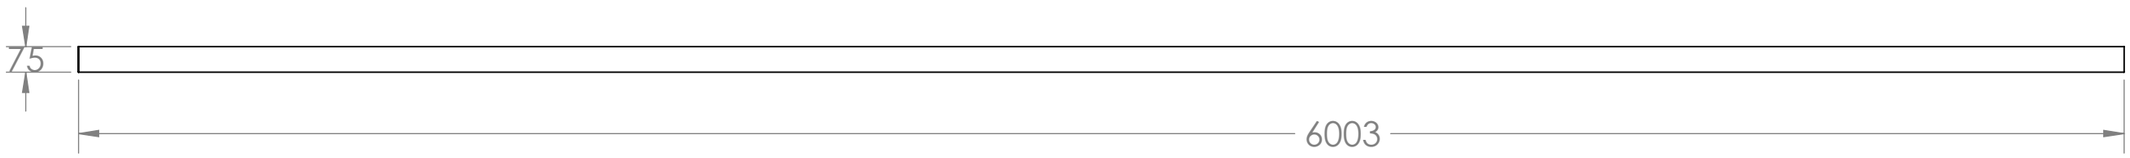

MTL -MS
THK -12MM
QTY-01

TITLE - CIVIL FOUNDATION DRAWING				NIHVA TECHNOLOGIES PVT.LTD.PUNE
DWG NO - NTPL234-			QTY - 1	Website - www.nihva.com
	NAME	SIGNATURE	DATE	PROJECT NO - NTPL234
DRAWN	B.B		10.07.2024	PRODUCT - BALCONY ENCLOSURE
CHK'D	B.B		10.07.2024	SITE LOCATION -
APPV'D	V.T.		10.07.2024	
if any queries contact - supportautomation@nihva.com				REVISION -
ALL DIMENSION ARE IN mm		A3		SCALE - SHEET 2 OF 2