


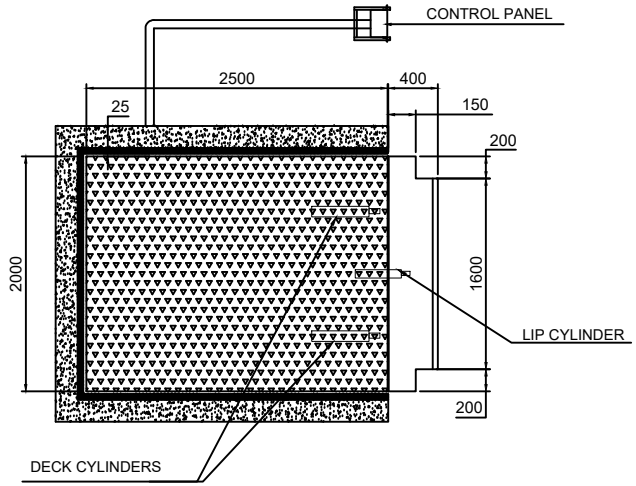


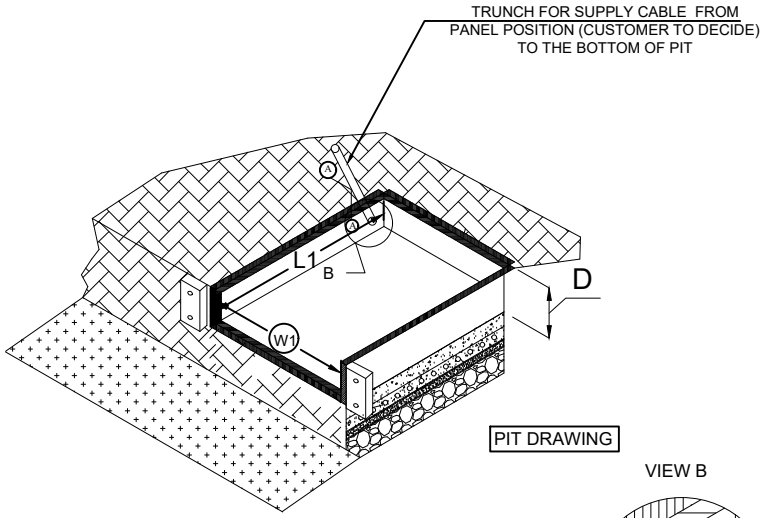


PIT DRAWING

VIEW B

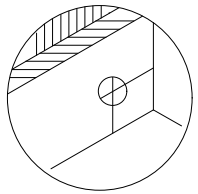

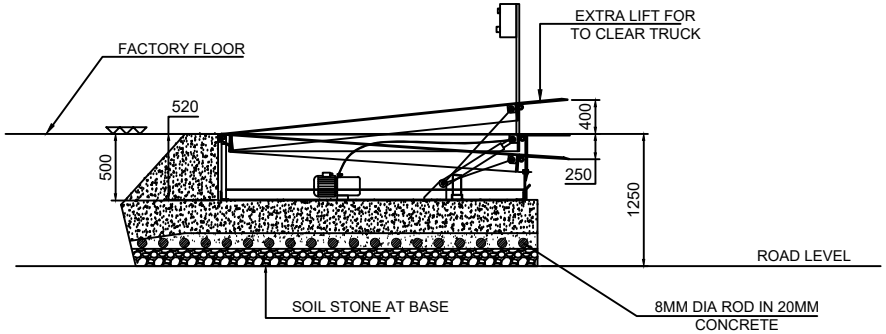

Section at A-A

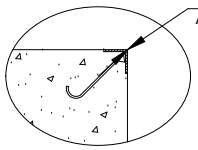

Capacity:- 6 TON

DOCK LEVELER SIZE	WIDTH (W)	LENGTH (L)	HEIGHT (H)	LIP (C) LENGTH	QTY
	2000	2500	500	400	05

NOTE:-

1. ALL DIMENSIONS ARE IN MM
2. THES DRAWING IS FOR UNDERSTANDING PURPOSE
3. PIT,DUCT FOR HOSES & ALL CIVIL WORK IN CLIENT SCOPE

This drawing & design is the property of NIHVA TECHNOLOGIES. Not to be sold or copied to any other concern.

TITLE:- DOCK LEVELER GA DRAWING

NIHVA TECHNOLOGIES PVT. LTD. PUNE
Tel : 020 66304033
Email:- info@nihva.com
Website:- www.nihva.com

	NAME	DATE	SIGN
DRAWN	B.S	10/02/2025	
CHECK	V.T	10/02/2025	
APPRD.	V.T	10/02/2025	

CLIENT - MKC Agro Fresh LTD.

LOCATION - Amravati

PRODUCT - DOCK LEVELER

If any queries contact : design@nihva.com

DWG NO:-NIHVA/24-25/00XX | REV- 0

ALL DIMENSION ARE IN mm

SCALE: NTS | SCALE:-- 1:1 | SHEET: 01 OF 01