





ELEVATION

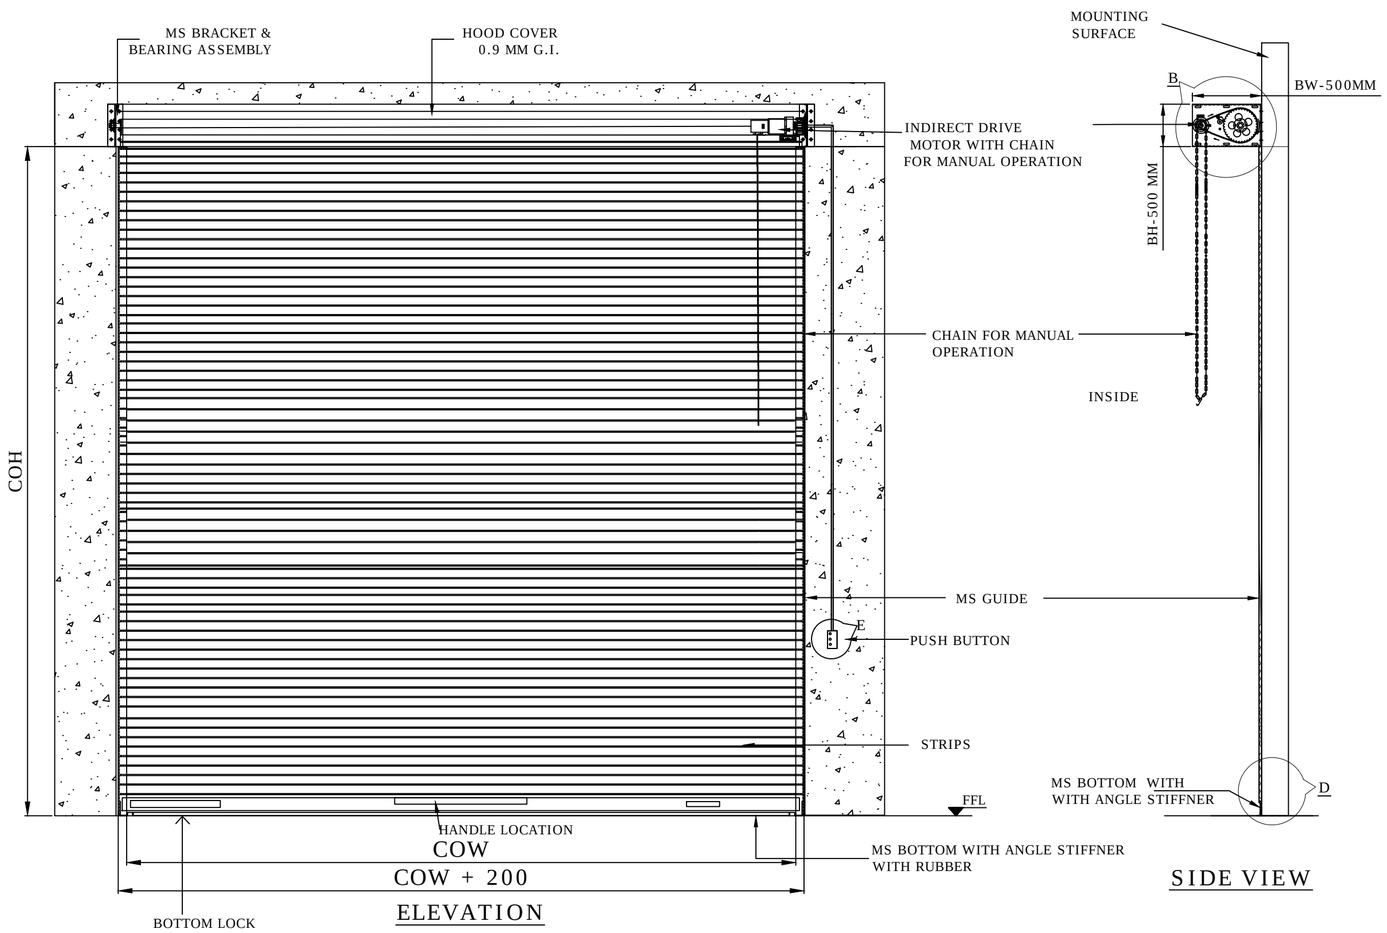


SIDE VIEW

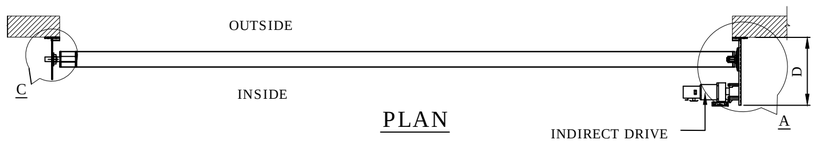



PLAN

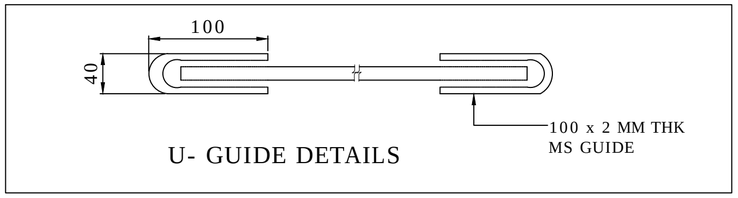



U- GUIDE DETAILS


| RAL CODE | SHADE | COLOUR |
|---|---|---|
| RAL 9001 | CREAM | |
| RAL 9002 | GREY WHITE | |
| RAL 9010 | PURE WHITE | |
| RAL 5002 | ULTRAMARINE BLUE | |
| RAL 7035 | LIGHT GREY | |
| RAL 7001 | SILVER GREY | |

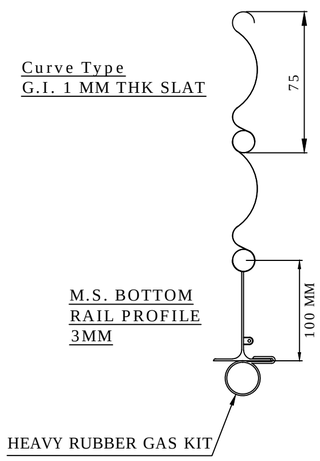


DETAILS : D

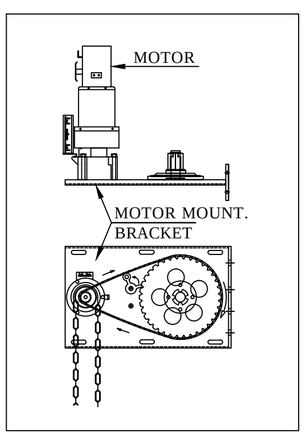


DETAILS : A & B

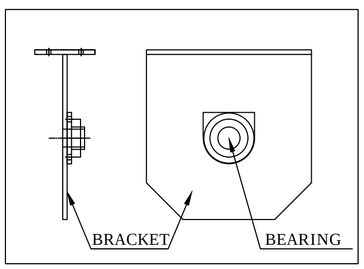


DETAILS : C

NOTES-

1. REFER ABOVE RAL SHADE CHART & CONFIRM RAL SHADE FOR POWDER COATING .
2. CONFIRM MOUNTING OF ROLLING SHUTTER IS ON CONCRETE WALL OR STRUCTURE .
3. IF REQUIRED ALL CIVIL WORK , STRUCTURE & ITS FITTING IS IN CLIENT SCOPE .
4. SPACE OF 700 MM IS REQUIRED ABOVE CLEAR OPENING HEIGHT FOR INSTALLATION OF SHUTTER.

| SR NO | CLEAR OPENING WIDTH (COW) | CLEAR OPENING HEIGHT (COH) | QUANTITY | RAL COLOR POWDER COATED |
|---|---|---|---|---|
| 1 | 4200 | 6000 | 1 NO | |

This drawing & design is the property of NIHVA TECHNOLOGIES. Not to be sold or copied to any other concern.

TITLE GI MOTORIZED ROLLING SHUTTER 4200X6000

| | NAME | SIGN | DATE |
|---|---|---|---|
| DRAWN | S.M.S. | | 5.7.2021 |
| CHECK | A.K. | | 5.7.2021 |
| APPRD. | | | |

NIHVA TECHNOLOGIES PVT. LTD.
NIHVA TECHNOLOGIES PVT. PUNE
Tel : 020 66304033
Email:- info@nihva.com
Website:- www.nihva.com

CLIENT - TAKSHI AUTO COMPONENTS PVT LTD

PROJECT -

SITE LOCATION - AMBETHAN , KHED

If any queries contact :design@nihva.com

DWG. NO. : NIHVA/21-22/029/MRS

REV- R00

ALL DIMENSION ARE IN mm

SCALE: NTS

WT:

SHEET: