


SR NO	DESCRIPTION	SPECIFICATION	QTY
1	R.TUBE	100 X 50 X 3.2 THK X 1800L	2 NOS
2	R.TUBE	100 X 50 X 3.2 THK X 1450L	2 NOS
3	SQ.TUBE	25 X 25 X 2.6 THK X 1600L	13 NOS
4	FLAT	100 X 10 X 125L	2 NOS
5	ISMC	75 X 40 X 150L	2 NOS
4	ANCHOR BOLT	M12 X 150L	8 NOS

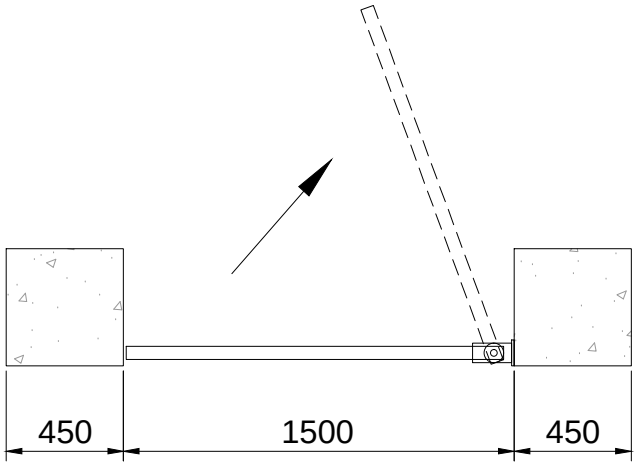

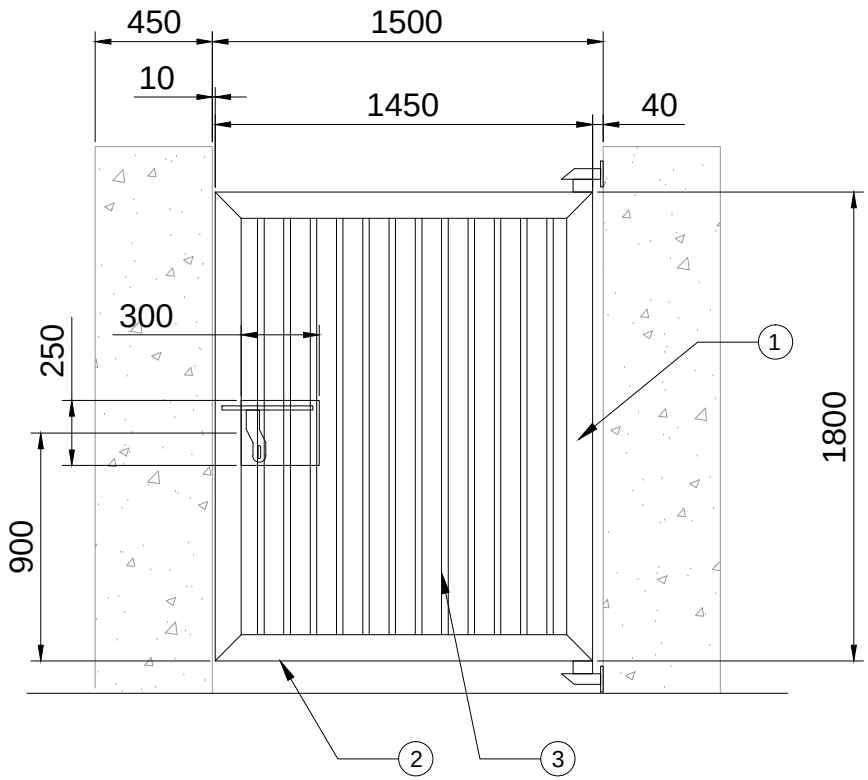

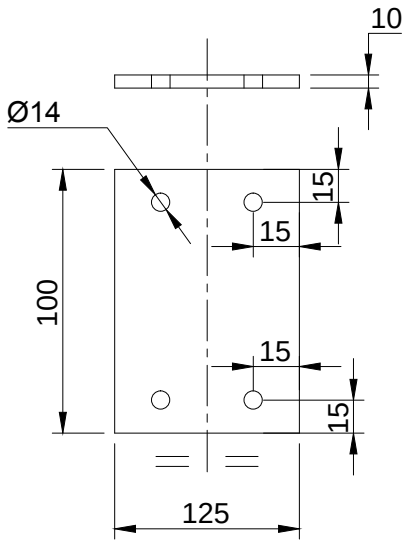

TOLERANCE- ±2mm

This drawing & designing is the property of NIHVA TECHNOLOGIES. Not to be sold or copied to any other concern.

TITLE: WICKET GATE

NIHVA TECHNOLOGIES PVT. LTD.

NIHVA TECHNOLOGIES PVT. LTD. PUNE
Tel : 020 66304033
Email:- info@nihva.com
Website:- www.nihva.com

	NAME	SIGN	DATE
DRAWN	P.A		30.01.20
CHECK	G.J		30.01.20
APPROVAL			

CLIENT -

PROJECT -

SITE LOCATION -

If any queries contact : design@nihva.com

DWG. NO. : NIHVA/19-20/VDR/302 REV.:- 00

ALL DIMENSION ARE IN mm

SCALE: NTS WT: SHEET: 01 OF 01