

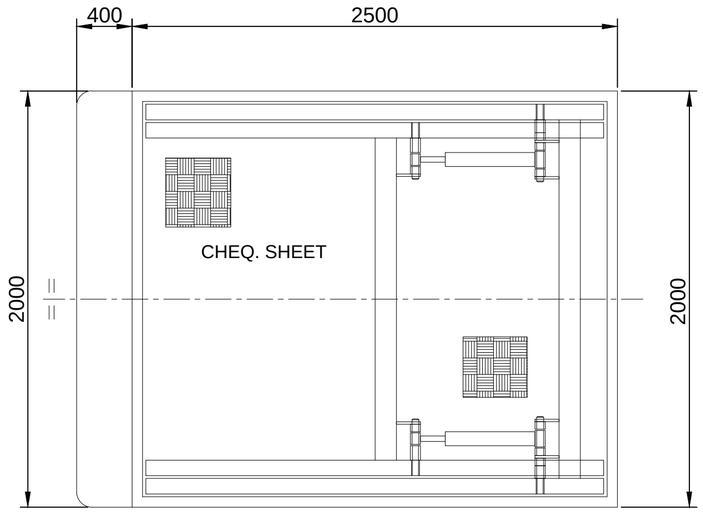



TOP VIEW

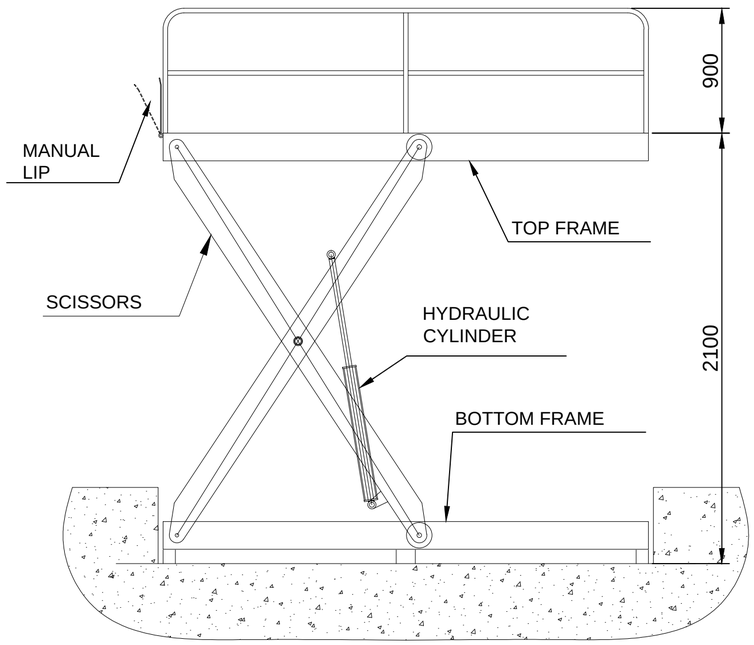

OPEN HEIGHT FRONT VIEW

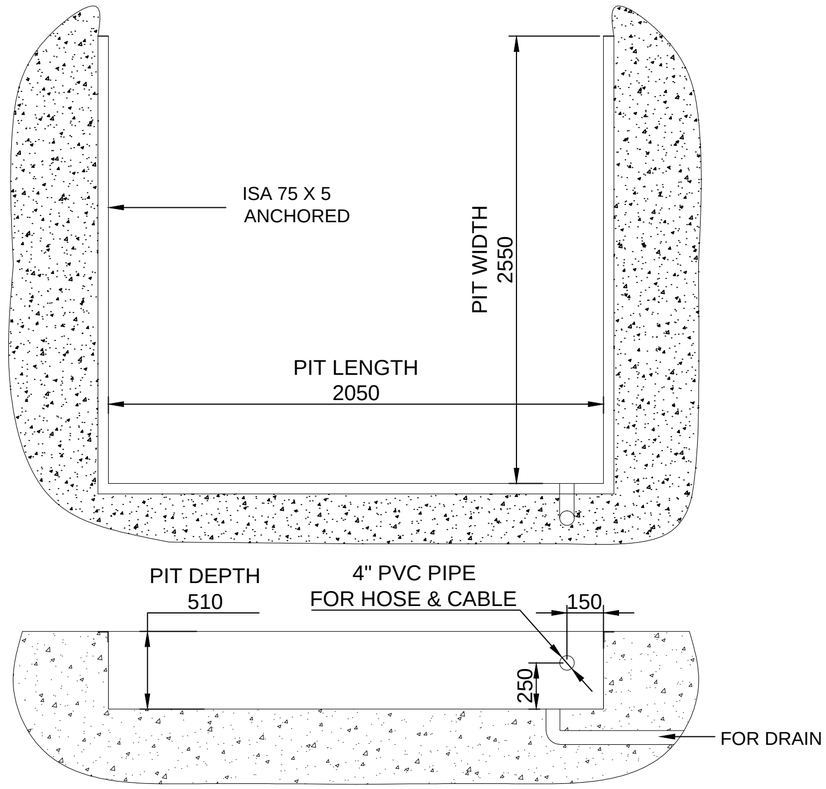

PIT DRAWING

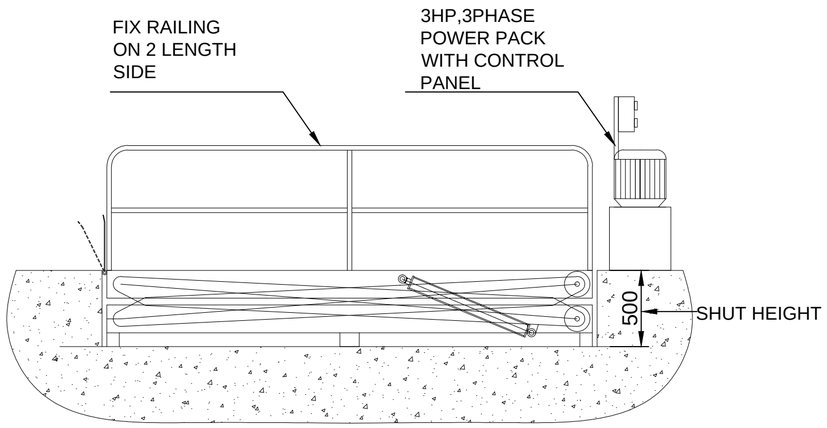

CLOSED HEIGHT FRONT VIEW

NOTE :

1. PIT FOR SCISSORLIFT HAS TO BE DIAGONALLY WITHIN 3-5 MM
2. BASE OF THE PIT HAS TO BE IN WATER LEVEL AND RIGHT ANGLE TO THE VERTICAL SIDE WALLS
3. PROPER ARRANGEMENT FOR ROUTING HOSES AND CABLES HAVE TO BE MADE DEPENDING ON SITE CONDITIONS AND POSITION OF POWER PACK
4. COVERING REQUIRED FOR CABLES AND RELATED CIVIL WORK IS IN CLIENTS SCOPE
5. WATER DRAINAGE AND PIT CLEANING NEEDS TO BE CONSIDERED AND DONE BY CLIENT
6. PIT & ALL CIVIL WORK IS IN CLIENT SCOPE.
7. TOLERANCE ± 10 MM.

SAFETY RAILING	900 MM HT
POWER PACK	3HP,3PHASE
MAX HT	2100MM
LIFT HT	1600 MM
SHUT HT	500 MM
PLATFORM SIZE	2000W x 2500L
CAPACITY	1.5 TON

Rev No.	Revision	Date	Revised By

This drawing & design is the property of NIHVA TECHNOLOGIES. Not to be sold or copied to any other concern.

TITLE:- PIT MOUNTED SCISSOR LIFT

NIHVA TECHNOLOGIES PVT. LTD. PUNE
Tel : 020 66304033
Email:- info@nihva.com
Website:- www.nihva.com

	NAME	DATE	SIGN
DRAWN	SUJATA.B	25/10/2021	
CHECK	G.PATIL	25/10/2021	
APPRD.	A.KURHADE	25/10/2021	

CLIENT - EMCURE PHARMACEUTICALS LIMITED

LOCATION - AHMEDABAD

PRODUCT - SCISSOR LIFT

If any queries contact : design@nihva.com

DWG NO:-NIHVA\21-22\0254 REV- 0

ALL DIMENSION ARE IN mm

SCALE: NTS SCALE:-- 1:1 SHEET: 01 OF 01