

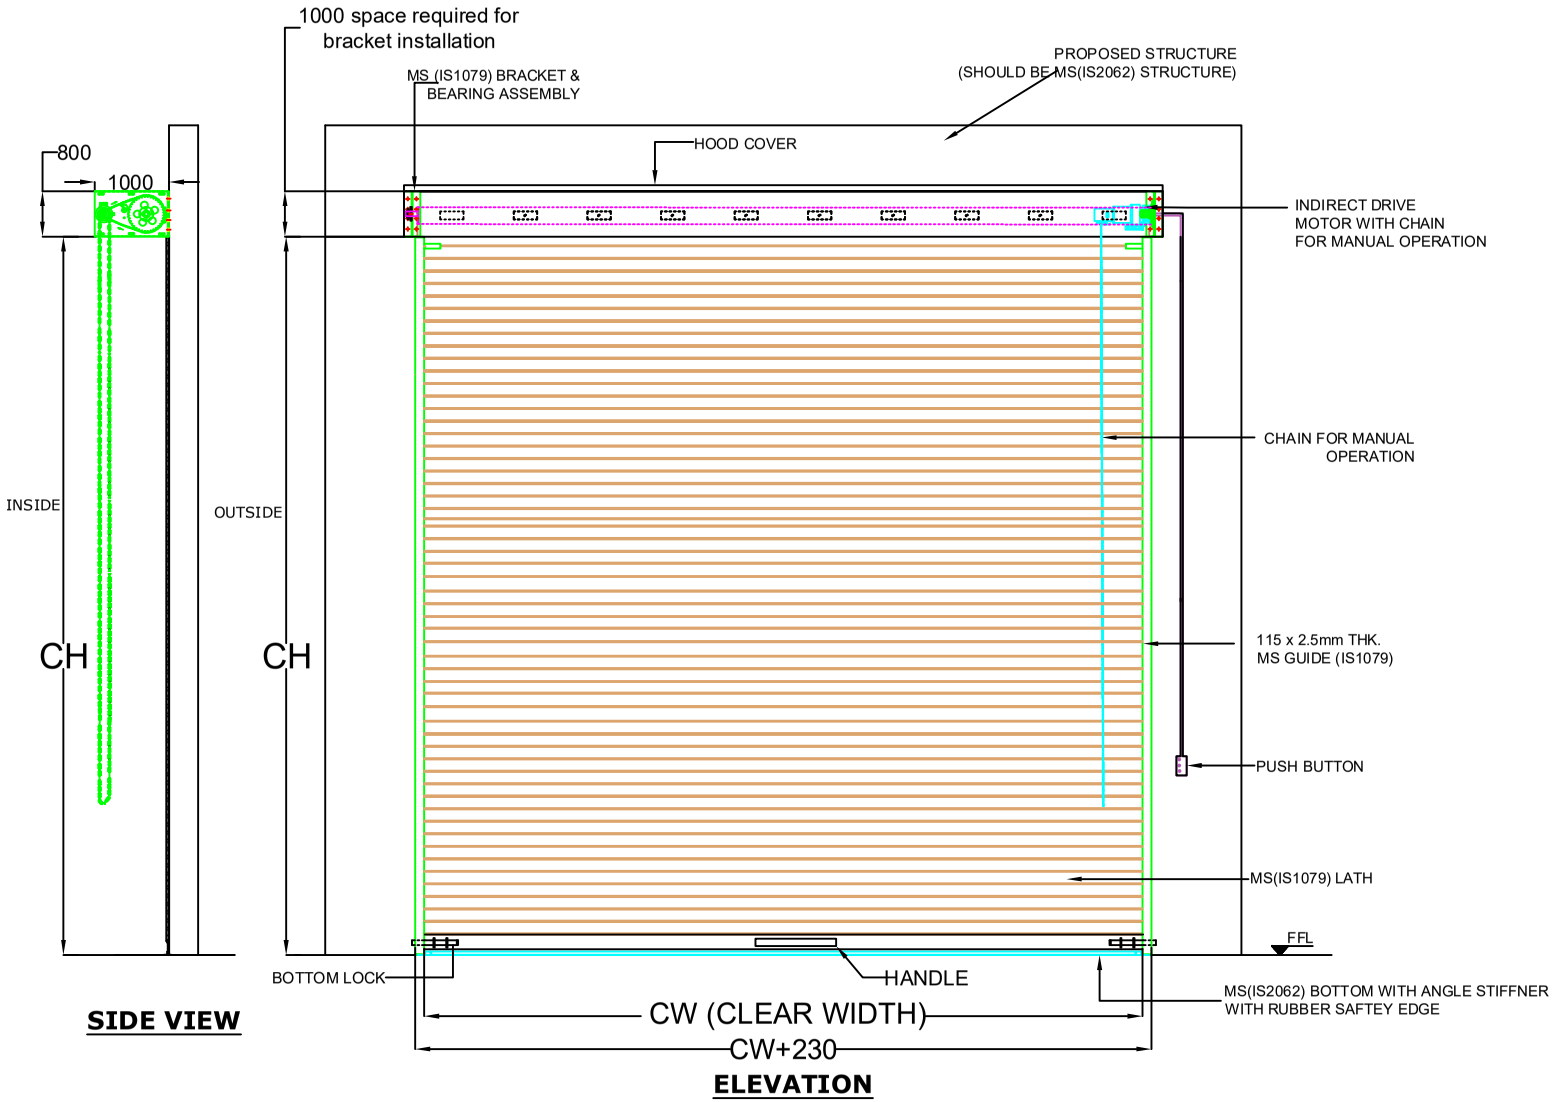


SIDE VIEW


ELEVATION

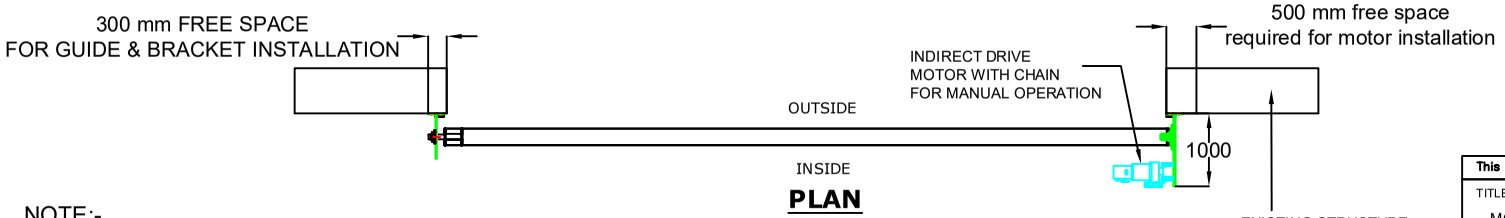

PLAN

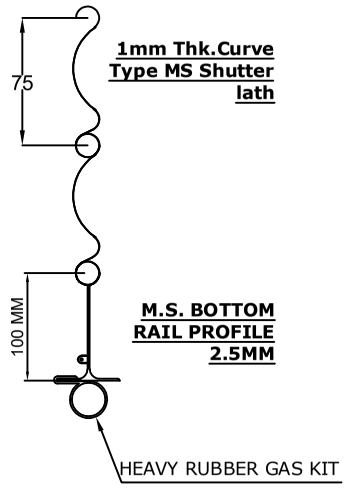

M.S. BOTTOM RAIL PROFILE 2.5MM

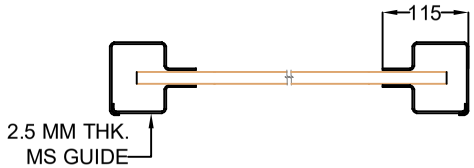

COLOR:-
1. RAL7035(LIGHT GRAY) ☐
2. RAL9016(TRAFFIC WHITE) ☐
3. RAL5005(SIGNAL BLUE) ☐
4. RAL7004(SIGNAL GRAY) ☐
5. RAL5015(SKY BLUE) ☑

CLEAR WIDTH (CW)	CLEAR HEIGHT (CH)	QUANTITY
5000	6000	04

NOTE:-
1. REQUIRED STRUCTURE FOR ROLLING SHUTTER SHALL BE IN NIHVA SCOPE.
2. ALL REQUIRED CIVIL WORK IN CLIENT SCOPE.
3. 3 PHASE POWER SUPPLY SHOULD BE PROVIDED BY CLIENT.
4. MOTOR : JIELONG , 1.5 TON, 1.25 KW, 3PH
5. PRIMER COAT THICKNESS WILL BE 40 MICRON AND FINISH COAT THICKNESS WILL BE 60 MICRON

REV01.(04/04/2022)
1 MOTOR DETAILS AND PAINT DETAILS TO BE ADDED
2. Grill Removed

This drawing & designing is the property of NIHVA TECHNOLOGIES. Not to be sold or copied to any other concern.

TITLE: MOTORIZED ROLLING SHUTTER

NIHVA TECHNOLOGIES PVT. LTD.

NIHVA TECHNOLOGIES PVT. LTD. PUNE
Tel : 020 66304033
Email:- info@nihva.com
Website:- www.nihva.com

	NAME	SIGN	DATE
DRAWN	G.P.		11/02/22
CHECK	A.K.		11/02/22
APPROVAL	V.T.		11/02/22

CLIENT -REWARD CONSTRUCTION
PROJECT -
SITE - INDAPUR

If any queries contact : design@nihva.com
DWG. NO. : NIHVA/21-22/CLT/347
REV. - 01
ALL DIMENSION ARE IN mm
SCALE: NTS
WT:
SHEET: 01 OF 01