
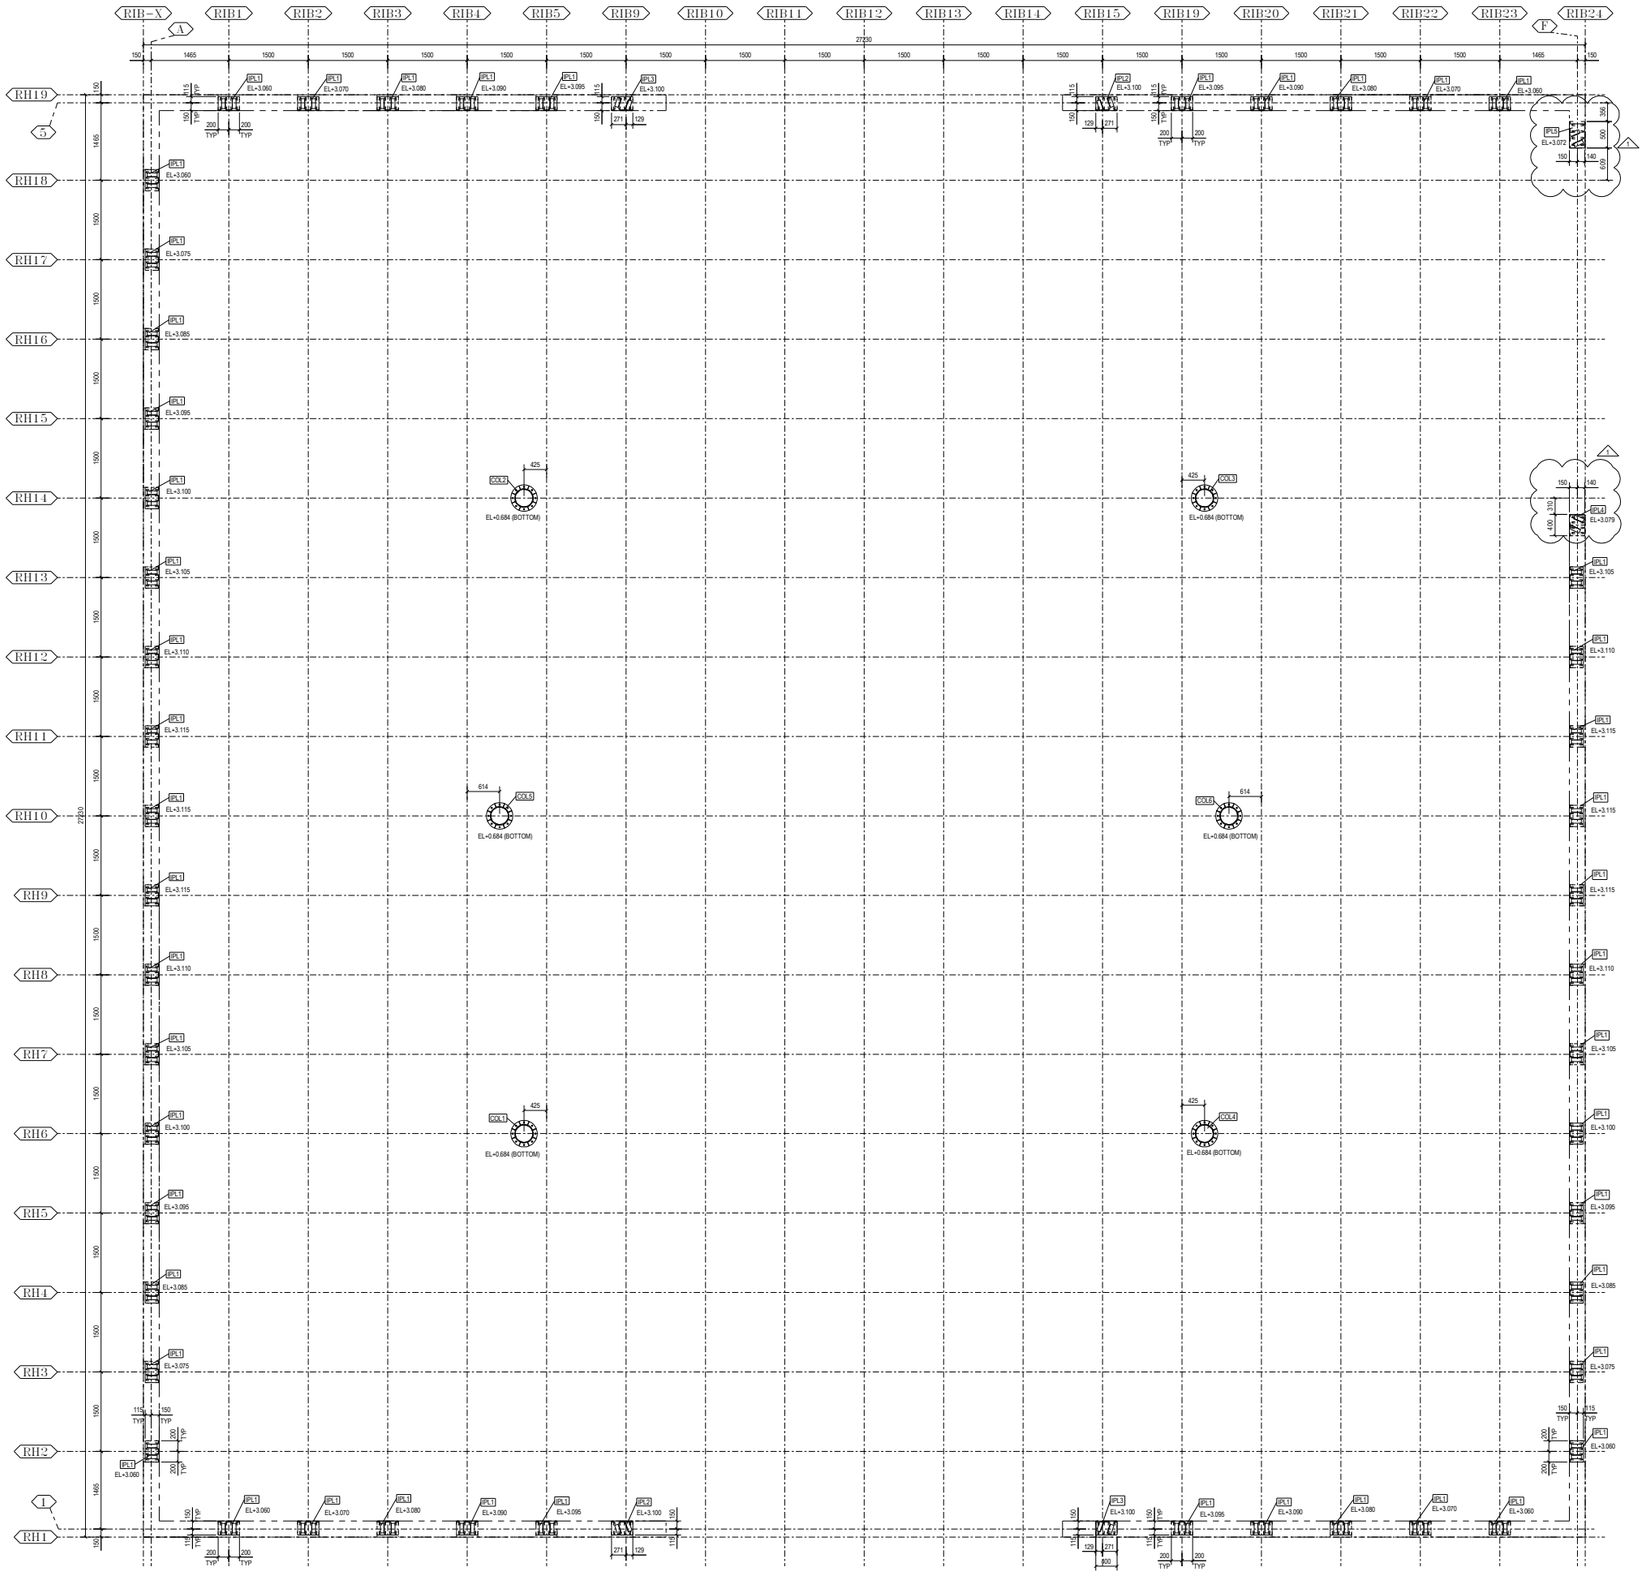
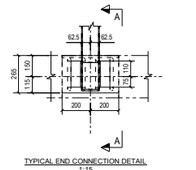
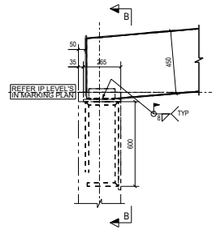



INSERT PLATE MARKING PLAN
SCALE- 1:40

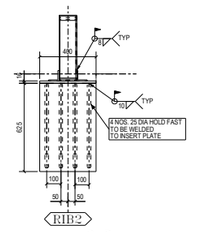


GENERAL NOTES :

1. ALL DIMENSIONS ARE IN MM.
2. GRADE OF STEEL SHALL BE FE-500D CONFORMING TO IS1786 - 2008.
3. DO NOT SCALE THE DRAWING, ONLY WRITTEN DIMENSIONS TO BE FOLLOWED.
4. ANY DISCREPANCY IN THE DWG TO BE BROUGHT TO THE NOTICE OF THE CONSULTANT BEFORE EXECUTION.
5. FOR ALL LEVELS AND DIMENSIONS REFER ARCH DRAWINGS.
6. ALL LEVELS & DIMENSIONS TO BE CONFIRMED AT SITE BEFORE EXECUTION.
7. ALL LEVELS TO BE CO-ORDINATED & RECONFIRMED WITH ARCHITECTURAL DRAWINGS.
8. ALL TRENCH SIZES INSERT SLEEVES & CUTOUTS TO BE CO-ORDINATED & RECONFIRMED WITH ARCHITECTURAL & MEP DRAWINGS.
9. ALL SHOP AND SITE WELDS ARE 8mm FILLET MIN. U.N.O.
10. CHECK ALL DIMENSIONS BEFORE FABRICATION OF STRUCTURAL STEEL WORK.
11. GRADE OF STEEL YST-250.
12. ⊕ INDICATES ORIENTATION MARK.

DIRECTION

CONTRACTOR–

UNIVASTU INDIA LTD
Let's Succeed Together!

UNIVASTU INDIA PVT LTD
PUNE (INDIA) 411038

PROJECT NO.


| | |
|---|---|
| PROJECT: | SHRI. MANOHAR PARRIKAR SMRITI STHAL |
| CLIENT: | GENERAL ADMINISTRATIVE DEPARTMENT,GOA |
| ARCHITECT: | UCJ ARCHITECTURE & ENVIRONMENT |
| STRUCTURAL ENGG.: | SHANGHAVI & ASSOCIATES CONSULTANTS Pvt. Ltd. |
| DRAWING TITLE: | INSERT PLATE MARKING PLAN |

| | DATE | INITIALS | SIGN. | SCALE | ORIG.SIZE | TOTAL PAGES |
|---|---|---|---|---|---|---|
| DRAWN | 03.09.2021 | VISHWATECH | | 1:40 | A4 (X1.189) | 1 |
| CHECKED | 03.09.2021 | SG | | DWG NO.: GSS–ST–GA–101 | PAGE 1 | REV. 1 |
| ENGINEER | 03.09.2021 | SG | | | | |
| APPROVED | 03.09.2021 | SG | | | | |


| REV. | REVISION | | | |
|---|---|---|---|---|
| 1 | HOLD RELEASED. | VT 23.09.2021 | SG 23.09.2021 | SG 23.09.2021 |
| 0 | ISSUED FOR APPROVAL | VT 04.09.2021 | SG 04.09.2021 | SG 04.09.2021 |

COMPUTER FILE NAME :– COMPUTER FILE LOCATION :–


SHEET SIZE– A0

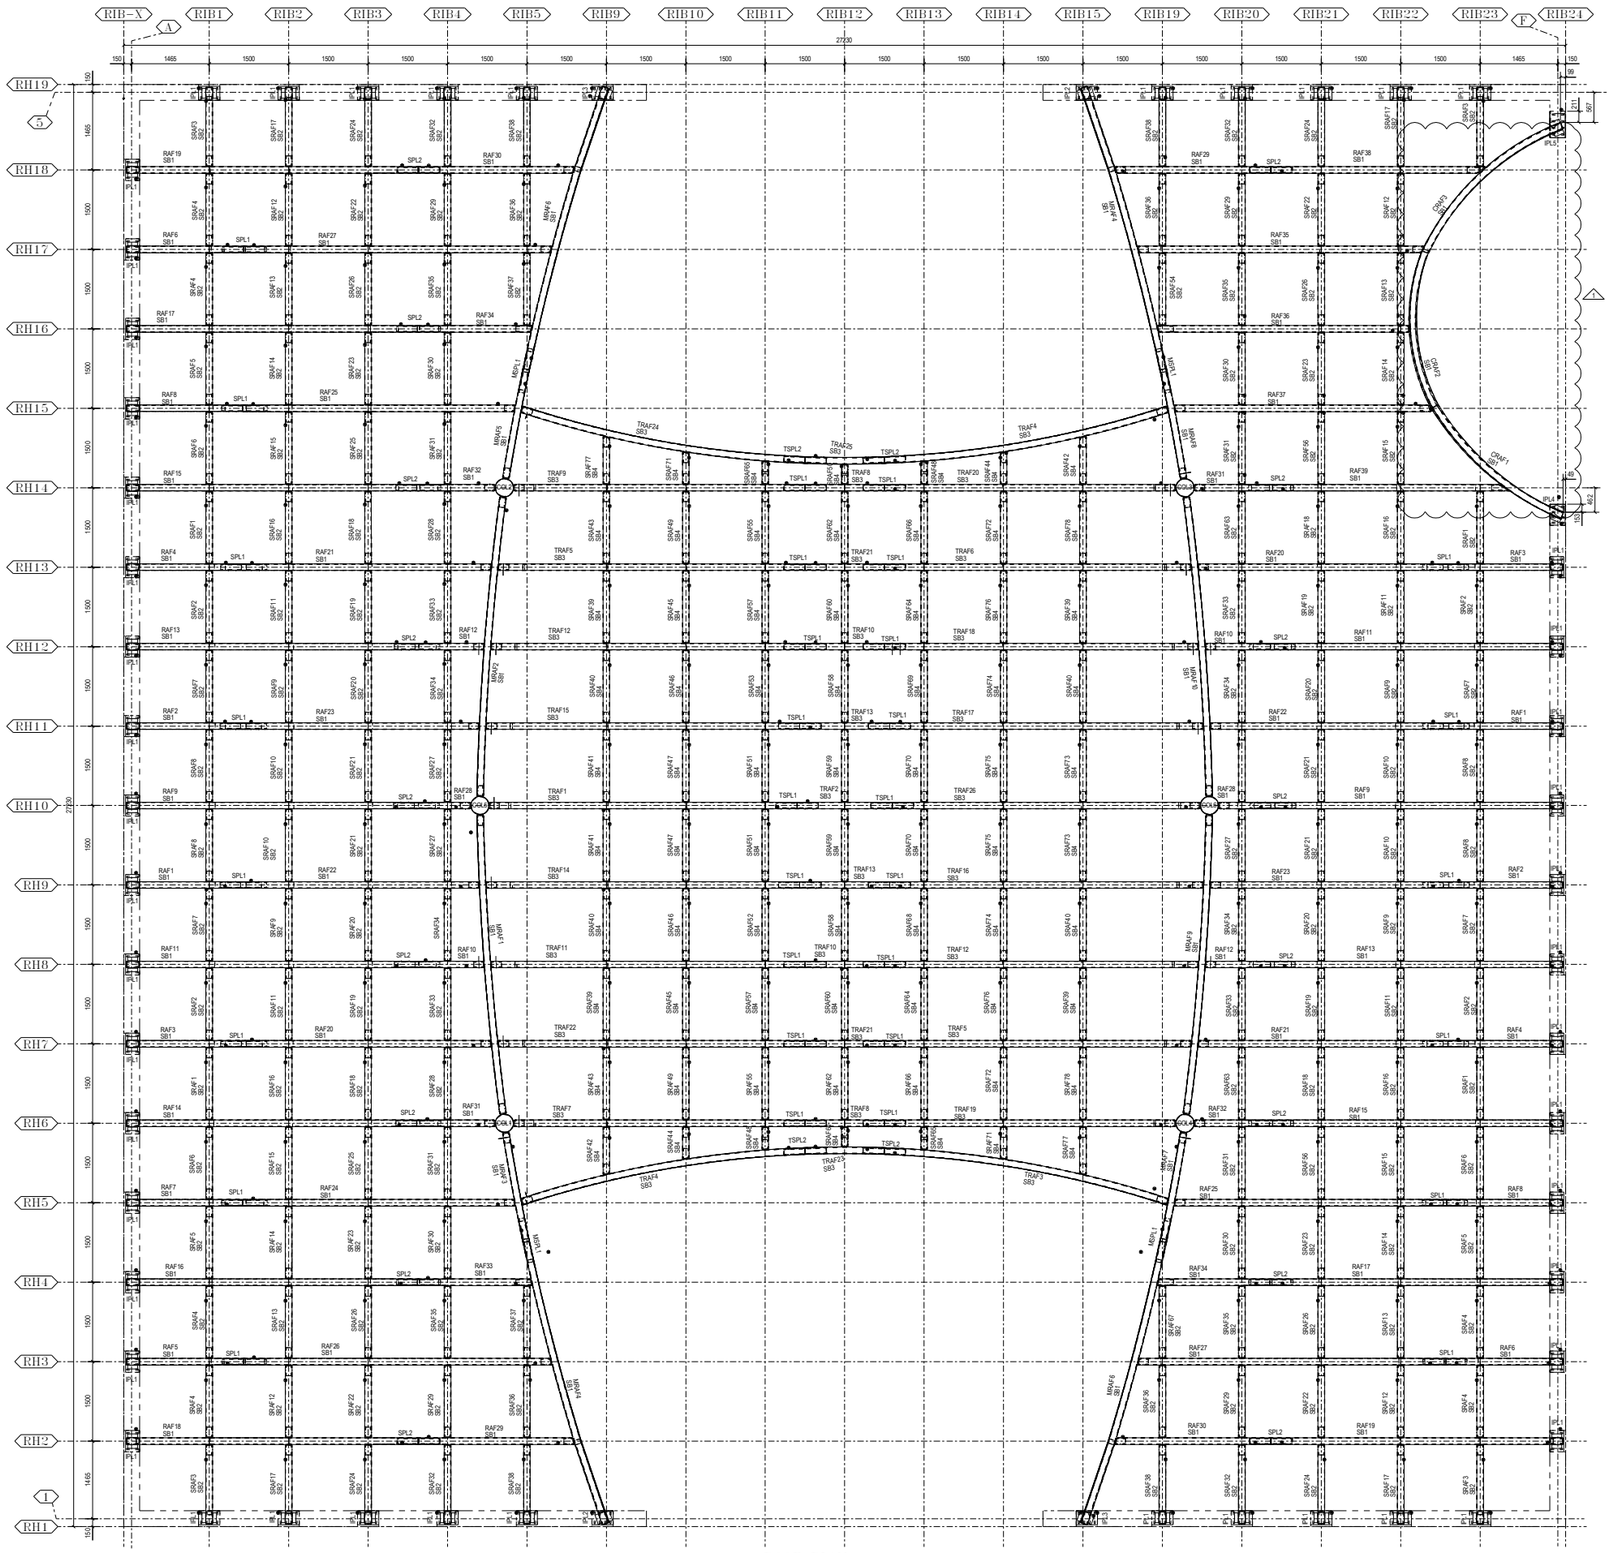



ROOF PLAN
SCALE - 1:40

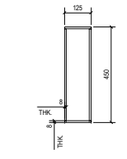



TYPICAL DETAIL -SB1
1:10

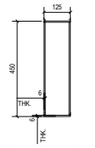



TYPICAL DETAIL -SB2
1:10

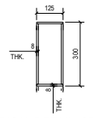



TYPICAL DETAIL -SB3
1:10

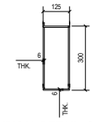



TYPICAL DETAIL -SB4
1:10

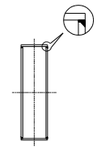


TYPICAL WELDING DETAIL

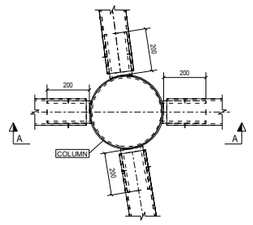



TYPICAL CONNECTION DETAIL
COLUMN WITH BEAM
1:10

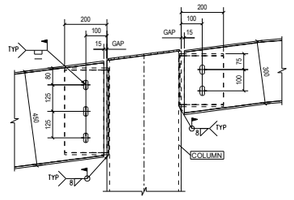


A - A
1:10

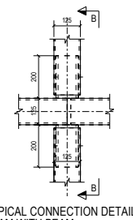


TYPICAL CONNECTION DETAIL
BEAM WITH BEAM
1:10

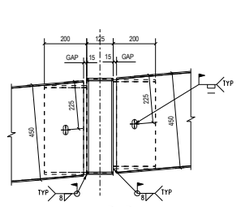


B - B
1:10

GENERAL NOTES :

1. ALL DIMENSIONS ARE IN MM.
2. GRADE OF STEEL SHALL BE FE-500D CONFORMING TO IS1786 - 2008.
3. DO NOT SCALE THE DRAWING, ONLY WRITTEN DIMENSIONS TO BE FOLLOWED.
4. ANY DISCREPANCY IN THE DWG TO BE BROUGHT TO THE NOTICE OF THE CONSULTANT BEFORE EXECUTION.
5. FOR ALL LEVELS AND DIMENSIONS REFER ARCH DRAWINGS.
6. ALL LEVELS & DIMENSIONS TO BE CONFIRMED AT SITE BEFORE EXECUTION.
7. ALL LEVELS TO BE CO-ORDINATED & RECONFIRMED WITH ARCHITECTURAL DRAWINGS.
8. ALL TRENCH SIZES INSERT SLEEVES & CUTOUTS TO BE CO-ORDINATED & RECONFIRMED WITH ARCHITECTURAL & MEP DRAWINGS.
9. ALL SHOP AND SITE WELDS ARE 8mm FILLET MIN. U.N.O.
10. CHECK ALL DIMENSIONS BEFORE FABRICATION OF STRUCTURAL STEEL WORK.
11. GRADE OF STEEL YST-250.
12. ⊕ INDICATES ORIENTATION MARK.

DIRECTION




CONTRACTOR-

Let's Succeed Together!
UNIVASTU INDIA LTD

UNIVASTU INDIA PVT LTD
PUNE (INDIA) 411038

PROJECT NO.

| | |
|---|---|
| PROJECT: | SHRI. MANOHAR PARRIKAR SMRITI STHAL |
| CLIENT: | GENERAL ADMINISTRATIVE DEPARTMENT,GOA |
| ARCHITECT: | UCJ ARCHITECTURE & ENVIRONMENT |
| STRUCTURAL ENGG.: | SHANGHAVI & ASSOCIATES CONSULTANTS Pvt. Ltd. |
| DRAWING TITLE: | PLAN AT ROOF LVL |


| | DATE | INITIALS | SIGN. |
|---|---|---|---|
| DRAWN | 20.08.2021 | VISHWATECH | |
| CHECKED | 20.08.2021 | SG | |
| ENGINEER | 20.08.2021 | SG | |
| APPROVED | 20.08.2021 | SG | |

SCALE: 1:40 | ORIG.SIZE: A4/A1/1189 | TOTAL PAGES: 1


DWG NO: GSS-ST-GA-102

PAGE: 1 | REV.: 1


| NO/Rv | REVISION | INITIALS | DATE | CHECKED | APPROVED |
|---|---|---|---|---|---|
| 1 | HOLD RELEASED. | VT | 21.09.2021 | SG | SG |
| 0 | ISSUED FOR APPROVAL | VT | 04.09.2021 | SG | SG |
| | | MOST | DATE | CHECKED | APPROVED |

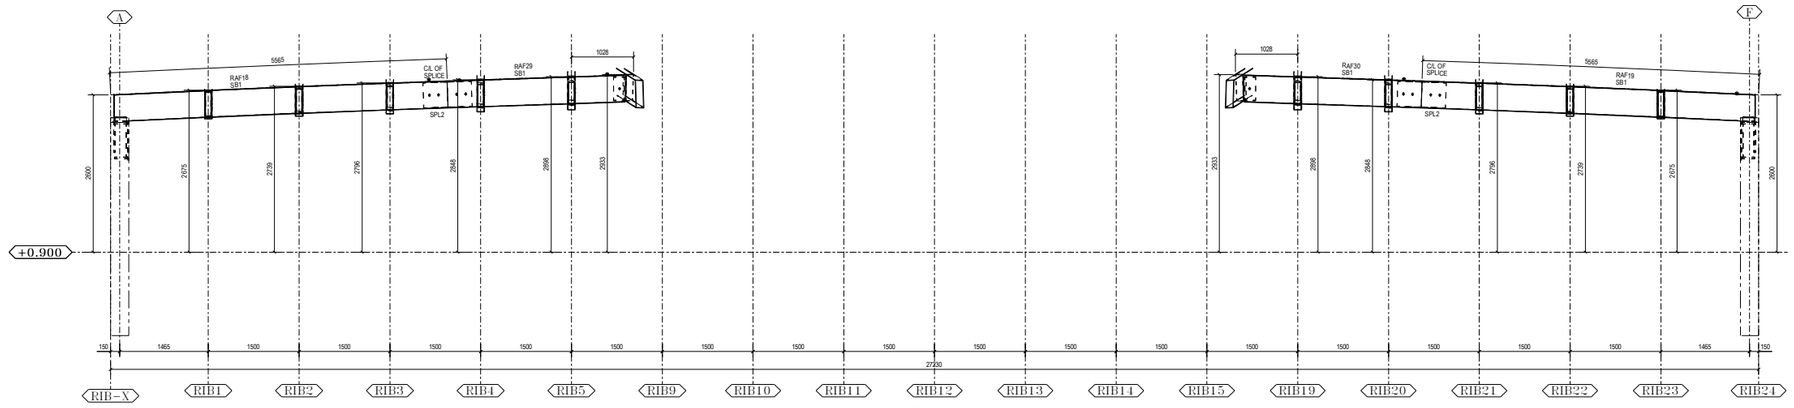


GRID@ RH2
SCALE- 1:35

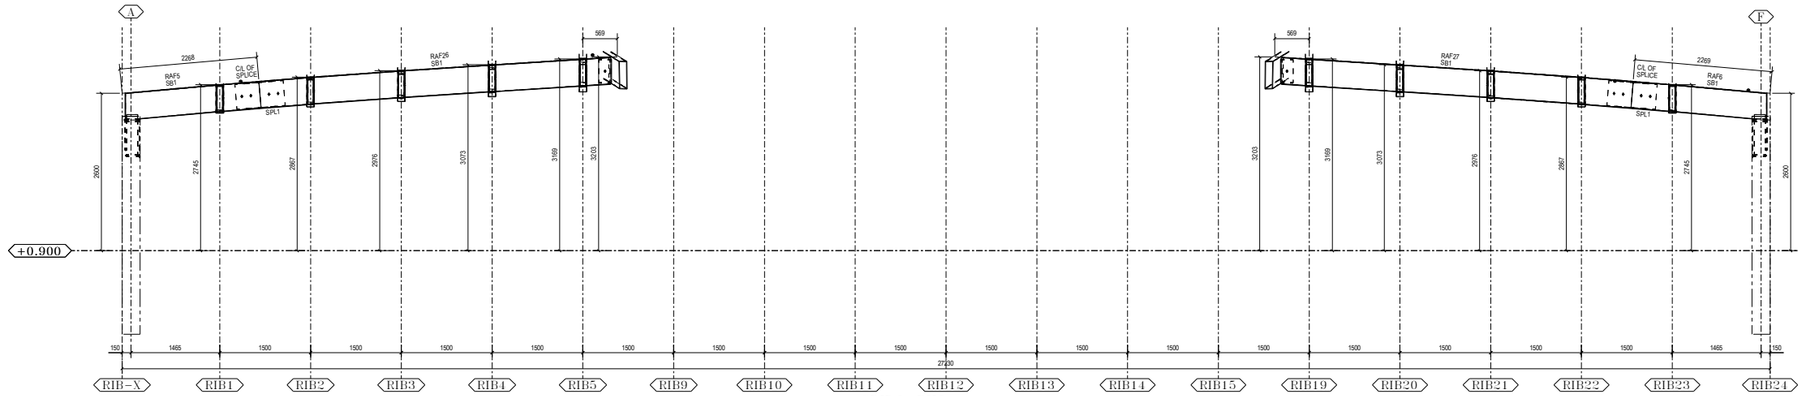


GRID@ RH3
SCALE- 1:35

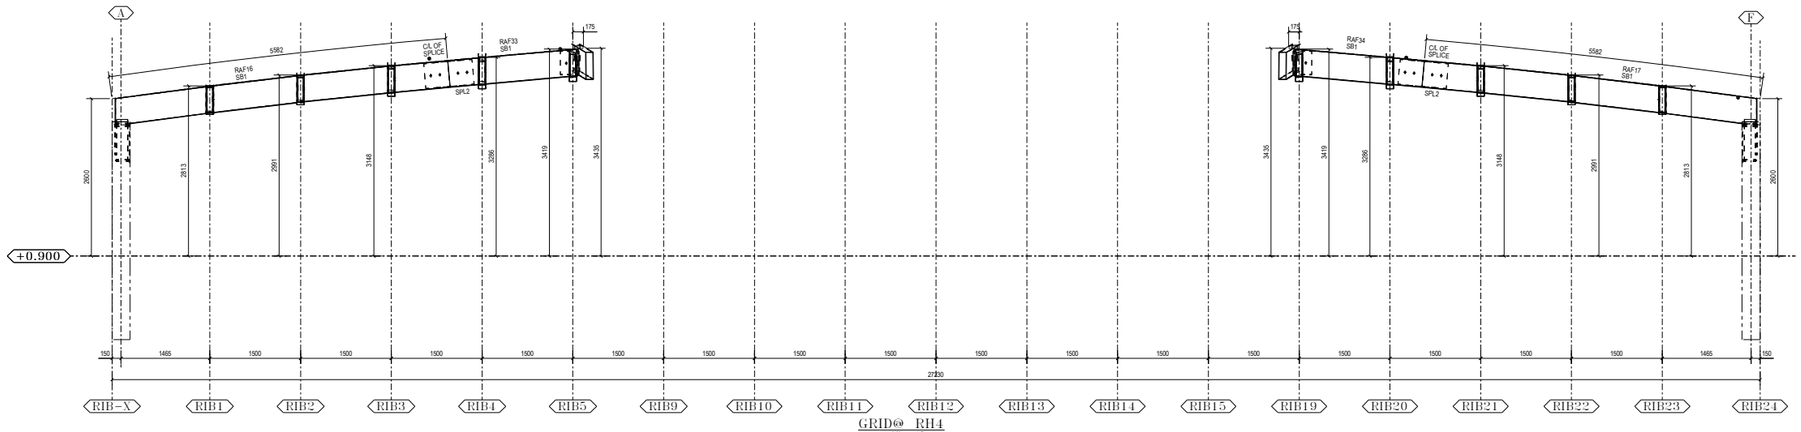


GRID@ RH4
SCALE- 1:35

GENERAL NOTES :

1. ALL DIMENSIONS ARE IN MM.
2. GRADE OF STEEL SHALL BE FE-500D CONFORMING TO IS1786 - 2008.
3. DO NOT SCALE THE DRAWING, ONLY WRITTEN DIMENSIONS TO BE FOLLOWED.
4. ANY DISCREPANCY IN THE DWG TO BE BROUGHT TO THE NOTICE OF THE CONSULTANT BEFORE EXECUTION.
5. FOR ALL LEVELS AND DIMENSIONS REFER ARCH DRAWINGS.
6. ALL LEVELS & DIMENSIONS TO BE CONFIRMED AT SITE BEFORE EXECUTION.
7. ALL LEVELS TO BE CO-ORDINATED & RECONFIRMED WITH ARCHITECTURAL DRAWINGS.
8. ALL TRENCH SIZES INSERT SLEEVES & CUTOUTS TO BE CO-ORDINATED & RECONFIRMED WITH ARCHITECTURAL & MEP DRAWINGS.
9. ALL SHOP AND SITE WELDS ARE 8mm FILLET MIN. U.N.O.
10. CHECK ALL DIMENSIONS BEFORE FABRICATION OF STRUCTURAL STEEL WORK.
11. GRADE OF STEEL YST-250.
12. ⬢ INDICATES ORIENTATION MARK.

DIRECTION




CONTRACTOR-

Let's Succeed Together!
UNIVASTU INDIA LTD


UNIVASTU INDIA PVT LTD
PUNE (INDIA) 411038

PROJECT NO:

| | |
|---|---|
| PROJECT: | SHRI. MANOHAR PARRIKAR SMRITI STHAL |
| CLIENT: | GENERAL ADMINISTRATIVE DEPARTMENT,GOA |
| ARCHITECT: | UCJ ARCHITECTURE & ENVIRONMENT |
| STRUCTURAL ENGG.: | SHANGHAVI & ASSOCIATES CONSULTANTS Pvt. Ltd. |
| DRAWING TITLE: | ELEVATION ALONG GRID RH2, RH3 & RH4 |

| | DATE | INITIALS | SIGN. | SCALE | ORIG.SIZE | TOTAL PAGES |
|---|---|---|---|---|---|---|
| DRAWN | 04.09.2021 | VISHWANTH | | 1:35 | A4/A1/ISB | 1 |
| CHECKED | 04.09.2021 | SG | | DWG NO : GSS-ST-GA-103 | | PAGE 1 / REV. 0 |
| ENGINEER | 04.09.2021 | SG | | | | |
| APPROVED | 04.09.2021 | SG | | | | |


CONSTRUCTION PURPOSE
SHEET SIZE- A0

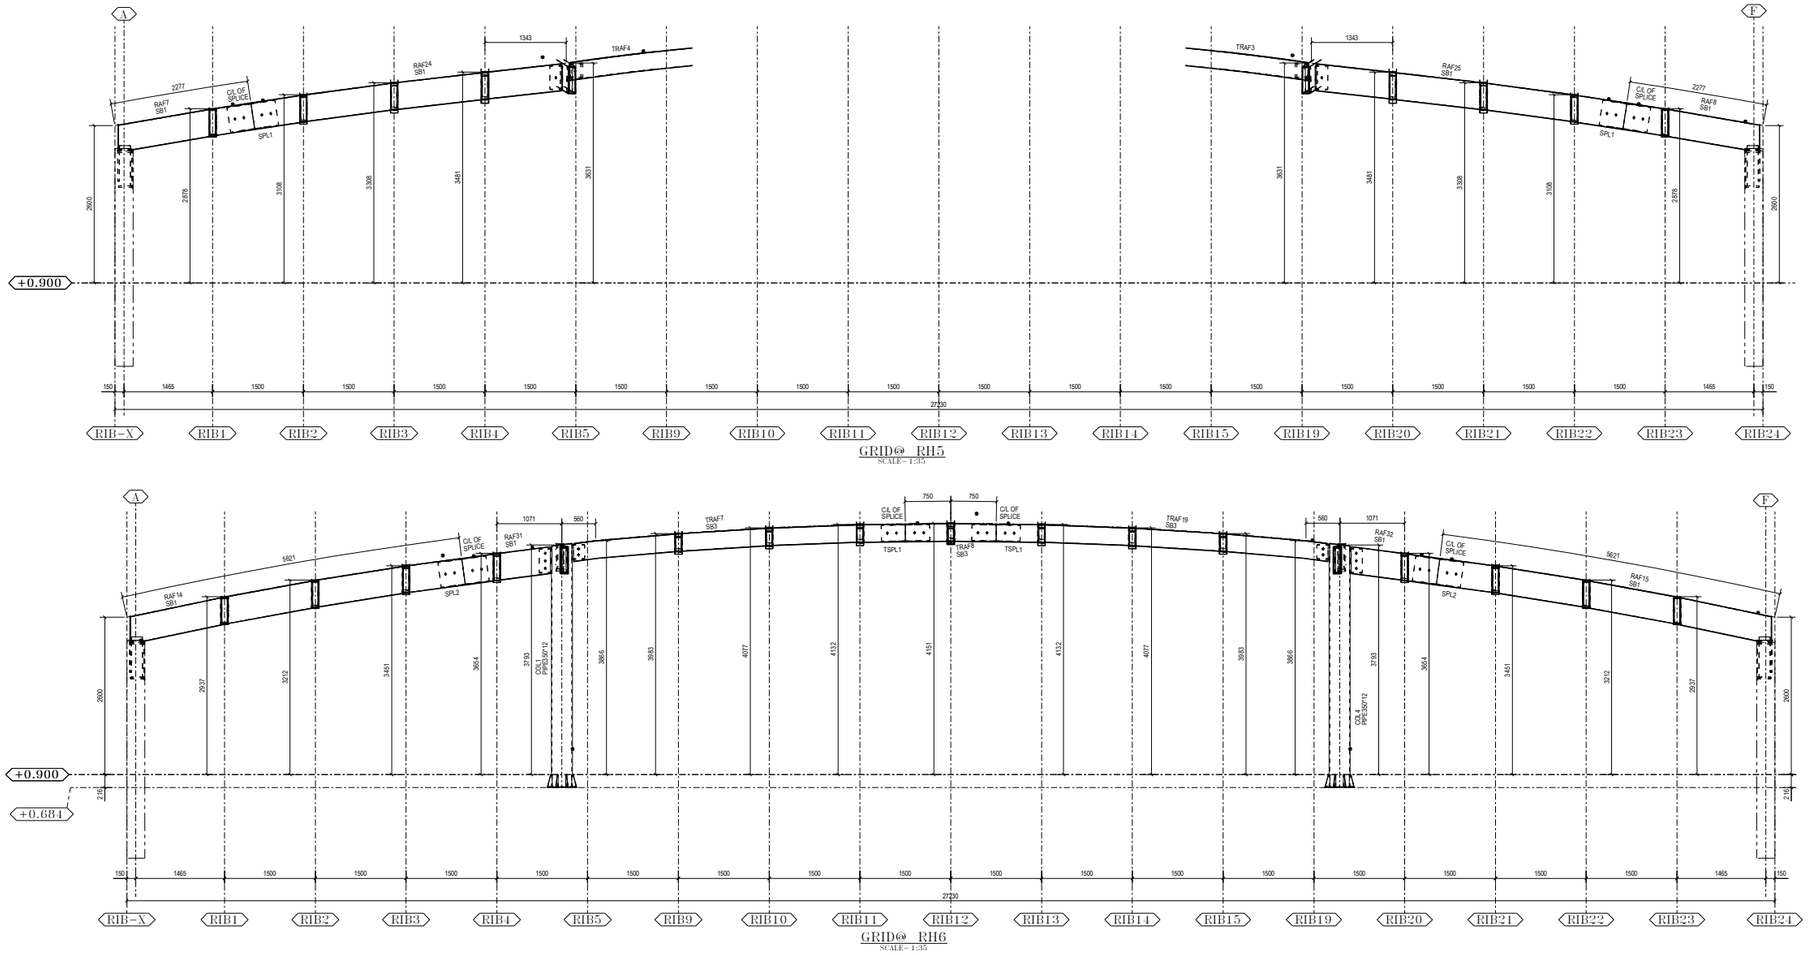


GRID@ RH5
SCALE- 1:35




GRID@ RH6
SCALE- 1:35

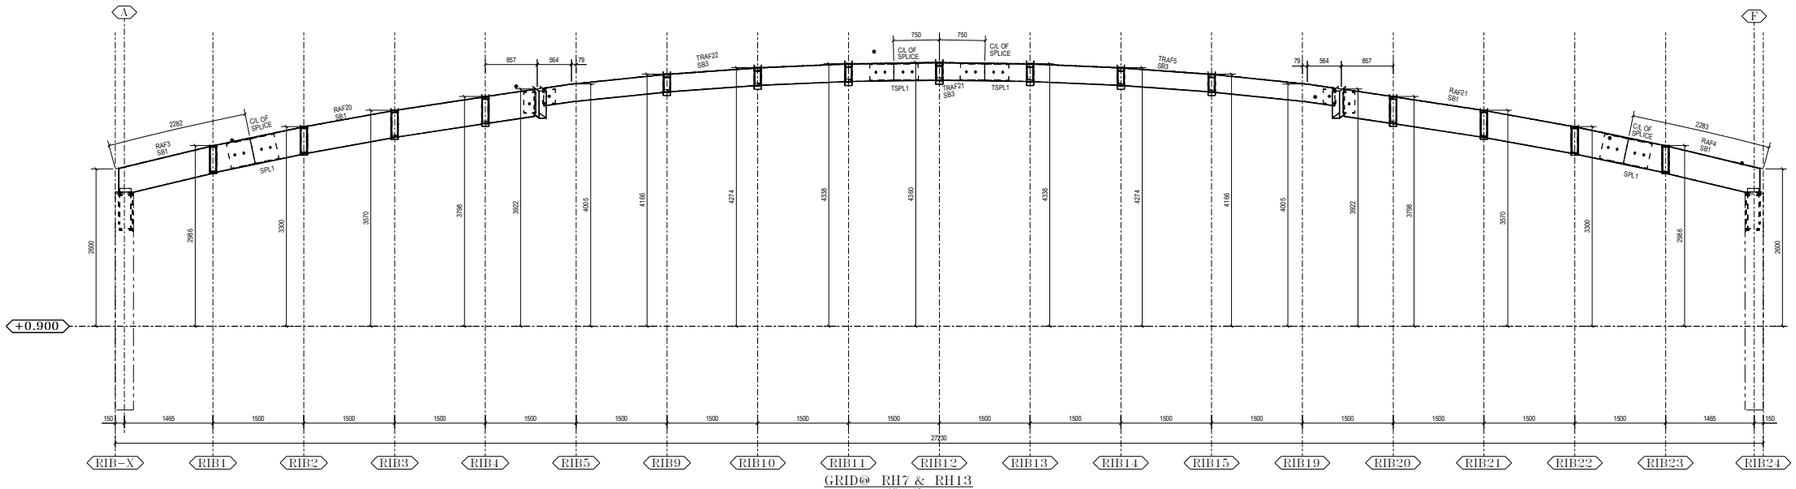



GRID@ RH7 & RH13
SCALE- 1:35

GENERAL NOTES :

1. ALL DIMENSIONS ARE IN MM.
2. GRADE OF STEEL SHALL BE FE-500D CONFORMING TO IS1786 - 2008.
3. DO NOT SCALE THE DRAWING, ONLY WRITTEN DIMENSIONS TO BE FOLLOWED.
4. ANY DISCREPANCY IN THE DWG TO BE BROUGHT TO THE NOTICE OF THE CONSULTANT BEFORE EXECUTION.
5. FOR ALL LEVELS AND DIMENSIONS REFER ARCH DRAWINGS.
6. ALL LEVELS & DIMENSIONS TO BE CONFIRMED AT SITE BEFORE EXECUTION.
7. ALL LEVELS TO BE CO-ORDINATED & RECONFIRMED WITH ARCHITECTURAL DRAWINGS.
8. ALL TRENCH SIZES INSERT SLEEVES & CUTOUTS TO BE CO-ORDINATED & RECONFIRMED WITH ARCHITECTURAL & MEP DRAWINGS.
9. ALL SHOP AND SITE WELDS ARE 8mm FILLET MIN. U.N.O.
10. CHECK ALL DIMENSIONS BEFORE FABRICATION OF STRUCTURAL STEEL WORK.
11. GRADE OF STEEL YST-250.
12. ⊕ INDICATES ORIENTATION MARK.

DIRECTION

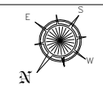


CONTRACTOR-

Let's Succeed Together!
UNIVASTU INDIA LTD

UNIVASTU INDIA PVT LTD
PUNE (INDIA) 411038


PROJECT NO.

| | |
|---|---|
| PROJECT: | SHRI. MANOHAR PARRIKAR SMRITI STHAL |
| CLIENT: | GENERAL ADMINISTRATIVE DEPARTMENT,GOA |
| ARCHITECT: | UCJ ARCHITECTURE & ENVIRONMENT |
| STRUCTURAL ENGG.: | SHANGHAVI & ASSOCIATES CONSULTANTS Pvt. Ltd. |
| DRAWING TITLE: | ELEVATION ALONG GRID RH5, RH6, RH7 & RH13 |

| | DATE | INITIALS | SIGN. | SCALE | ORIG.SIZE | TOTAL PAGES |
|---|---|---|---|---|---|---|
| DRAWN | 04.09.2021 | VISHWATECH | | 1:35 | 841X1189 | 1 |
| CHECKED | 04.09.2021 | SG | | DWG NO.: | PAGE | REV. |
| ENGINEER | 04.09.2021 | SG | | GSS--ST--GA--104 | 1 | 0 |
| APPROVED | 04.09.2021 | SG | | | | |


CONSULTER FOR WORK CONSULTER FOR LOCATION

SHEET SIZE- A0

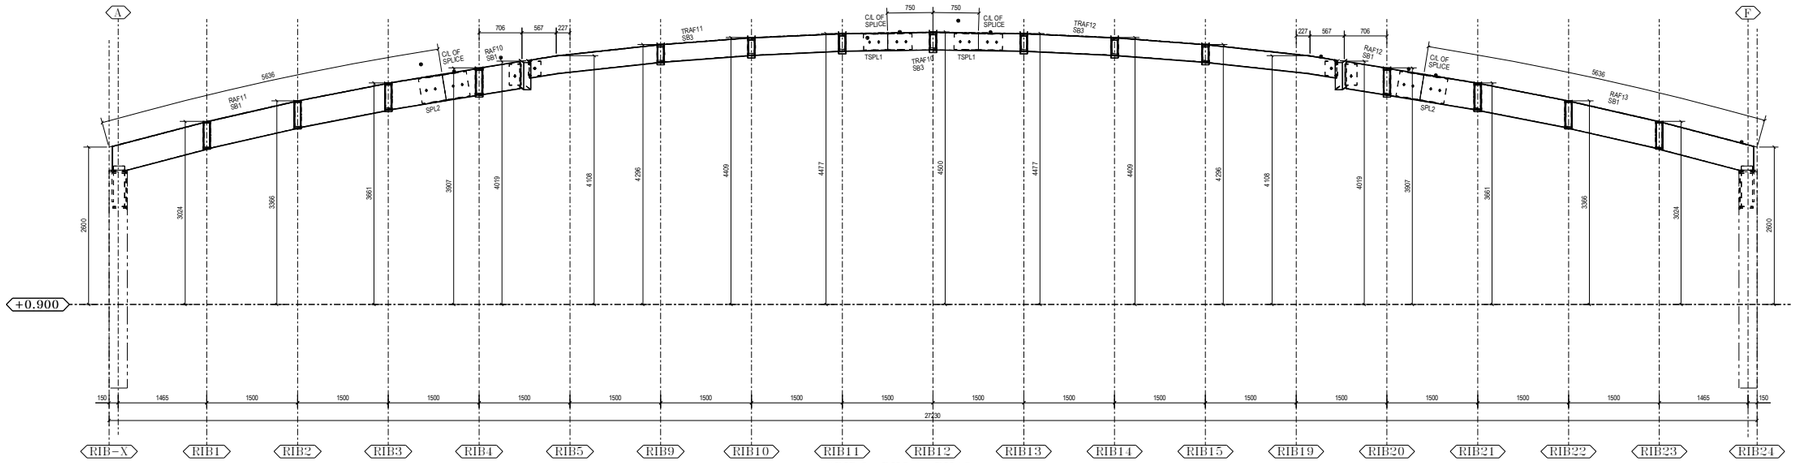



GRID@ RIB & RIB12

SCALE- 1:35

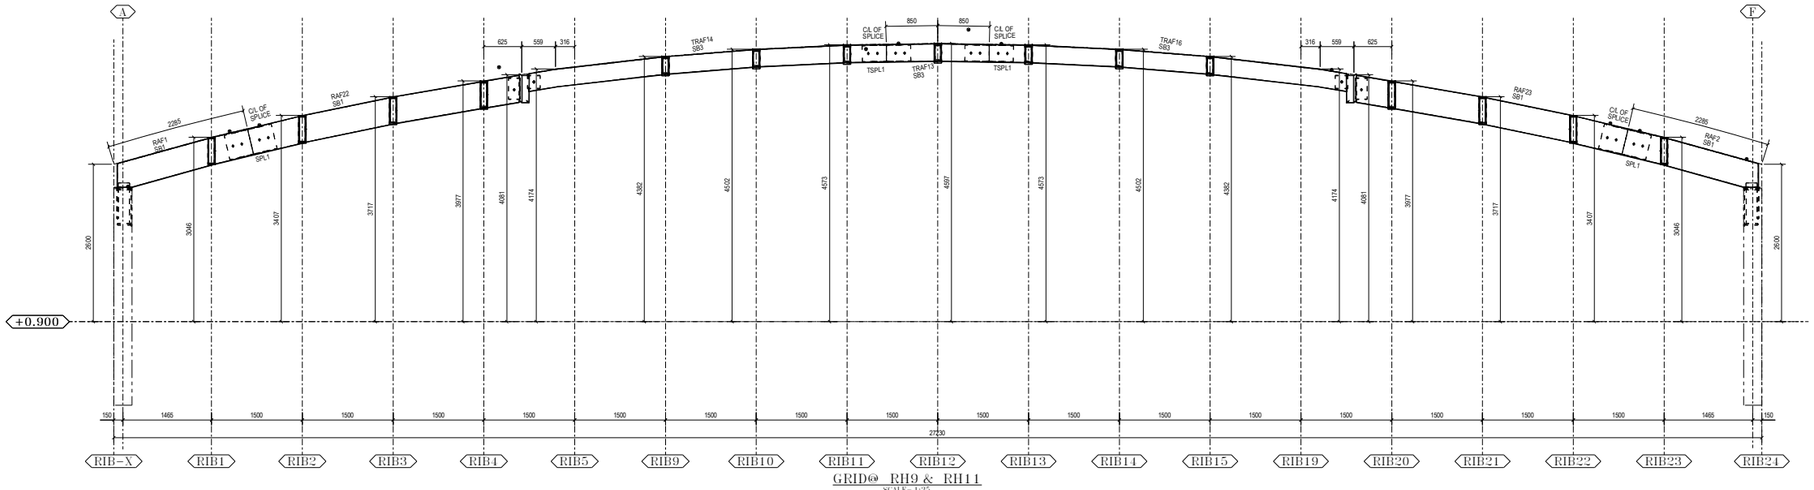


GRID@ RIB & RIB11

SCALE- 1:35

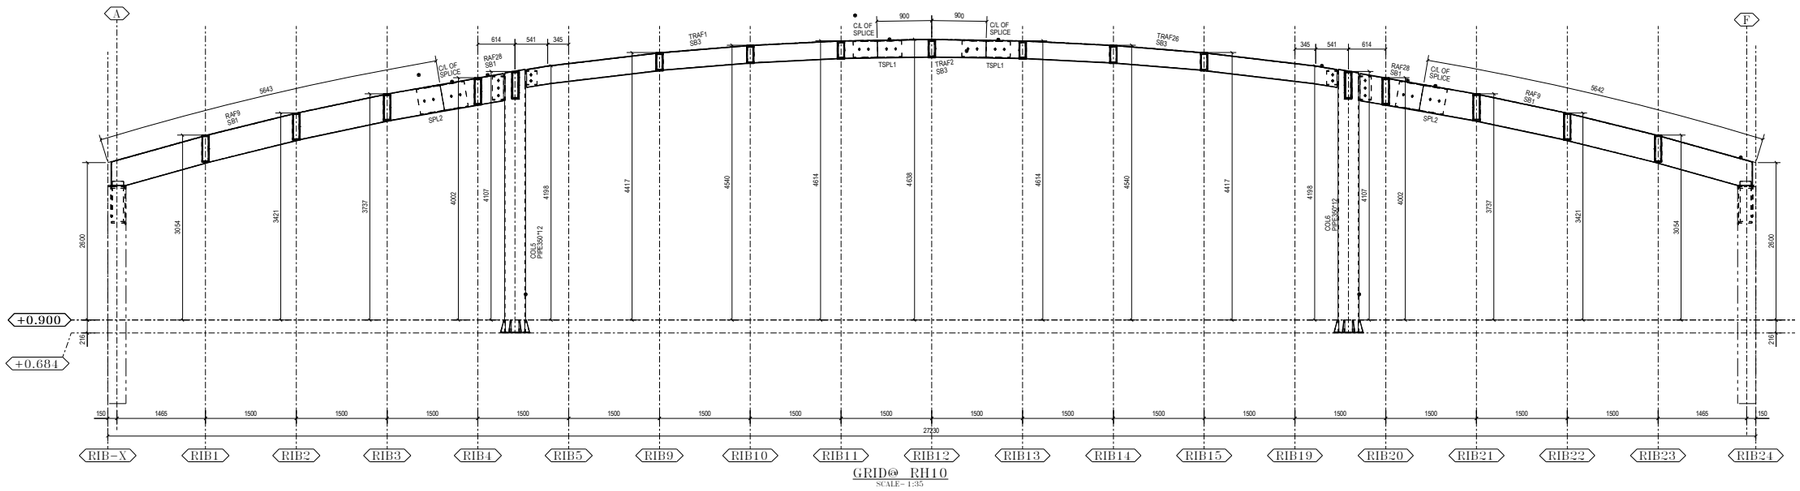



GRID@ RIB10

SCALE- 1:35

GENERAL NOTES :

1. ALL DIMENSIONS ARE IN MM.
2. GRADE OF STEEL SHALL BE FE-500D CONFORMING TO IS1786 - 2008.
3. DO NOT SCALE THE DRAWING, ONLY WRITTEN DIMENSIONS TO BE FOLLOWED.
4. ANY DISCREPANCY IN THE DWG TO BE BROUGHT TO THE NOTICE OF THE CONSULTANT BEFORE EXECUTION.
5. FOR ALL LEVELS AND DIMENSIONS REFER ARCH DRAWINGS.
6. ALL LEVELS & DIMENSIONS TO BE CONFIRMED AT SITE BEFORE EXECUTION.
7. ALL LEVELS TO BE CO-ORDINATED & RECONFIRMED WITH ARCHITECTURAL DRAWINGS.
8. ALL TRENCH SIZES INSERT SLEEVES & CUTOUTS TO BE CO-ORDINATED & RECONFIRMED WITH ARCHITECTURAL & MEP DRAWINGS.
9. ALL SHOP AND SITE WELDS ARE 6mm FILLET MIN. U.N.O.
10. CHECK ALL DIMENSIONS BEFORE FABRICATION OF STRUCTURAL STEEL WORK.
11. GRADE OF STEEL YST-250.
12. ⊕ INDICATES ORIENTATION MARK.

DIRECTION

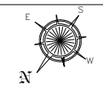


CONTRACTOR-

UNIVASTU INDIA LTD

Let's Succeed Together!

UNIVASTU INDIA PVT LTD
PUNE (INDIA) 411038


PROJECT NO.

| | |
|---|---|
| PROJECT: | SHRI. MANOHAR PARRIKAR SMRITI STHAL |
| CLIENT: | GENERAL ADMINISTRATIVE DEPARTMENT,GOA |
| ARCHITECT: | UCJ ARCHITECTURE & ENVIRONMENT |
| STRUCTURAL ENGG.: | SHANGHAVI & ASSOCIATES CONSULTANTS Pvt. Ltd. |
| DRAWING TITLE: | ELEVATION ALONG GRID RIB TO RIB12 |

| | DATE | INITIALS | SIGN. | SCALE | ORIG.SIZE | TOTAL PAGES |
|---|---|---|---|---|---|---|
| DRAWN | 04.09.2021 | VISHWATECH | | 1:35 | A4/A1/A0 | 1 |
| CHECKED | 04.09.2021 | SG | | DWG NO : GSS-ST-GA-105 | PAGE 1 | REV. 0 |
| ENGINEER | 04.09.2021 | SG | | | | |
| APPROVED | 04.09.2021 | SG | | | | |


COMPUTER FILE NAME : COMPUTER FILE LOCATION :

SHEET SIZE- A0

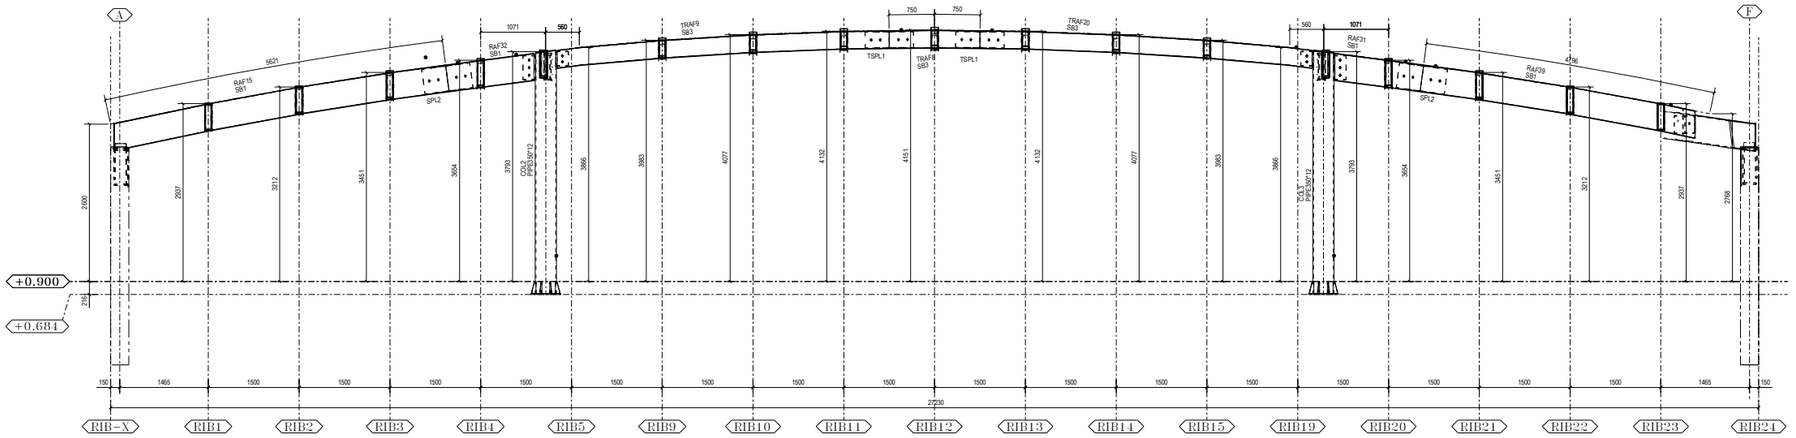



GRID@ RH14

SCALE- 1:35

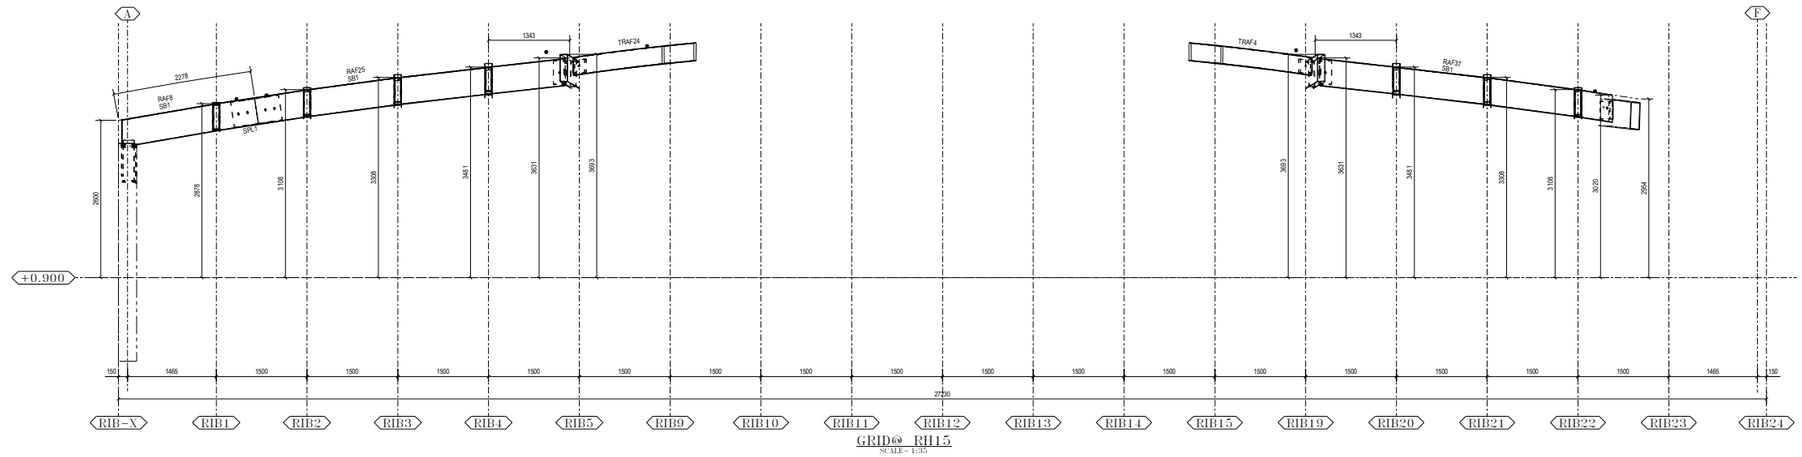


GRID@ RH15

SCALE- 1:35

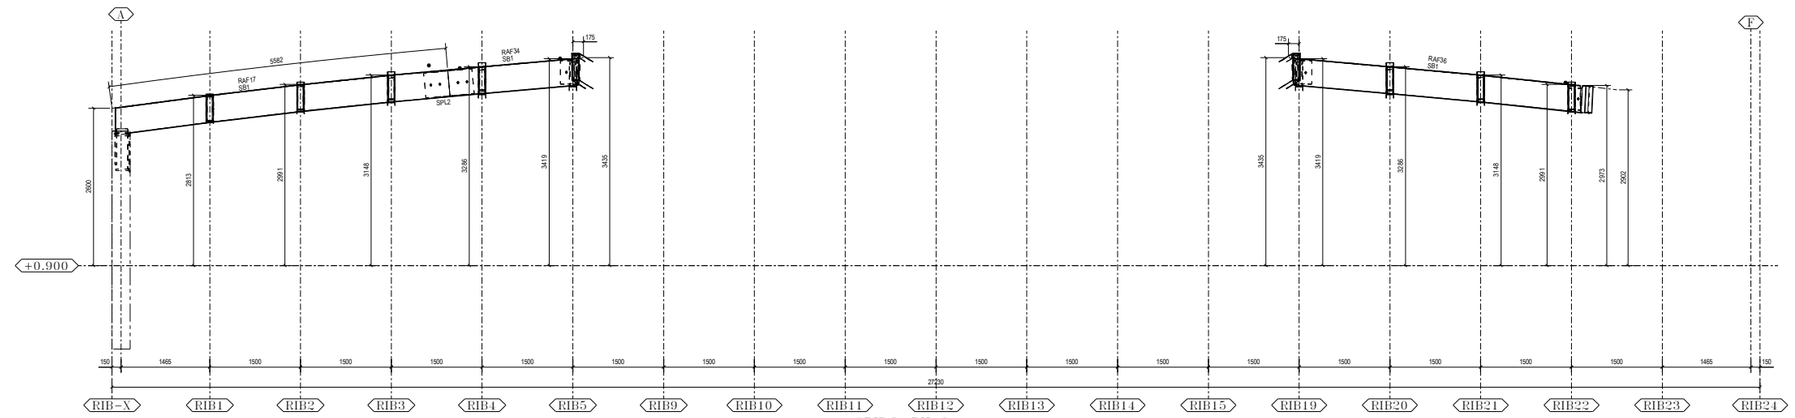



GRID@ RH16

SCALE- 1:35

GENERAL NOTES :

1. ALL DIMENSIONS ARE IN MM.
2. GRADE OF STEEL SHALL BE FE-500D CONFORMING TO IS1786 - 2008.
3. DO NOT SCALE THE DRAWING, ONLY WRITTEN DIMENSIONS TO BE FOLLOWED.
4. ANY DISCREPANCY IN THE DWG TO BE BROUGHT TO THE NOTICE OF THE CONSULTANT BEFORE EXECUTION.
5. FOR ALL LEVELS AND DIMENSIONS REFER ARCH DRAWINGS.
6. ALL LEVELS & DIMENSIONS TO BE CONFIRMED AT SITE BEFORE EXECUTION.
7. ALL LEVELS TO BE CO-ORDINATED & RECONFIRMED WITH ARCHITECTURAL DRAWINGS.
8. ALL TRENCH SIZES INSERT SLEEVES & CUTOUTS TO BE CO-ORDINATED & RECONFIRMED WITH ARCHITECTURAL & MEP DRAWINGS.
9. ALL SHOP AND SITE WELDS ARE 8mm FILLET MIN. U.N.O.
10. CHECK ALL DIMENSIONS BEFORE FABRICATION OF STRUCTURAL STEEL WORK.
11. GRADE OF STEEL YST-250.
12. ⬟ INDICATES ORIENTATION MARK.

DIRECTION

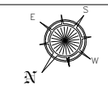


CONTRACTOR-

Let's Succeed Together!

UNIVASTU INDIA LTD

UNIVASTU INDIA PVT LTD
PUNE (INDIA) 411038


PROJECT NO.

| | |
|---|---|
| PROJECT: | SHRI. MANOHAR PARRIKAR SMRITI STHAL |
| CLIENT: | GENERAL ADMINISTRATIVE DEPARTMENT,GOA |
| ARCHITECT: | UCJ ARCHITECTURE & ENVIRONMENT |
| STRUCTURAL ENGG. | SHANGHAVI & ASSOCIATES CONSULTANTS Pvt. Ltd. |
| DRAWING TITLE: | ELEVATION ALONG GRID RH14, RH15 & RH16 |

| | DATE | INITIALS | SIGN. | SCALE | ORIG.SIZE | TOTAL PAGES |
|---|---|---|---|---|---|---|
| DRAWN | 04.09.2021 | VISHWATECH | | 1:35 | A4/A1/1IB | 1 |
| CHECKED | 04.09.2021 | SG | | DWG NO : | | PAGE / REV. |
| ENGINEER | 04.09.2021 | SG | | GSS-ST-GA-106 | | 1 / 0 |
| APPROVED | 04.09.2021 | SG | | | | |

CONSULTER FILE NAME:- CONSULTER FILE LOCATION:-

SHEET SIZE-A0

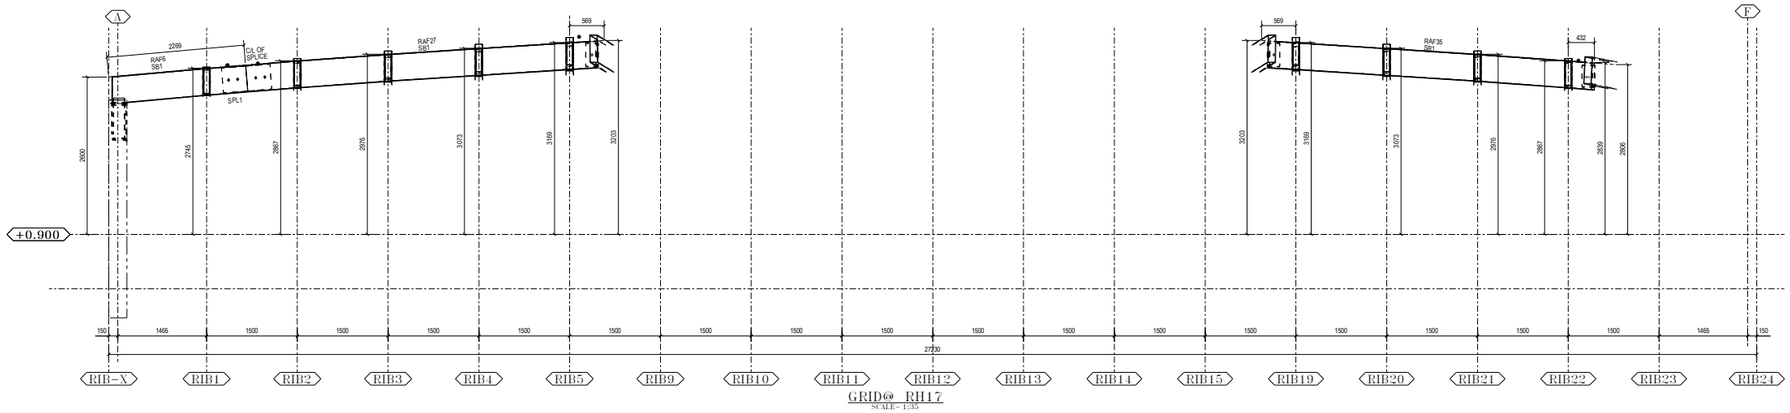


GRID@ RH17

SCALE- 1:35





GRID@ RH18

SCALE- 1:35

GENERAL NOTES :

1. ALL DIMENSIONS ARE IN MM.
2. GRADE OF STEEL SHALL BE FE-500D CONFORMING TO IS1786 - 2008.
3. DO NOT SCALE THE DRAWING, ONLY WRITTEN DIMENSIONS TO BE FOLLOWED.
4. ANY DISCREPANCY IN THE DWG TO BE BROUGHT TO THE NOTICE OF THE CONSULTANT BEFORE EXECUTION.
5. FOR ALL LEVELS AND DIMENSIONS REFER ARCH DRAWINGS.
6. ALL LEVELS & DIMENSIONS TO BE CONFIRMED AT SITE BEFORE EXECUTION.
7. ALL LEVELS TO BE CO-ORDINATED & RECONFIRMED WITH ARCHITECTURAL DRAWINGS.
8. ALL TRENCH SIZES INSERT SLEEVES & CUTOUTS TO BE CO-ORDINATED & RECONFIRMED WITH ARCHITECTURAL & MEP DRAWINGS.
9. ALL SHOP AND SITE WELDS ARE 8mm FILLET MIN. U.N.O.
10. CHECK ALL DIMENSIONS BEFORE FABRICATION OF STRUCTURAL STEEL WORK.
11. GRADE OF STEEL YST-250.
12. ⬟ INDICATES ORIENTATION MARK.

DIRECTION

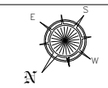


CONTRACTOR-

Let's Succeed Together!
UNIVASTU INDIA LTD

UNIVASTU INDIA PVT LTD
PUNE (INDIA) 411038

PROJECT NO.

| | |
|---|---|
| PROJECT: | SHRI. MANOHAR PARRIKAR SMRITI STHAL |
| CLIENT: | GENERAL ADMINISTRATIVE DEPARTMENT,GOA |
| ARCHITECT: | UCJ ARCHITECTURE & ENVIRONMENT |
| STRUCTURAL ENGG.: | SHANGHAVI & ASSOCIATES CONSULTANTS Pvt. Ltd. |
| DRAWING TITLE: | ELEVATION ALONG GRID RH17 & RH18 |

| | DATE | INITIALS | SIGN. |
|---|---|---|---|
| DRAWN | 04.09.2021 | VISHWATECH | |
| CHECKED | 04.09.2021 | SG | |
| ENGINEER | 04.09.2021 | SG | |
| APPROVED | 04.09.2021 | SG | |


| SCALE | ORIG.SIZE | TOTAL PAGES |
|---|---|---|
| 1:35 | 841X119 | 1 |

DWG NO : GSS-ST-GA-107

| PAGE | REV. |
|---|---|
| 1 | 0 |


CONSTR.FAC.NUMBER CONSTR.FAC.LOCATION

SHEET SIZE- A0

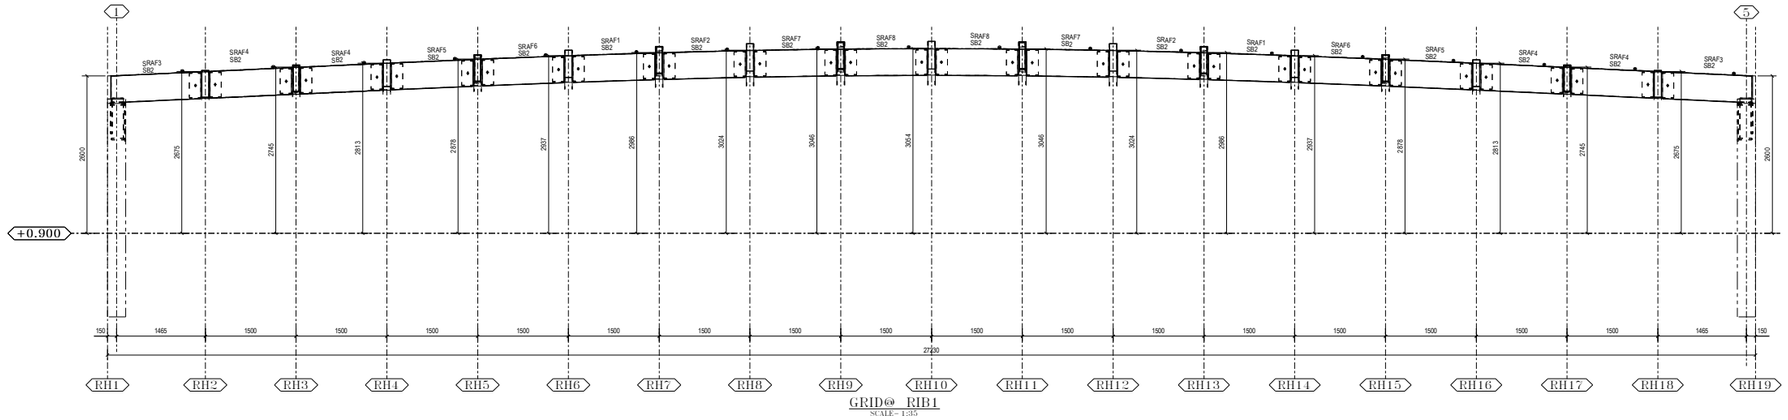



GRID@ RIB1

SCALE- 1:35

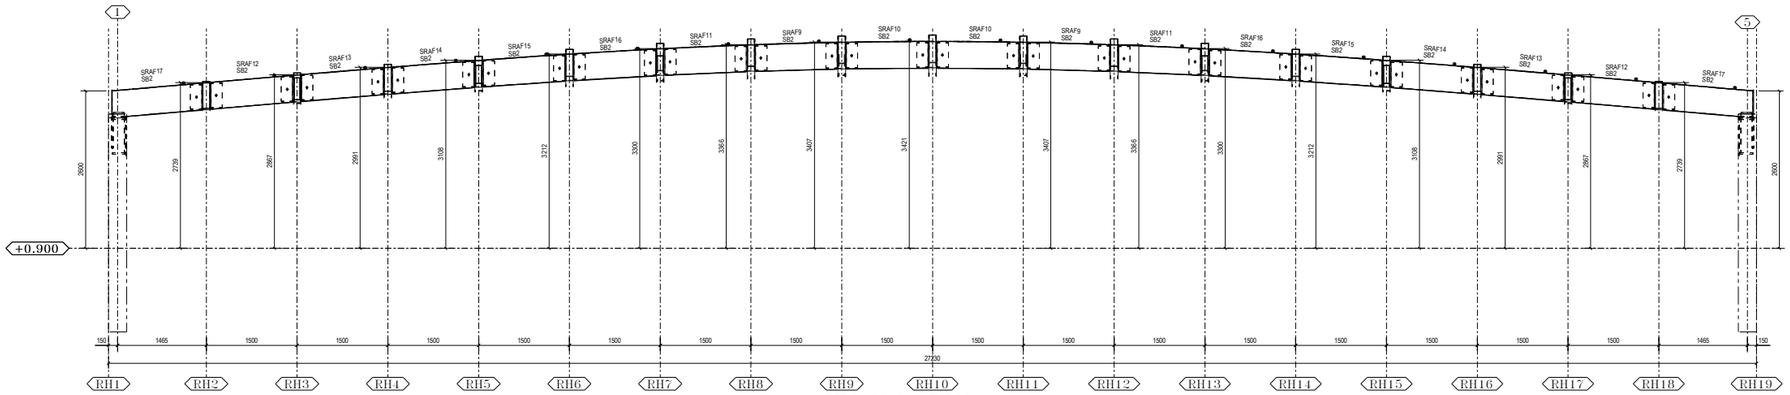


GRID@ RIB2 & RIB22

SCALE- 1:35

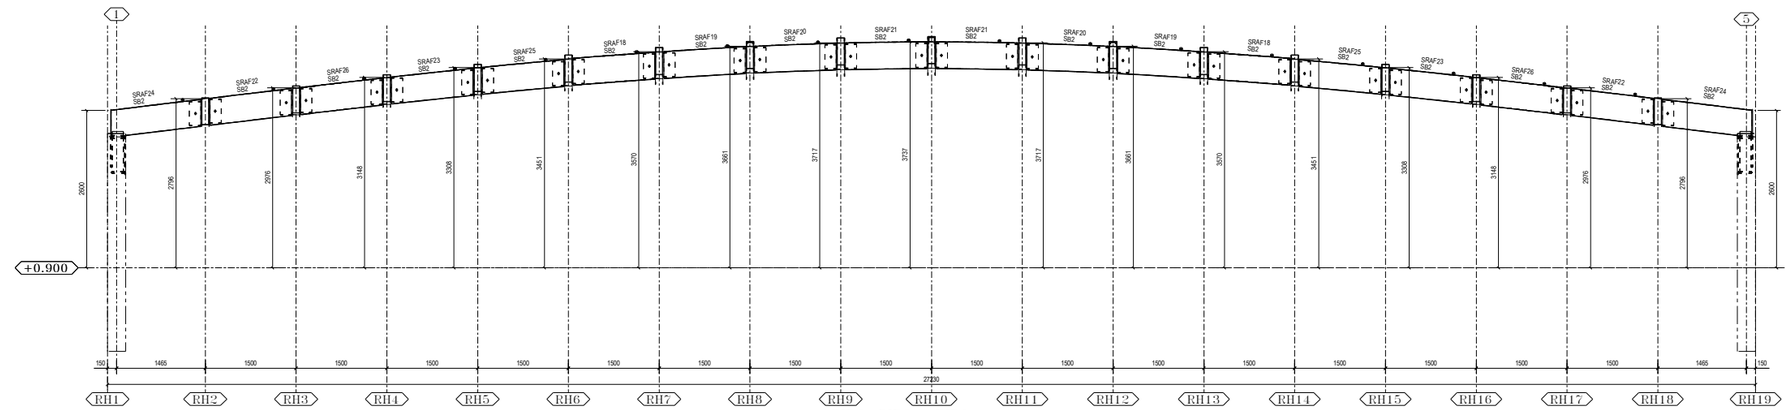



GRID@ RIB3 & RIB21

SCALE- 1:35

GENERAL NOTES :

1. ALL DIMENSIONS ARE IN MM.
2. GRADE OF STEEL SHALL BE FE-500D CONFORMING TO IS1786 - 2008.
3. DO NOT SCALE THE DRAWING, ONLY WRITTEN DIMENSIONS TO BE FOLLOWED.
4. ANY DISCREPANCY IN THE DWG TO BE BROUGHT TO THE NOTICE OF THE CONSULTANT BEFORE EXECUTION.
5. FOR ALL LEVELS AND DIMENSIONS REFER ARCH DRAWINGS.
6. ALL LEVELS & DIMENSIONS TO BE CONFIRMED AT SITE BEFORE EXECUTION.
7. ALL LEVELS TO BE CO-ORDINATED & RECONFIRMED WITH ARCHITECTURAL DRAWINGS.
8. ALL TRENCH SIZES INSERT SLEEVES & CUTOUTS TO BE CO-ORDINATED & RECONFIRMED WITH ARCHITECTURAL & MEP DRAWINGS.
9. ALL SHOP AND SITE WELDS ARE 8mm FILLET MIN. U.N.O.
10. CHECK ALL DIMENSIONS BEFORE FABRICATION OF STRUCTURAL STEEL WORK.
11. GRADE OF STEEL YST-250.
12. ⊕ INDICATES ORIENTATION MARK.

DIRECTION

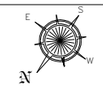


CONTRACTOR-

UNIVASTU INDIA PVT LTD
PUNE (INDIA) 411038

PROJECT NO:

| | |
|---|---|
| PROJECT: | SHRI. MANOHAR PARRIKAR SMRITI STHAL |
| CLIENT: | GENERAL ADMINISTRATIVE DEPARTMENT,GOA |
| ARCHITECT: | UCJ ARCHITECTURE & ENVIRONMENT |
| STRUCTURAL ENGG.: | SHANGHAVI & ASSOCIATES CONSULTANTS Pvt. Ltd. |
| DRAWING TITLE: | ELEVATION ALONG GRID RIB1, RIB2, RIB3, RIB21 & RIB22 |


| | DATE | INITIALS | SIGN. |
|---|---|---|---|
| DRAWN | 04.09.2021 | VISHWARCH | |
| CHECKED | 04.09.2021 | SG | |
| ENGINEER | 04.09.2021 | SG | |
| APPROVED | 04.09.2021 | SG | |

| SCALE | ORIG.SIZE | TOTAL PAGES |
|---|---|---|
| 1:35 | A4/A1/A0 | 1 |


DWG NO.: GSS-ST-GA-108

| PAGE | REV. |
|---|---|
| 1 | 0 |


SHEET SIZE- A0

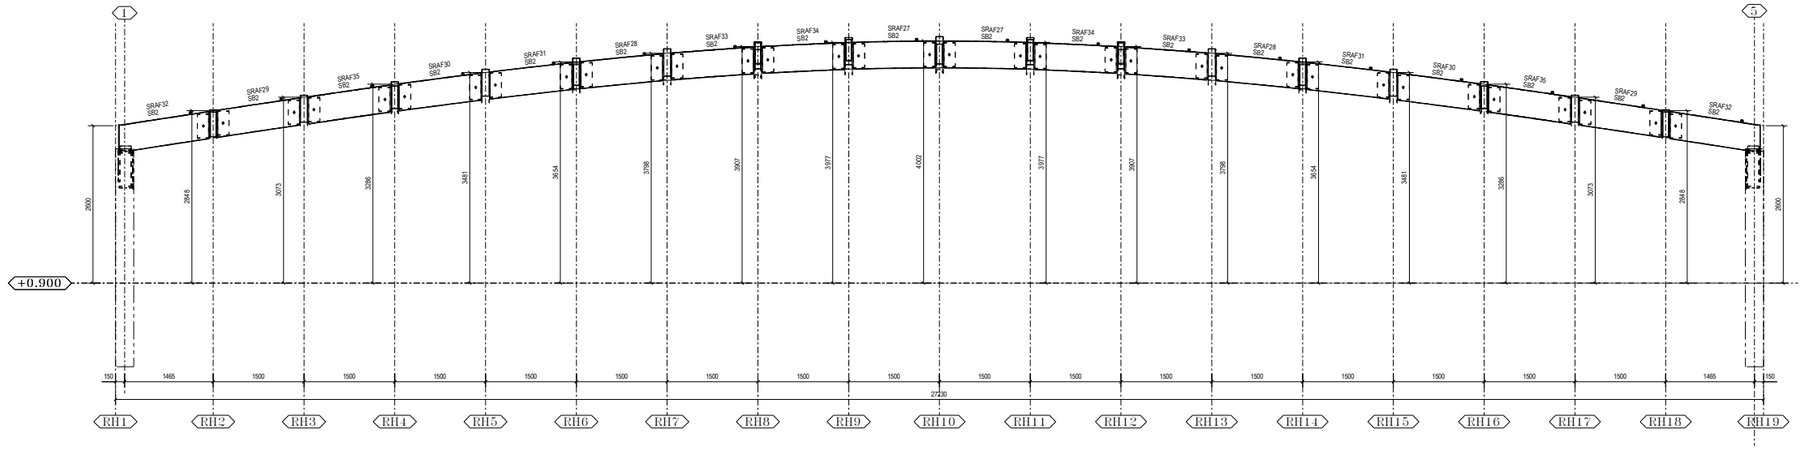


GRID@ RIB4 & RIB20
SCALE- 1:35

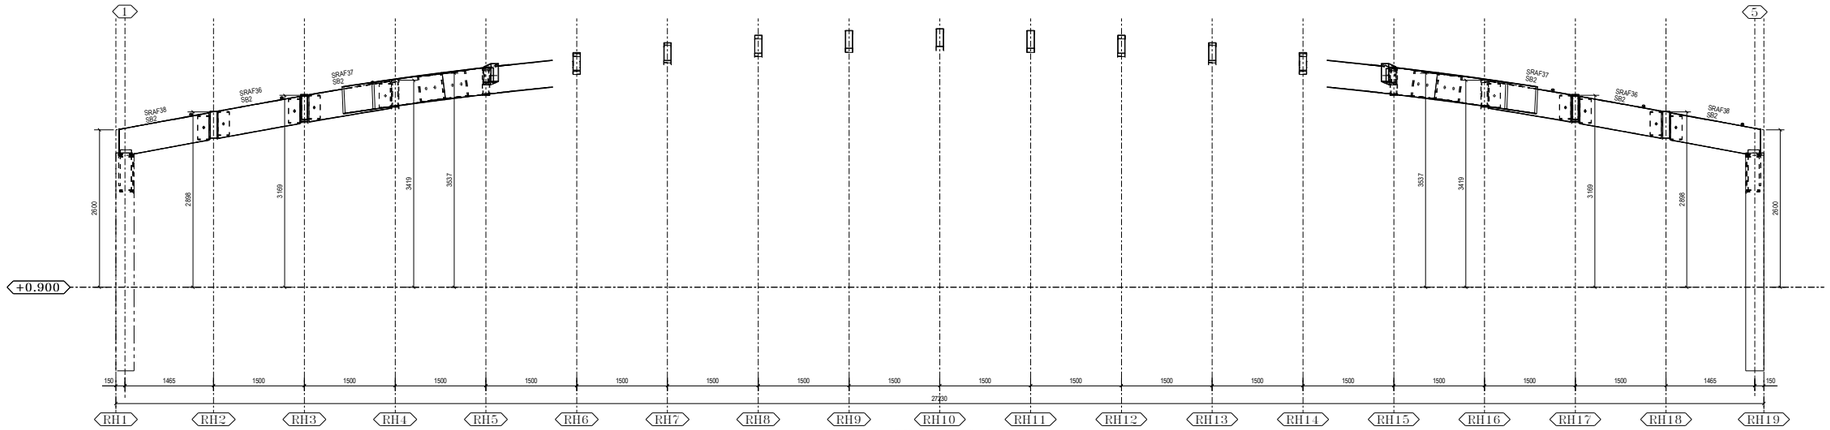


GRID@ RIB5 & RIB19
SCALE- 1:35

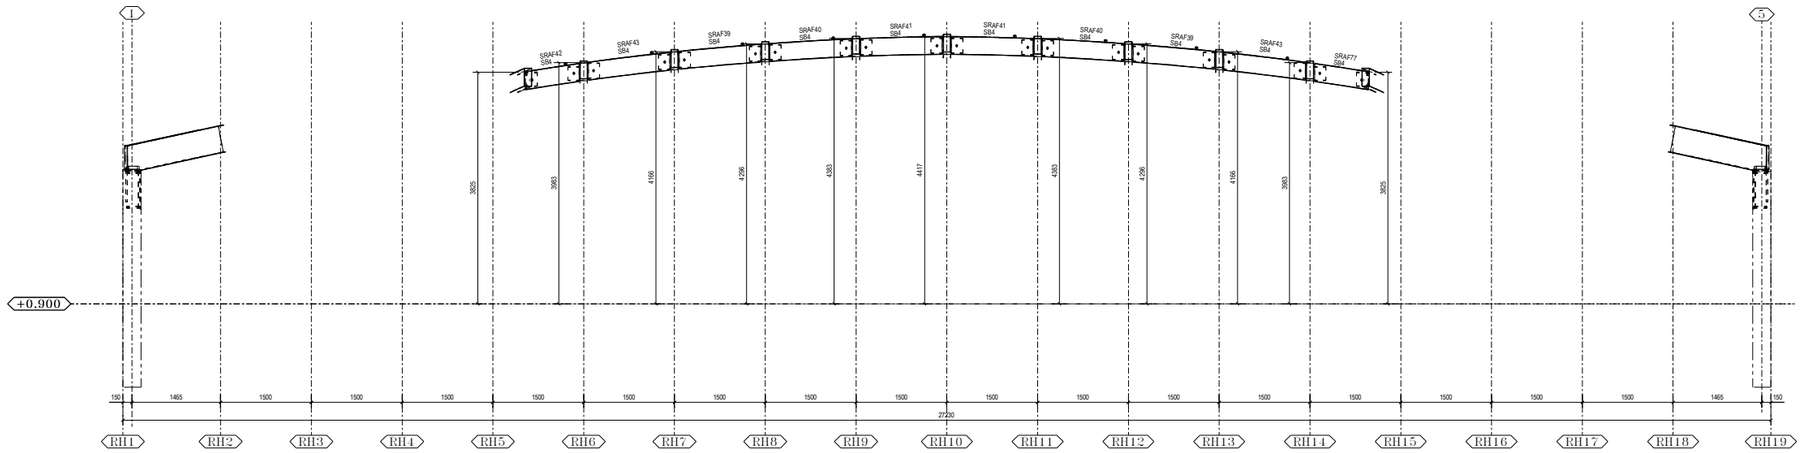



GRID@ RIB9 & RIB15
SCALE- 1:35

GENERAL NOTES :

1. ALL DIMENSIONS ARE IN MM.
2. GRADE OF STEEL SHALL BE FE-500D CONFORMING TO IS1786 - 2008.
3. DO NOT SCALE THE DRAWING, ONLY WRITTEN DIMENSIONS TO BE FOLLOWED.
4. ANY DISCREPANCY IN THE DWG TO BE BROUGHT TO THE NOTICE OF THE CONSULTANT BEFORE EXECUTION.
5. FOR ALL LEVELS AND DIMENSIONS REFER ARCH DRAWINGS.
6. ALL LEVELS & DIMENSIONS TO BE CONFIRMED AT SITE BEFORE EXECUTION.
7. ALL LEVELS TO BE CO-ORDINATED & RECONFIRMED WITH ARCHITECTURAL DRAWINGS.
8. ALL TRENCH SIZES INSERT SLEEVES & CUTOUTS TO BE CO-ORDINATED & RECONFIRMED WITH ARCHITECTURAL & MEP DRAWINGS.
9. ALL SHOP AND SITE WELDS ARE 8mm FILLET MIN. U.N.O.
10. CHECK ALL DIMENSIONS BEFORE FABRICATION OF STRUCTURAL STEEL WORK.
11. GRADE OF STEEL YST-250.
12. ⬟ INDICATES ORIENTATION MARK.

DIRECTION

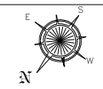


CONTRACTOR-

Let's Succeed Together!
UNIVASTU INDIA LTD

UNIVASTU INDIA PVT LTD
PUNE (INDIA) 411038


PROJECT NO.

| | |
|---|---|
| PROJECT: | SHRI. MANOHAR PARRIKAR SMRITI STHAL |
| CLIENT: | GENERAL ADMINISTRATIVE DEPARTMENT,GOA |
| ARCHITECT: | UCJ ARCHITECTURE & ENVIRONMENT |
| STRUCTURAL ENGG.: | SHANGHAVI & ASSOCIATES CONSULTANTS Pvt. Ltd. |
| DRAWING TITLE: | ELEVATION ALONG GRID RIB4, RIB5, RIB9, RIB15, RIB19 & RIB20 |

| | DATE | INITIALS | SIGN. | SCALE | ORIG.SIZE | TOTAL PAGES |
|---|---|---|---|---|---|---|
| DRAWN | 04.09.2021 | ASHWINTECH | | 1:35 | A4/A1/A0 | 1 |
| CHECKED | 04.09.2021 | SG | | DWG NO : | | PAGE / REV. |
| ENGINEER | 04.09.2021 | SG | | GSS-ST-GA-109 | | 1 / 0 |
| APPROVED | 04.09.2021 | SG | | | | |


COMPUTER FILE NAME :- COMPUTER FILE LOCATION :-

SHEET SIZE-A0

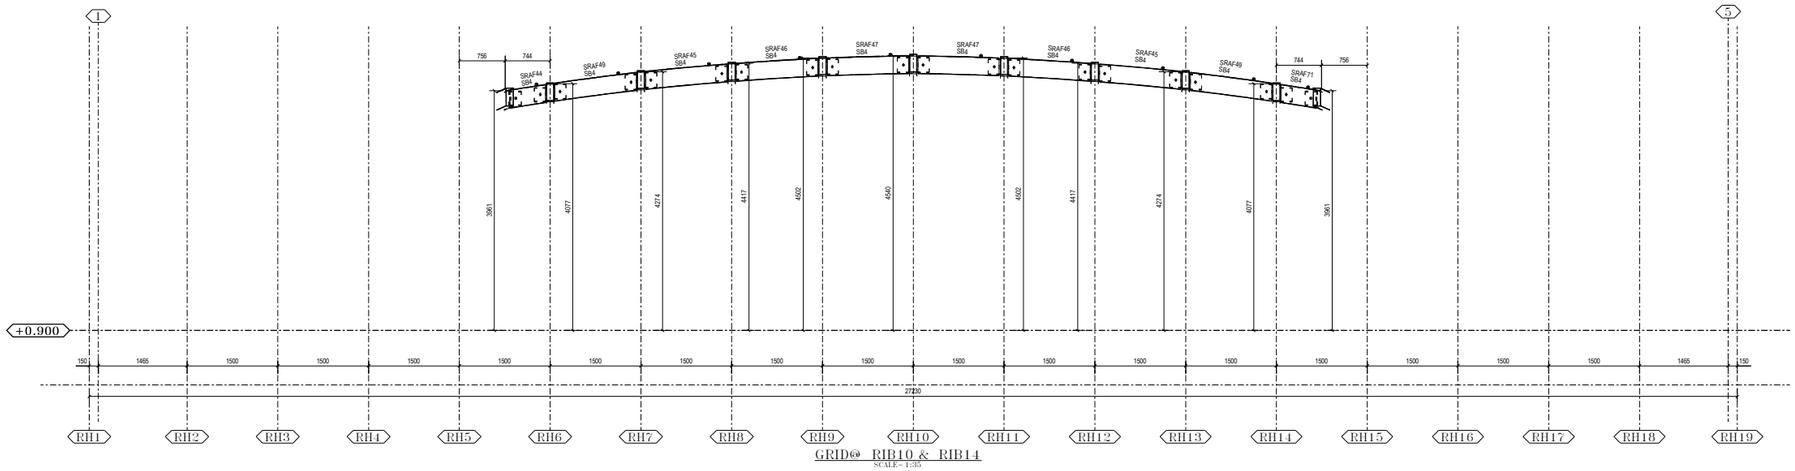



GRID@ RIB10 & RIB14

SCALE- 1:35

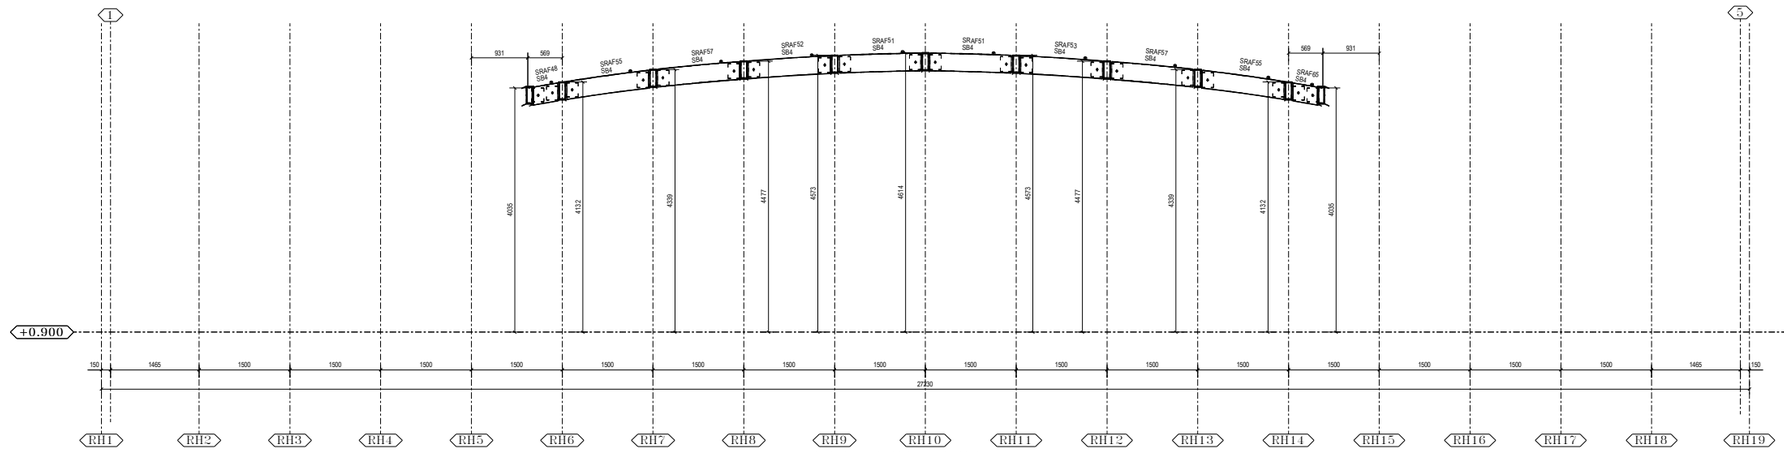


GRID@ RIB11 & RIB13

SCALE- 1:35

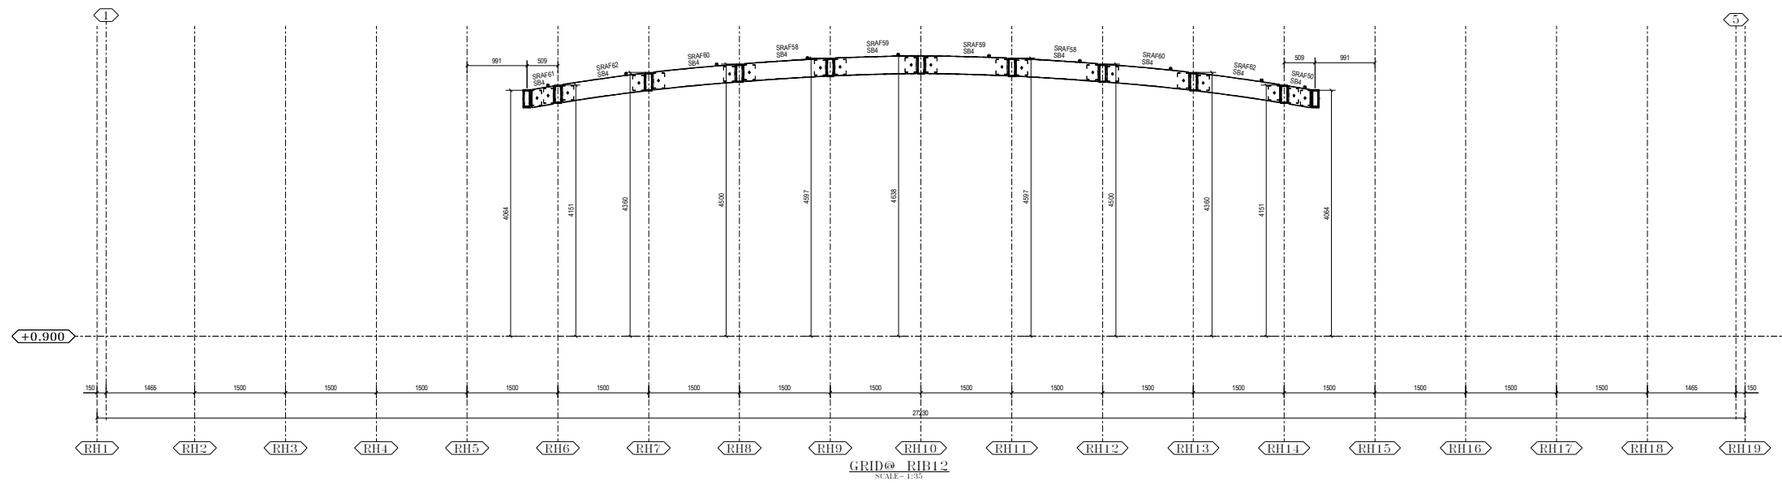



GRID@ RIB12

SCALE- 1:35

GENERAL NOTES :

1. ALL DIMENSIONS ARE IN MM.
2. GRADE OF STEEL SHALL BE FE-500D CONFORMING TO IS1786 - 2008.
3. DO NOT SCALE THE DRAWING, ONLY WRITTEN DIMENSIONS TO BE FOLLOWED.
4. ANY DISCREPANCY IN THE DWG TO BE BROUGHT TO THE NOTICE OF THE CONSULTANT BEFORE EXECUTION.
5. FOR ALL LEVELS AND DIMENSIONS REFER ARCH DRAWINGS.
6. ALL LEVELS & DIMENSIONS TO BE CONFIRMED AT SITE BEFORE EXECUTION.
7. ALL LEVELS TO BE CO-ORDINATED & RECONFIRMED WITH ARCHITECTURAL DRAWINGS.
8. ALL TRENCH SIZES INSERT SLEEVES & CUTOUTS TO BE CO-ORDINATED & RECONFIRMED WITH ARCHITECTURAL & MEP DRAWINGS.
9. ALL SHOP AND SITE WELDS ARE 8mm FILLET MIN. U.N.O.
10. CHECK ALL DIMENSIONS BEFORE FABRICATION OF STRUCTURAL STEEL WORK.
11. GRADE OF STEEL YST-250.
12. ❁ INDICATES ORIENTATION MARK.

DIRECTION

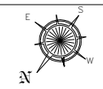


CONTRACTOR-

Let's Succeed Together!
UNIVASTU INDIA LTD

UNIVASTU INDIA PVT LTD
PUNE (INDIA) 411038

PROJECT NO.

| | |
|---|---|
| PROJECT: | SHRI. MANOHAR PARRIKAR SMRITI STHAL |
| CLIENT: | GENERAL ADMINISTRATIVE DEPARTMENT,GOA |
| ARCHITECT: | UCJ ARCHITECTURE & ENVIRONMENT |
| STRUCTURAL ENGG.: | SHANGHAVI & ASSOCIATES CONSULTANTS Pvt. Ltd. |
| DRAWING TITLE: | ELEVATION ALONG GRID RIB10 TO RIB14 |

| | DATE | INITIALS | SIGN. |
|---|---|---|---|
| DRAWN | 04.09.2021 | VISHWATECH | |
| CHECKED | 04.09.2021 | SG | |
| ENGINEER | 04.09.2021 | SG | |
| APPROVED | 04.09.2021 | SG | |


| SCALE | ORIG.SIZE | TOTAL PAGES |
|---|---|---|
| 1:25 | A4/A1/1189 | 1 |

DWG NO. GSS-ST-GA-110

PAGE 1 | REV. 0

CONSULTED FOR: CONSULTED FOR LOCATION:

SHEET SIZE-A1

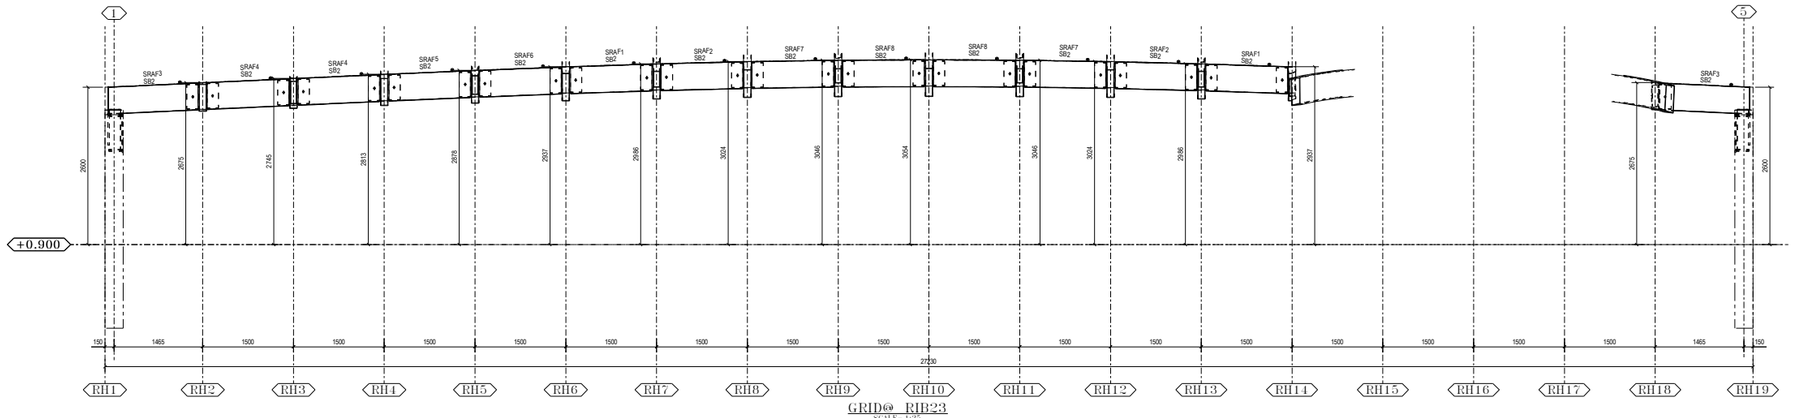



GRID@ RIB23

SCALE- 1:35

GENERAL NOTES :

1. ALL DIMENSIONS ARE IN MM.
2. GRADE OF STEEL SHALL BE FE-500D CONFORMING TO IS1786 - 2008.
3. DO NOT SCALE THE DRAWING, ONLY WRITTEN DIMENSIONS TO BE FOLLOWED.
4. ANY DISCREPANCY IN THE DWG TO BE BROUGHT TO THE NOTICE OF THE CONSULTANT BEFORE EXECUTION.
5. FOR ALL LEVELS AND DIMENSIONS REFER ARCH DRAWINGS.
6. ALL LEVELS & DIMENSIONS TO BE CONFIRMED AT SITE BEFORE EXECUTION.
7. ALL LEVELS TO BE CO-ORDINATED & RECONFIRMED WITH ARCHITECTURAL DRAWINGS.
8. ALL TRENCH SIZES INSERT SLEEVES & CUTOUTS TO BE CO-ORDINATED & RECONFIRMED WITH ARCHITECTURAL & MEP DRAWINGS.
9. ALL SHOP AND SITE WELDS ARE 8mm FILLET MIN. U.N.O.
10. CHECK ALL DIMENSIONS BEFORE FABRICATION OF STRUCTURAL STEEL WORK.
11. GRADE OF STEEL YST-250.
12. ⬟ INDICATES ORIENTATION MARK.

DIRECTION

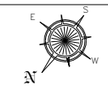


CONTRACTOR-

Let's Succeed Together!

UNIVASTU INDIA LTD

UNIVASTU INDIA PVT LTD
PUNE (INDIA) 411038

PROJECT NO.

| | |
|---|---|
| PROJECT: | SHRI. MANOHAR PARRIKAR SMRITI STHAL |
| CLIENT: | GENERAL ADMINISTRATIVE DEPARTMENT,GOA |
| ARCHITECT: | UCJ ARCHITECTURE & ENVIRONMENT |
| STRUCTURAL ENGG.: | SHANGHAVI & ASSOCIATES CONSULTANTS Pvt. Ltd. |
| DRAWING TITLE: | ELEVATION ALONG GRID RIB23 |


| | DATE | INITIALS | SIGN. |
|---|---|---|---|
| DRAWN | 04.09.2021 | VISHWATECH | |
| CHECKED | 04.09.2021 | SG | |
| ENGINEER | 04.09.2021 | SG | |
| APPROVED | 04.09.2021 | SG | |

SCALE: 1:35 | ORIG.SIZE: 841X1189 | TOTAL PAGES: 1

DWG NO.: GNS-ST-GA-111 | PAGE: 1 | REV.: 0

COMPUTER FILE NAME: | COMPUTER FILE LOCATION:

SHEET SIZE-A0

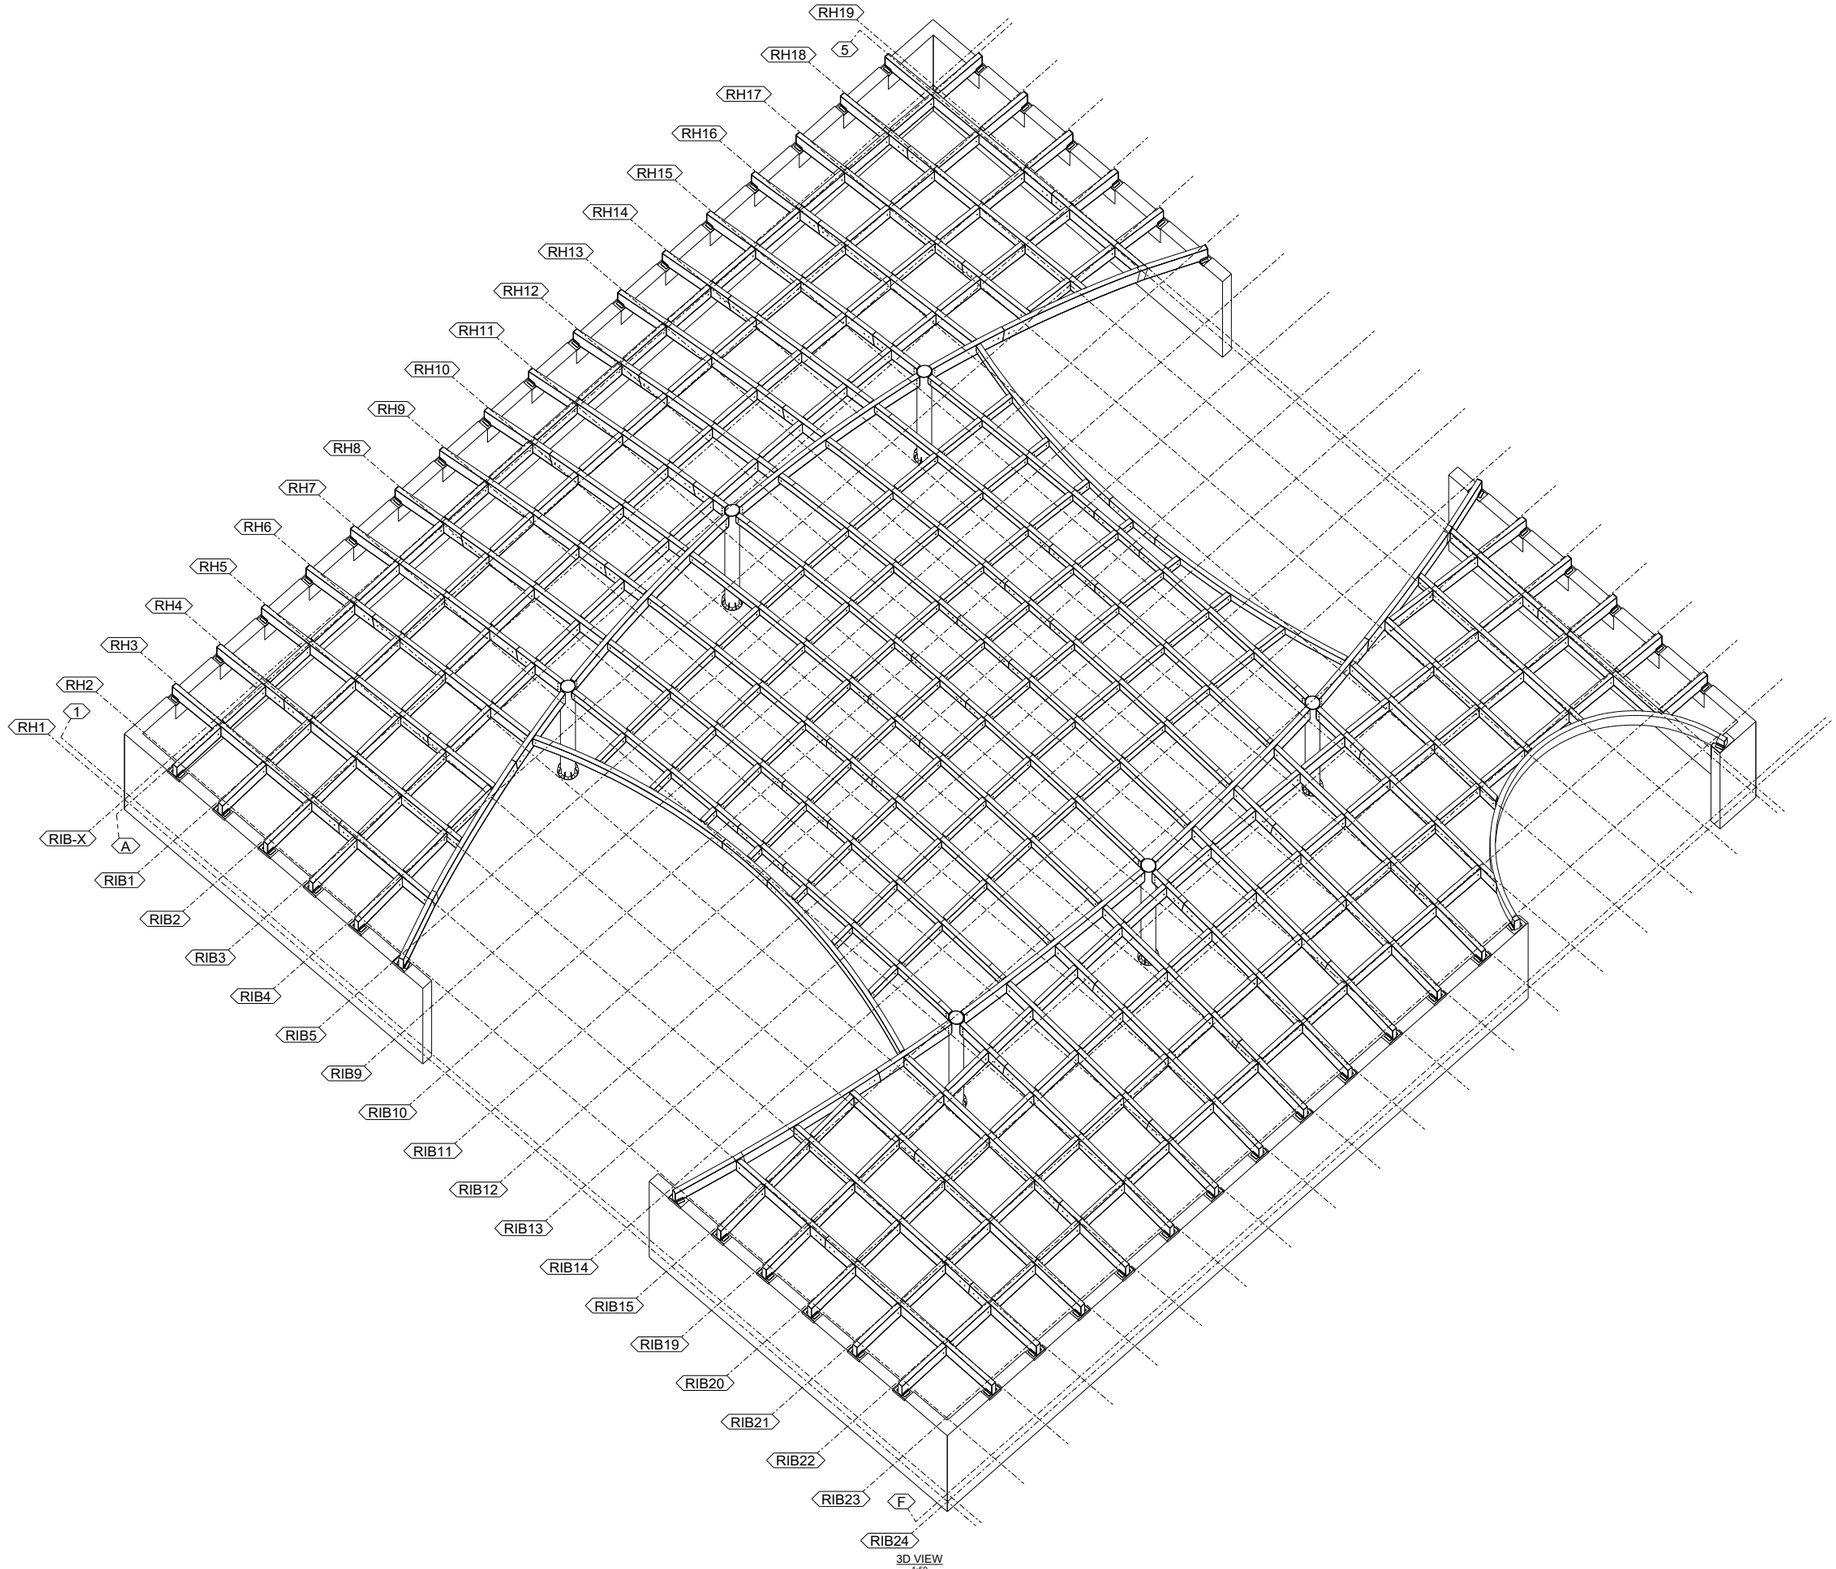



3D VIEW
1:50

GENERAL NOTES :

1. ALL DIMENSIONS ARE IN MM.
2. GRADE OF STEEL SHALL BE FE-500D CONFORMING TO IS1786 - 2008.
3. DO NOT SCALE THE DRAWING, ONLY WRITTEN DIMENSIONS TO BE FOLLOWED.
4. ANY DISCREPANCY IN THE DWG TO BE BROUGHT TO THE NOTICE OF THE CONSULTANT BEFORE EXECUTION.
5. FOR ALL LEVELS AND DIMENSIONS REFER ARCH DRAWINGS.
6. ALL LEVELS & DIMENSIONS TO BE CONFIRMED AT SITE BEFORE EXECUTION.
7. ALL LEVELS TO BE CO-ORDINATED & RECONFIRMED WITH ARCHITECTURAL DRAWINGS.
8. ALL TRENCH SIZES INSERT SLEEVES & CUTOUTS TO BE CO-ORDINATED & RECONFIRMED WITH ARCHITECTURAL & MEP DRAWINGS.
9. ALL SHOP AND SITE WELDS ARE 8mm FILLET MIN. U.N.O.
10. CHECK ALL DIMENSIONS BEFORE FABRICATION OF STRUCTURAL STEEL WORK.
11. GRADE OF STEEL YST-250.
12. ⬟ INDICATES ORIENTATION MARK.

DIRECTION

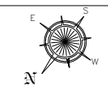


CONTRACTOR–

Let's Succeed Together!
UNIVASTU INDIA LTD

UNIVASTU INDIA PVT. LTD
PUNE (INDIA) 411038

PROJECT NO.

| | |
|---|---|
| PROJECT: | SHRI. MANOHAR PARRIKAR SMRITI STHAL |
| CLIENT: | GENERAL ADMINISTRATIVE DEPARTMENT,GOA |
| ARCHITECT: | UCJ ARCHITECTURE & ENVIRONMENT |
| STRUCTURAL ENGG.: | SHANGHAVI & ASSOCIATES CONSULTANTS Pvt. Ltd. |
| DRAWING TITLE: | 3D VIEW |

| | DATE | INITIALS | SIGN. | SCALE | ORIG.SIZE | TOTAL PAGES |
|---|---|---|---|---|---|---|
| DRAWN | 04.09.2021 | VISHWARTH | | 1:50 | A4/A1/A0 | 1 |
| CHECKED | 04.09.2021 | SG | | DWG NO.: GSS–ST–GA–112 | | PAGE 1 / REV. 0 |
| ENGINEER | 04.09.2021 | SG | | | | |
| APPROVED | 04.09.2021 | SG | | | | |

CONSTRUCTION STAGE CONSTRUCTION DRAWING

SHEET SIZE - A0