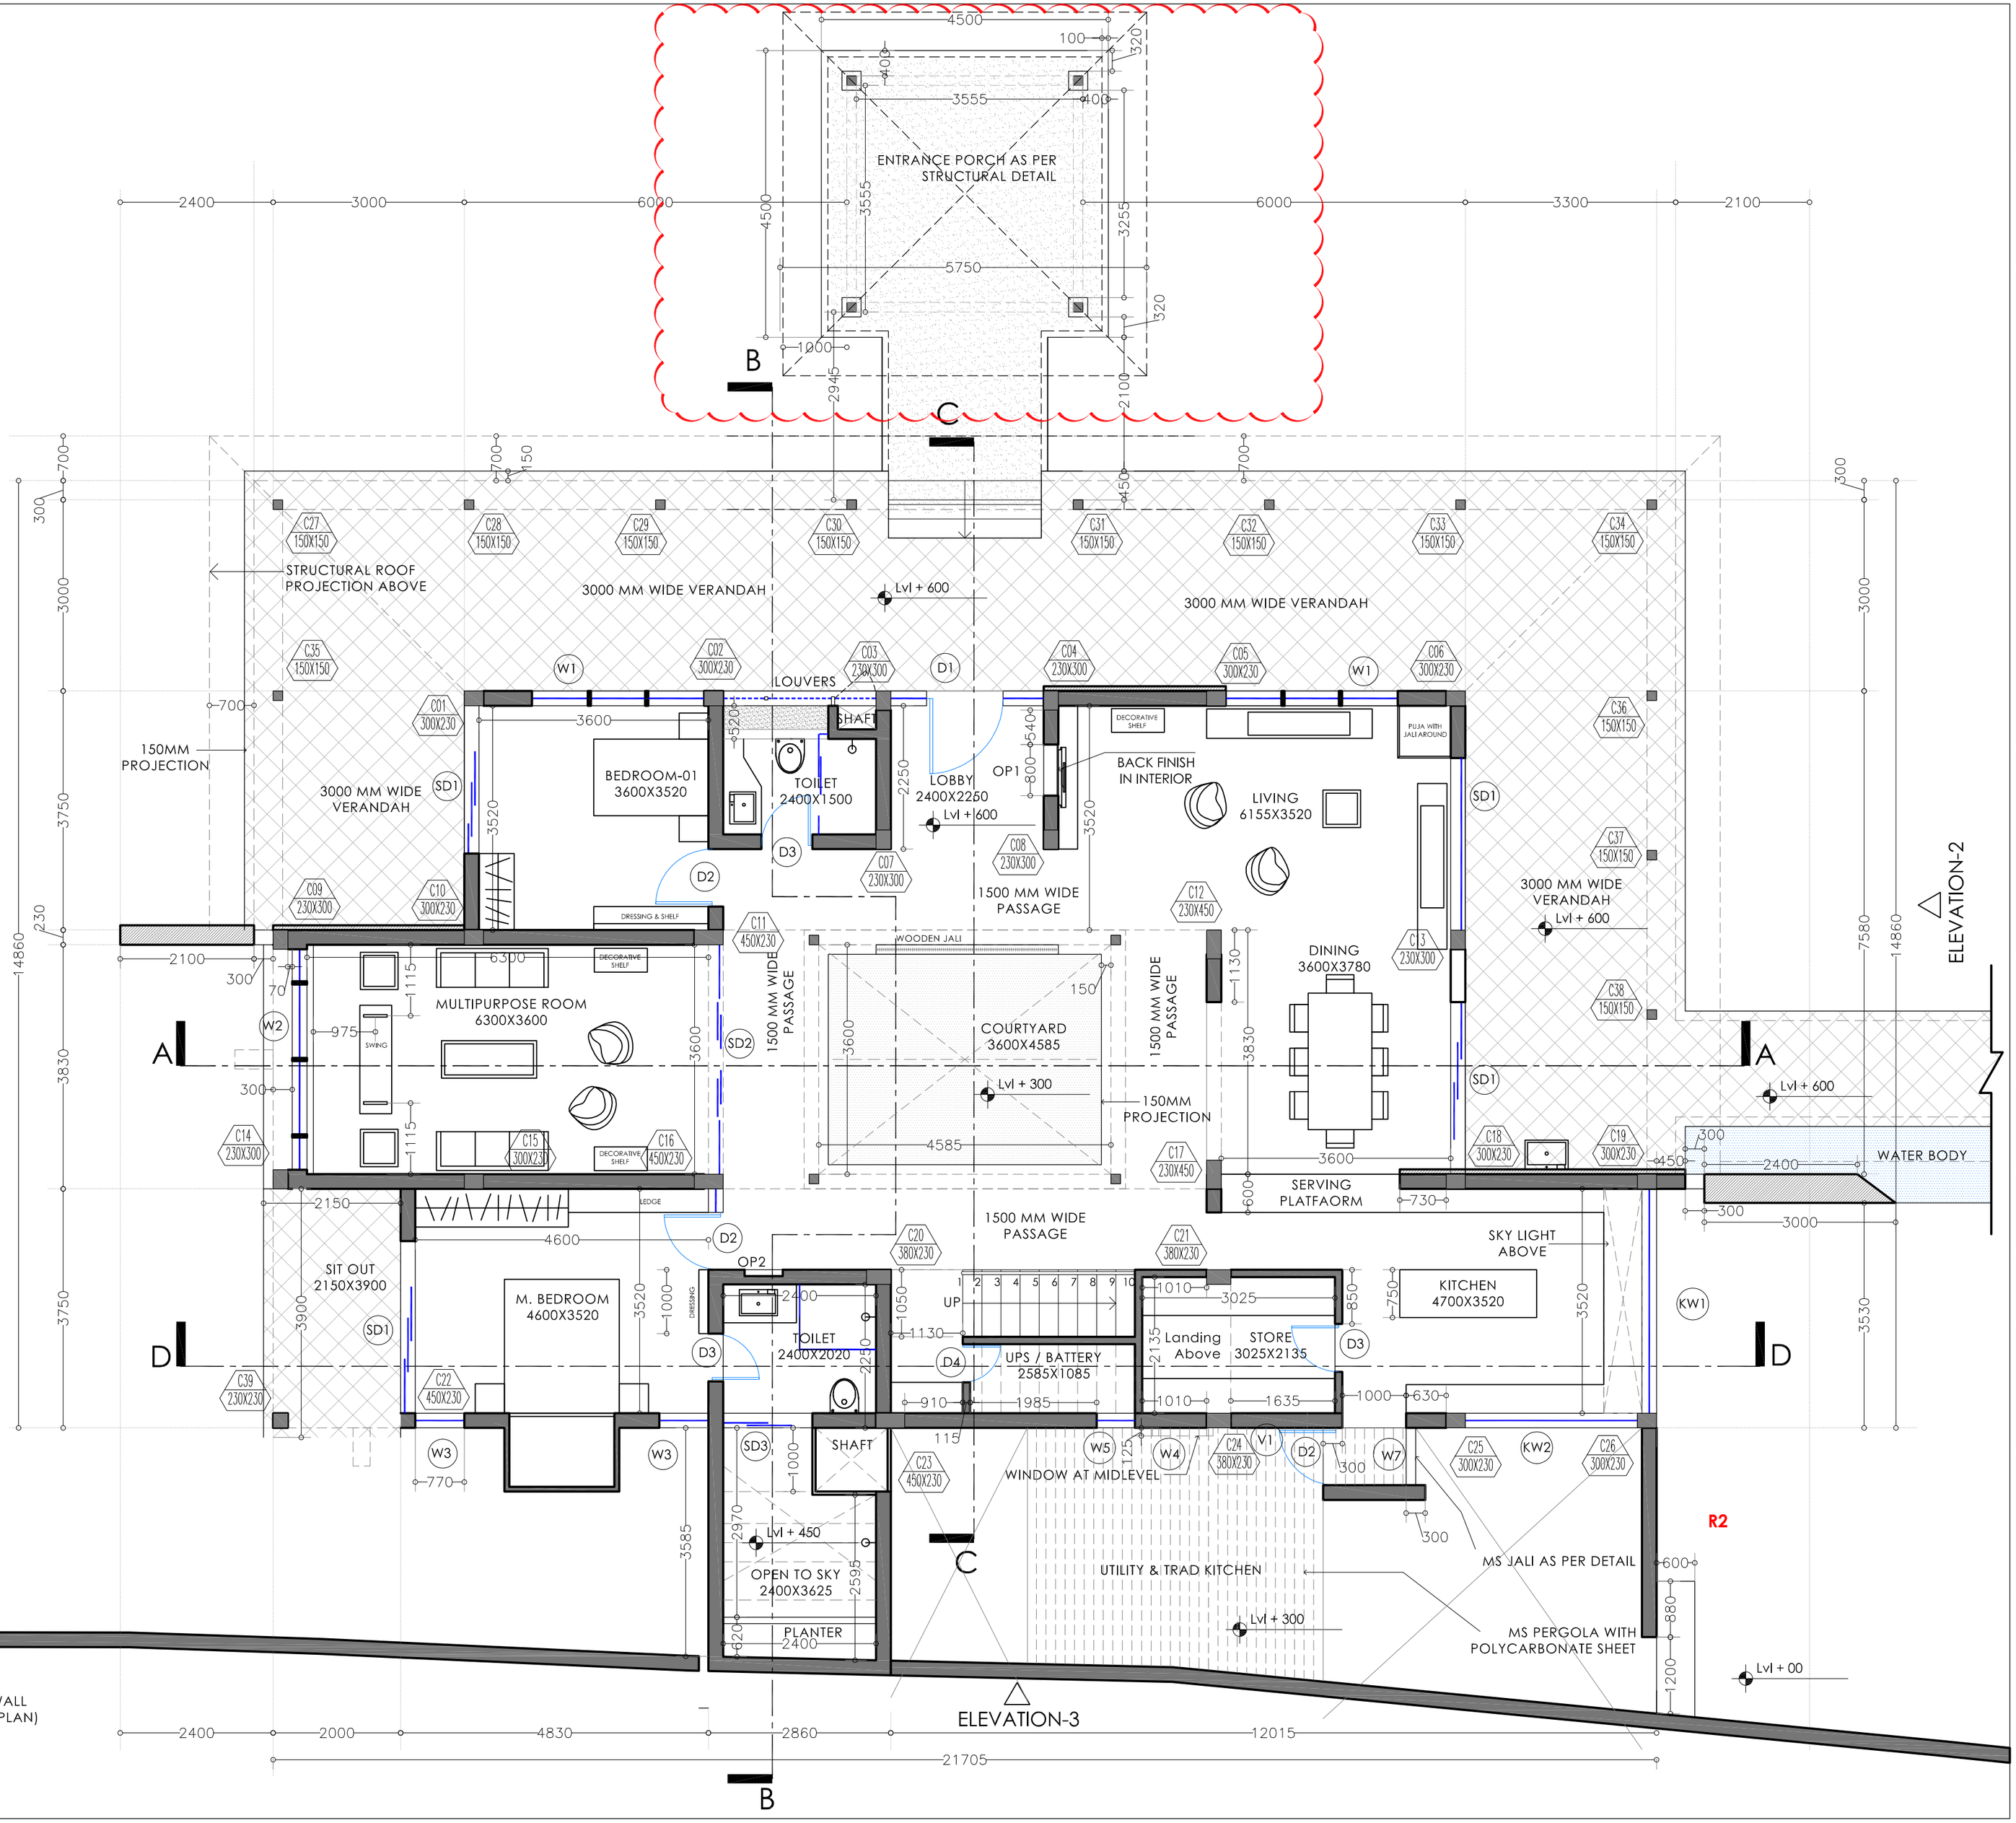


COPYRIGHT NOTE :-

THIS DRAWING IS SOLE PROPERTY OF DESIGN CONSULTANTS ARCHITECTS PVT. LTD. AND THE COPYRIGHT OF THIS DRAWING SHALL REMAIN WITH US. THIS DRAWING MUST NOT WITHOUT OUR CONSENT BE SHOWN TO ANY PERSON OUTSIDE THE RECIPIENT, EMPLOYER OR BE COPIED OR ALTERED OR USED FOR THE PURPOSE OF CONSTRUCTION OR MANUFACTURING ANY ARTICLE SHOWN IN THIS DRAWING. THIS DRAWING ALONG WITH COPIES MADE BY THE RECIPIENT SHALL BE RETURNED ON DEMAND TO US.

NOTES :

1. ALL DIMENSIONS ARE IN Mtr
2. ONLY WRITTEN DIMENSIONS ARE TO BE FOLLOWED
3. ALL LEVELS INDICATED IN THE DRAWING ARE FROM THE FINISHED FLOOR LEVEL
4. IN CASE OF ANY DISCREPANCY PLEASE REFER TO THE ARCHITECTS

DOOR WINDOWS OPENING SCHEDULE

D/W	WIDTH	SILL	LINTEL	NOS	LOCATION
SD1	2700	-	2400	4	LIVING, BEDROOM & MULTI-HALL
SD2	3600	-	2400	1	MULTI HALL
SD3	1400	-	2400	1	TOILET
D1	1200	-	2400	1	ENTRY MAIN DOOR
D2	900	-	2400	2	BEDROOM ENTRY
D3	800	-	2400	4	TOILET, KITCHEN & STORE
D4	600	-	2100	1	UPS / BATTERY ROOM

DOOR WINDOWS OPENING SCHEDULE

D/W	WIDTH	SILL	LINTEL	NOS	LOCATION
W1	2700	200	2400	2	LIVING & BEDROOM-01
W2	3600	750	2400	1	MULTIPURPOSE HALL
W3	770	600	BEAM BOTTOM	2	M. BEDROOM
KW1	3520	950	1425	1	KITCHEN
KW2	2700	950	1425	1	KITCHEN
W4	750	1250	2000	1	MID LANDING LEVEL
W5	600	1050	1650	1	UPS / BATTERY
V1	1200	1800	2400	1	STORE
OP1	800	1050	1850	1	LOBBY

LEGEND: FOUNDATION WALLS & PLINTH BEAMS BELOW PLINTH LEVEL

	230 MM THK BRICK WORK
	115 MM THK BRICK WORK
	RCC COLUMN
	VERANDAH
	COURTYARD
	TOILET AREA
	STONE WALL

ARCHITECTS SIGN AND STAMP

N

NORTH

CLIENT NAME

MR. RAJENDRA KARNE, BARAMATI.

PROJECT NAME

PROPOSED BUNGALOW AT, BARAMATI

DRAWING NAME	DRAWING NO.
GROUND FLOOR PLAN	DC-006 (R4)

SR.NO.	REVISIONS	DATE	DRAWN BY
R1	south windows & stone wall added	18 / 04 / 16	pankaj
R2	Utility area added	29 / 04 / 16	pankaj
R3	furniture layout added	14 / 07 / 16	pankaj
R4	porch added	30 / 08 / 16	pankaj

STATUS	GOOD FOR CONSTRUCTION
DATE :	20/02/16
SCALE :	1:75 (Size-A2)
DRAWN BY	YOGENDRA
CHECKED BY	PANKAJ

R2

Design Consultants Architects Pvt. Ltd.

Website:www.dcapl.net
E-mail: dc@dcapl.net
Tel.: +91-20-25411470 Fax: +91-20-25422819