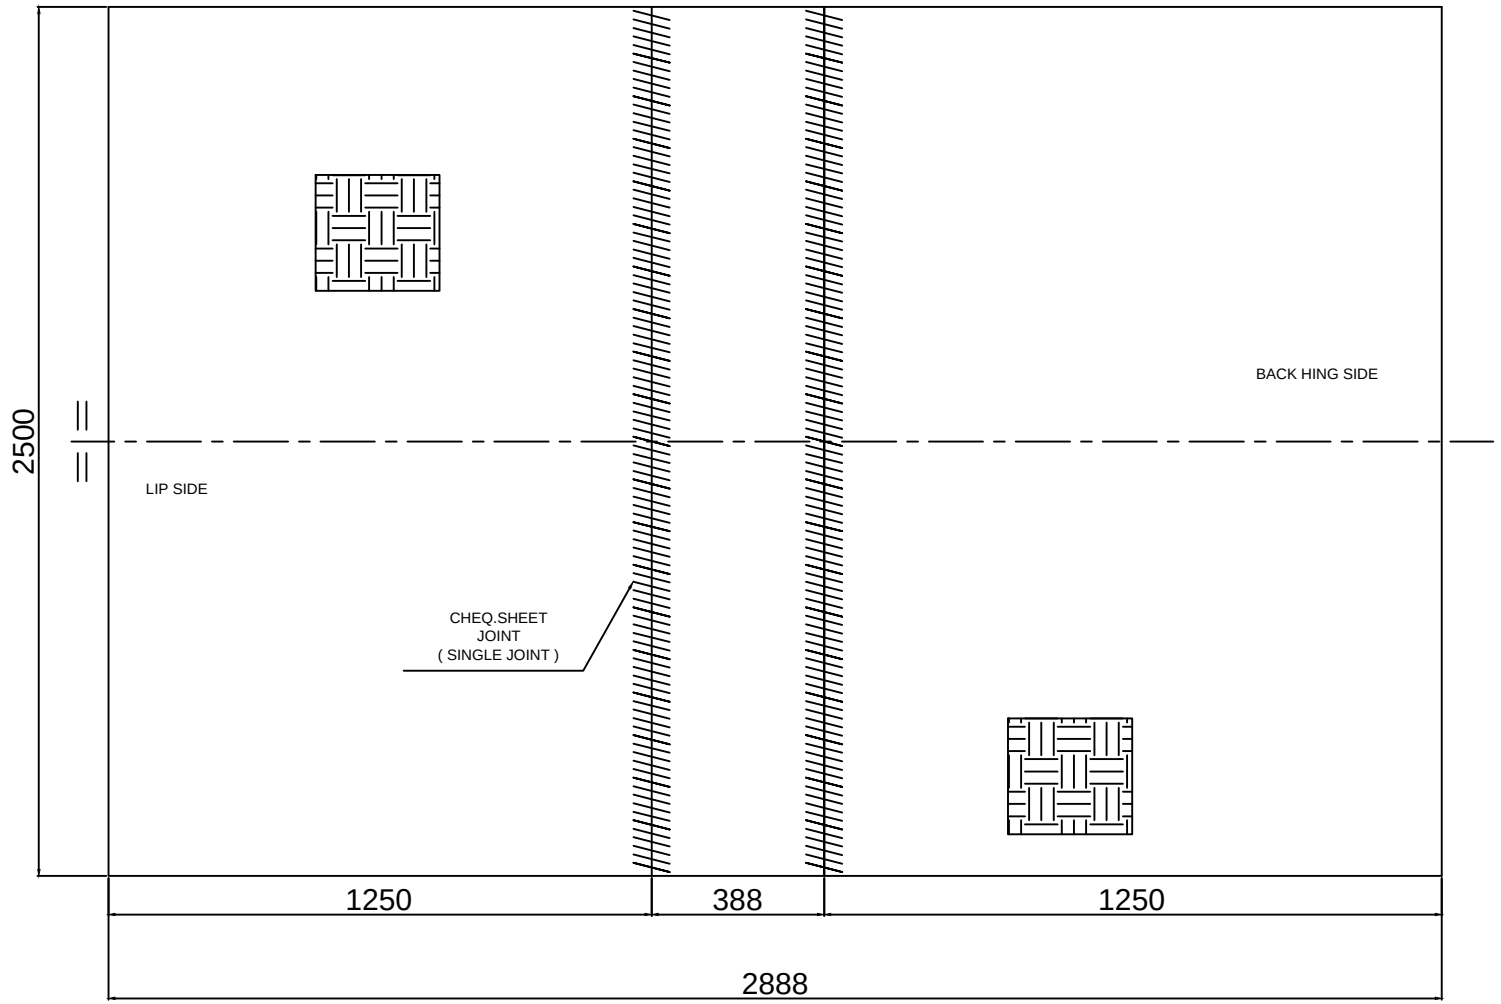

This drawing & design is the property of NIHVA TECHNOLOGIES. Not to be sold or copied to any other concern.

TITLE

DECK CHEQ.SHEET

	NAME	SIGN	DATE
DRAWN	P.A		12.12.18
CHECK	P.A		12.12.18
APPRD.	P.A		12.12.18

If any queries contact : design@nihva.com

ALL DIMENSION ARE IN mm

NIHVA TECHNOLOGIES PVT. LTD.

NIHVA TECHNOLOGIES PVT. LTD. PUNE
Tel : 020 66304033
Email:- info@nihva.com
Website:- www.nihva.com

CLIENT -

PROJECT - DLAG1010

SITE LOCATION -

DWG. NO. : NIHVA/18-19/MFG/DLAG1010/003

SCALE: NTS | WT: | REV- 00