

NOTE : ~ PLEASE MAINTAIN 7 MM GAP BETWEEN TWO LIP BUSHES.

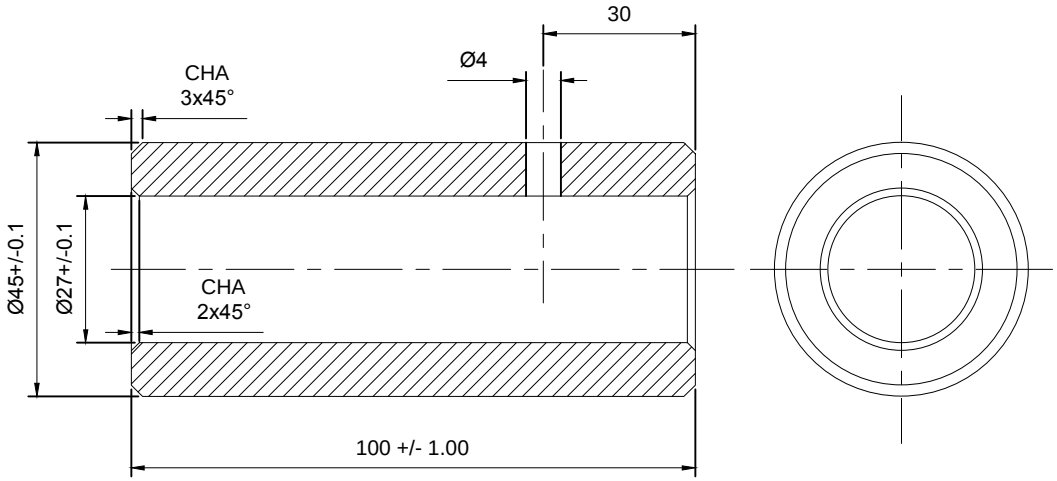

NOTE:~ MTL : MS

BUSH Ø45 X 103L = 15 NOS

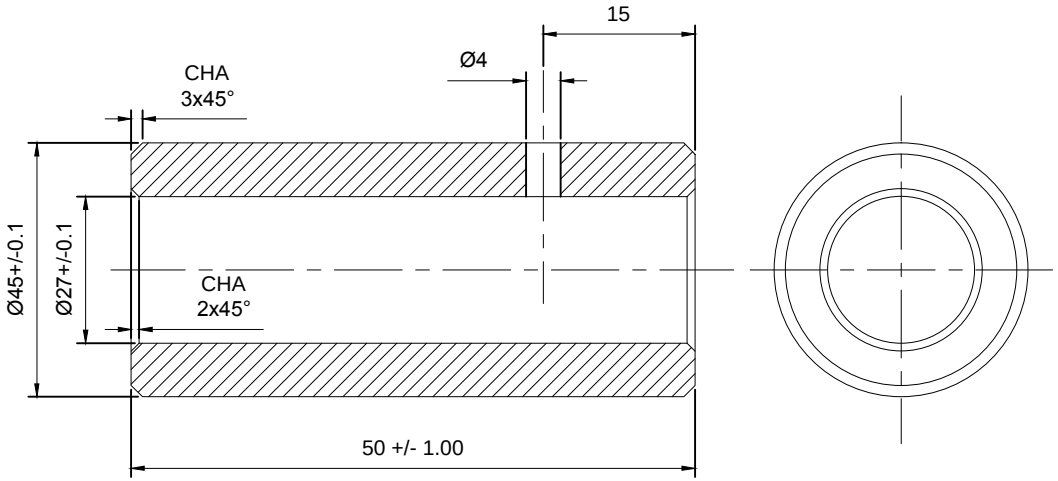

NOTE:~ MTL : MS

BUSH Ø45 X 53L = 10 NOS

This drawing & design is the property of NIHVA TECHNOLOGIES. Not to be sold or copied to any other concern.

TITLE				
LIP MOUNTING BUSH				NIHVA TECHNOLOGIES PVT. LTD.
	NAME	SIGN	DATE	
DRAWN	P.A		10.01.2020	CLIENT -
CHECK	G.J		10.01.2020	PROJECT -
APPRD.				SITE LOCATION -
If any queries contact : design@nihva.com				DWG. NO. : NIHVA/19-20/VDR/292
ALL DIMENSION ARE IN mm				SCALE: NTS / WT: / REV- 0

NIHVA TECHNOLOGIES PVT. LTD. PUNE
Tel : 020 66304033
Email:- info@nihva.com
Website:- www.nihva.com