



DRAWING

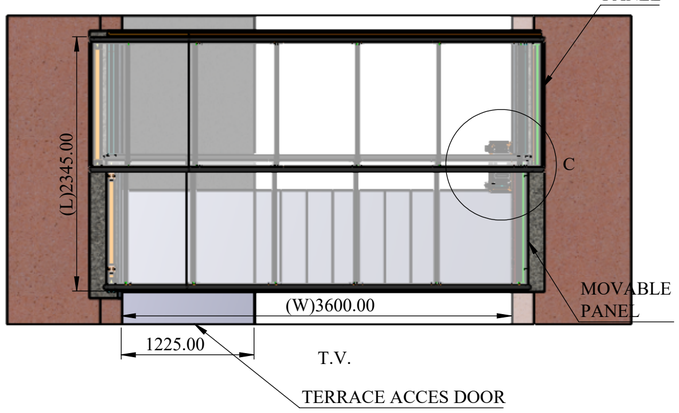

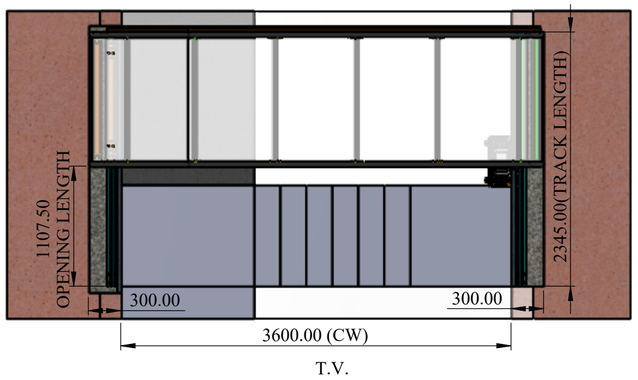


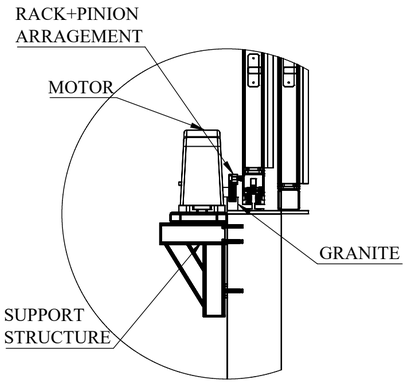


DETAIL A
SCALE 1 : 16

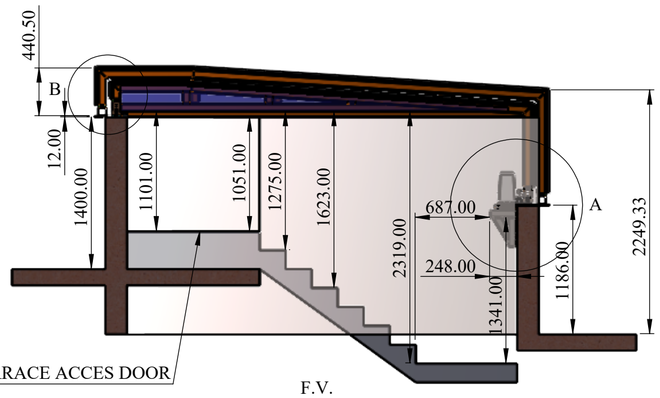


F.V.

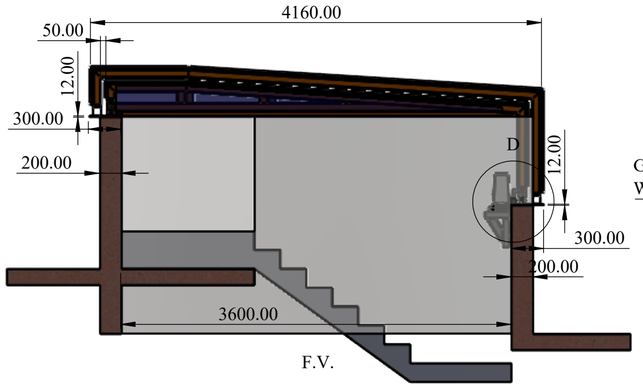


F.V.

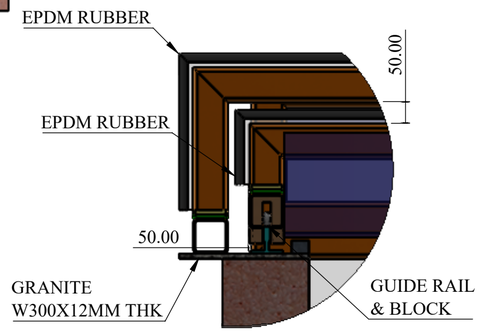

DETAIL B
SCALE 1 : 10

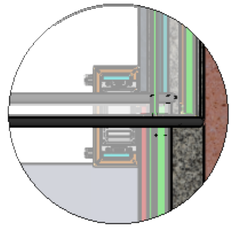


DETAIL C
SCALE 1 : 20

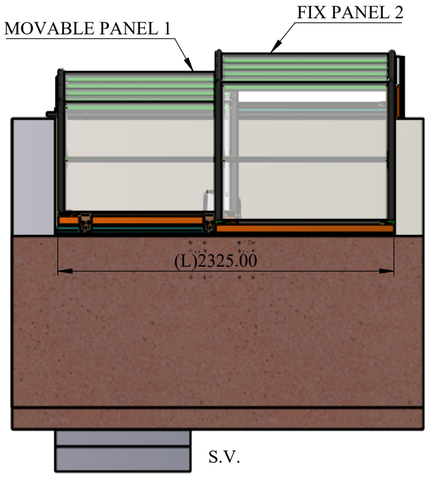


S.V.

CLOSE VIEW

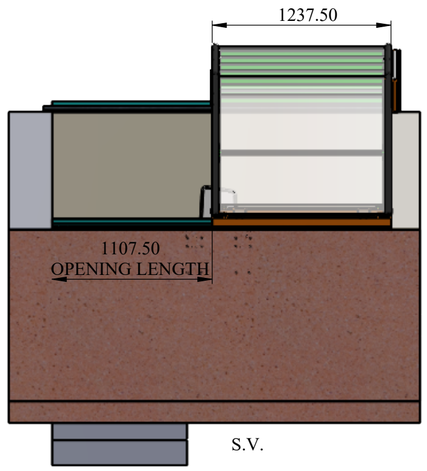

S.V.

OPEN VIEW

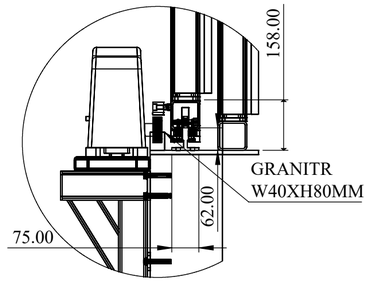

MOTOR MOUNTING
ARRANGEMENT

DETAIL D
SCALE 1 : 12

REV DESCRIPTION	DATE	REV NO
	19-08-2026	REV 00
1.		

NOTE :

THIS DRAWING IS ONLY FOR CLIENT APPORVAL
REQUIRED TRACK MOUNTING BASE STRUCTURE IN CLIENT SCOPE
EPDM RUBBER FLAPPER IS PROVIDED FOR AIR & WATER SEAL
TOTAL SYSTEM WEIGHT - 2,040 KG

SPECIAL INSTRUCTION'S :

This drawing & design is the property of NIHVA TECHONOLOGIES PVT. LTD. Not to be sold or copied to any other concern

TITLE - ROOF AUTOMATION

DWG NO - NTPL-

NIHVA TECHNOLOGIES PVT.LTD.PUNE
Website - www.nihva.com

	NAME	SIGNATURE	DATE
DRAWN	V.W.		19-08-2026
CHK'D	S.P.		21-08-2026
APPV'D	V.T.		21-08-2026

PRODUCT - RECTRACTABLE ROOF
CLIENT NAME - LODHA GROUP.
SITE LOCATION - MUMBAI - VIKROLI.
MATRIAL - | QTY - 1
If any queries contact - info@nihva.com
PROJECTION METHOD:
SCALE :
ALL DIMENSION ARE IN mm | A2
SHEET 1 OF 1