




SIDE VIEW

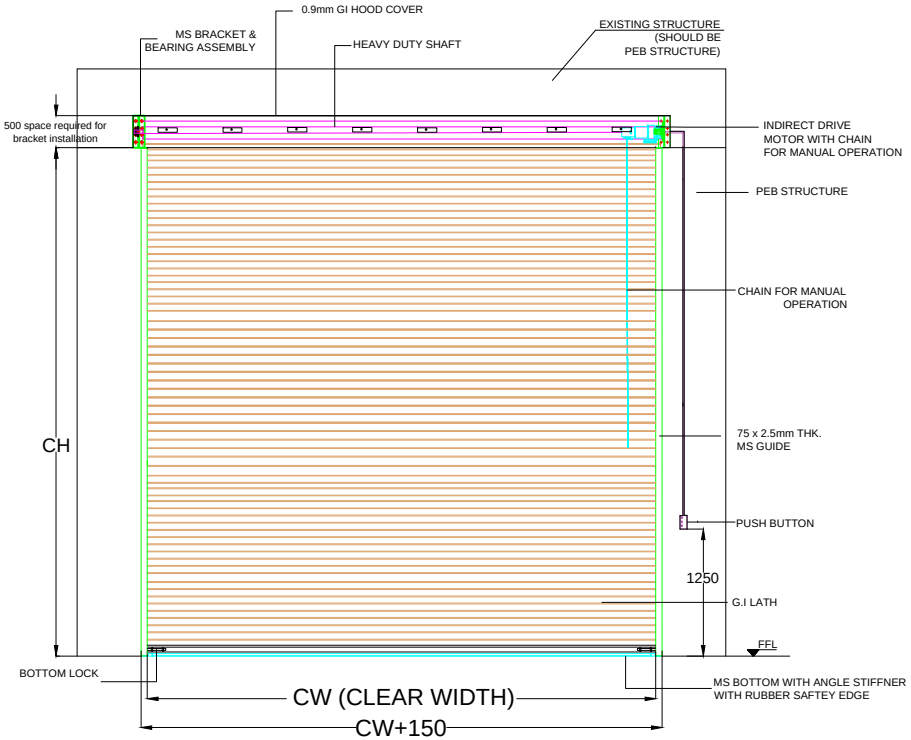


ELEVATION

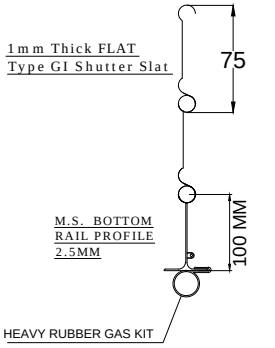

M.S. BOTTOM RAIL PROFILE 2.5MM

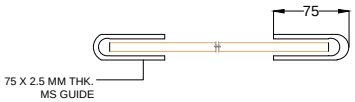

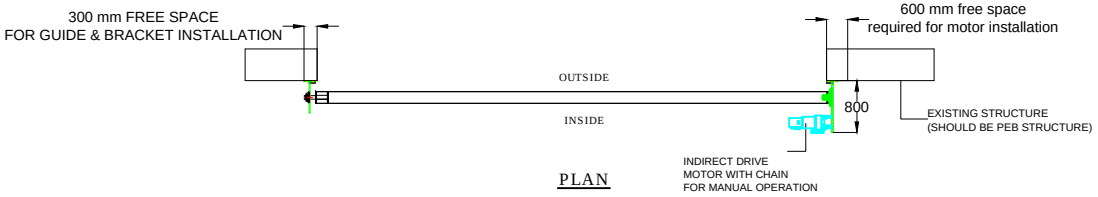

PLAN

NOTE:
1. NO OF SLATS : 4000 X 5000 = 1 NO (80 NOS SLATS)
2. NO OF SLATS : 2500 X 3000 = 3 NOS (50 NOS SLATS PER SHUTTER)
3. POWDER COATING : RAL 9001 (WHITE GRAY)

TOLERANCE - ±10mm

CLEAR WIDTH	CLEAR HEIGHT	QTY.
4000mm	5000mm	01NO
2500mm	3000mm	03NOS

This drawing & design is the property of NIHVA TECHNOLOGIES. Not to be sold or copied to any other concern.

TITLE
MOTORISED ROLLING SHUTTER

	NAME	SIGN	DATE
DRAWN	SURAJ		18-12-2018
CHECK	PRADEEP		18-12-2018
APPRD.	PRADEEP		18-12-2018

NIHVA TECHNOLOGIES PVT. LTD.
Website:- www.nihva.com
NIHVA TECHNOLOGIES PVT. LTD. PUNE
Tel : 020 66304033
Email:- info@nihva.com

CLIENT -

PROJECT -

SITE LOCATION - CHAKAN

If any queries contact : design@nihva.com

DWG. NO. : NIHVA/18-19/VDR/295 | REV- R01

ALL DIMENSION ARE IN mm | SCALE: NTS | WT: | SHEET: 01 OF 01