


Abbrevation's:
WOW-Wall Opening Width
WOH-Wall Opening Height
CH- Clear Height
UC-Under Cut
FFL-Finished Floor Level

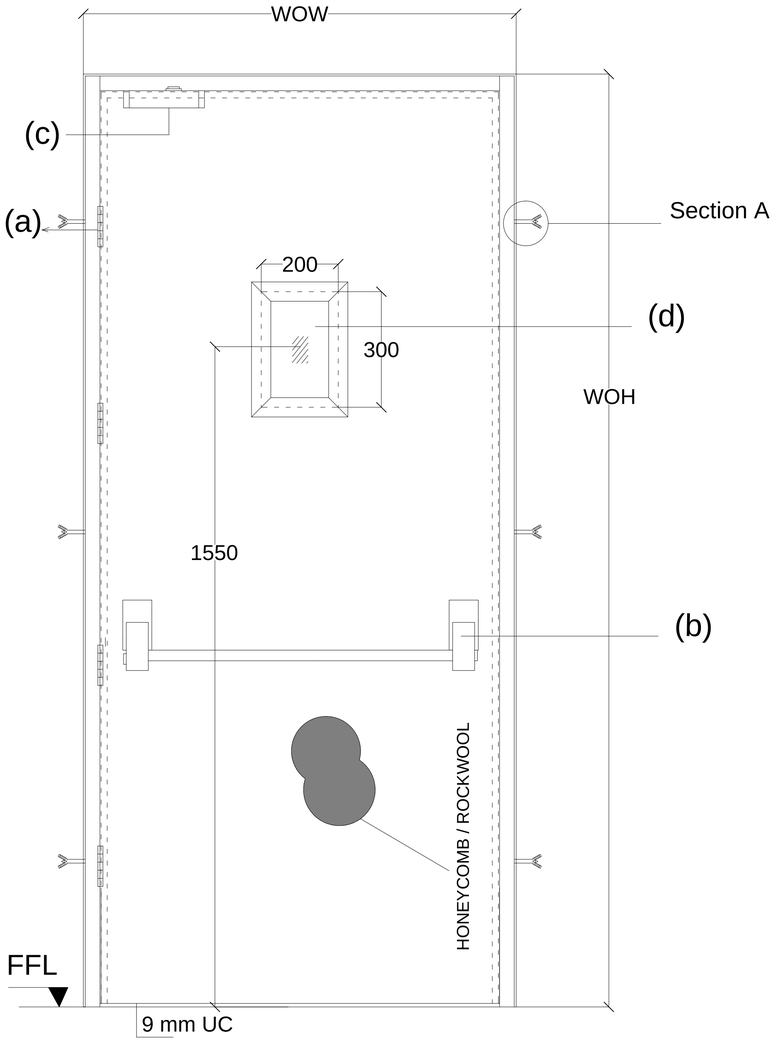

ELEVATION

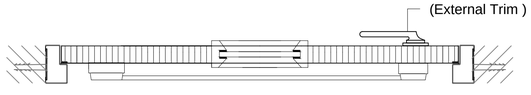

Top View

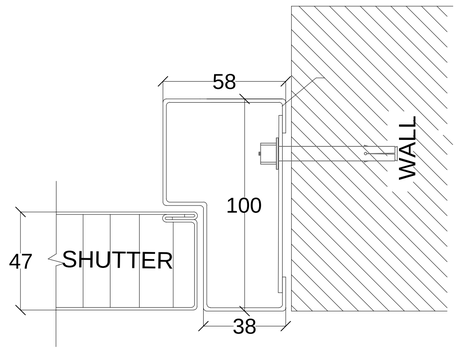

ASSESORIES DETALES

(a) HINGES: SS hinges 100x75x3mm

(b) LOCK : Mortise Lock with half cylinder.
Panic Bar
Outer trim

(c) DOOR CLOSER : F 8500

(d) VISION PANEL- 5mm THK. FIRE GLASS SIZE- 200X300mm.

Shutter thickness : 47 mm
Frame Sheet thick : 1.20mm
Shutter sheet thick : 0.80mm
Fixing : On Soliid Brick plasterd wall with Anchors

NOTE:- *All Dimensions are in mm.
*Tolerance:-All Linear Dimensions ±3mm,Others ±0.5mm.
*The Drawing Is For Location of Hardware only. Drawing Does Not Represent The Hardware For More Clarity, Please Go Through Hardware Broucher.

Fire door size						
WOW	WOH	TYPE 1	TYPE 2	TYPE 3	TYPE 4	QUANTITY
1198	2977					1

NOTE- CLIENT SHOULD SELECT DOOR TYPE FROM DOOR HANDLING SHEET & COLOR OF DOOR.

This drawing & designing is the property of NIHVA TECHNOLOGIES. Not to be sold or copied to any other concern.

TITLE FIRE RATED DOORS

NIHVA TECHNOLOGIES PVT. LTD.
NIHVA TECHNOLOGIES PVT. LTD. PUNE
Tel : 020 66304033
Email:- info@nihva.com
Website:- www.nihva.com

	SIGN	DATE
DRAWN	OMKAR	11/07/17
CHECK	SHEKHAR	11/07/17
REV.	00	
APPROVAL		

CLIENT - VAICHAL CONSTRUCTION
PROJECT - TAGMA CENTRE
SITE - CHAKAN
DWG. NO. : NIHVA/17-18/0129
If any queries contact : projects@nihva.com
SCALE: NTS | WT: | SHEET: 01 OF 01
ALL DIMENSION ARE IN mm